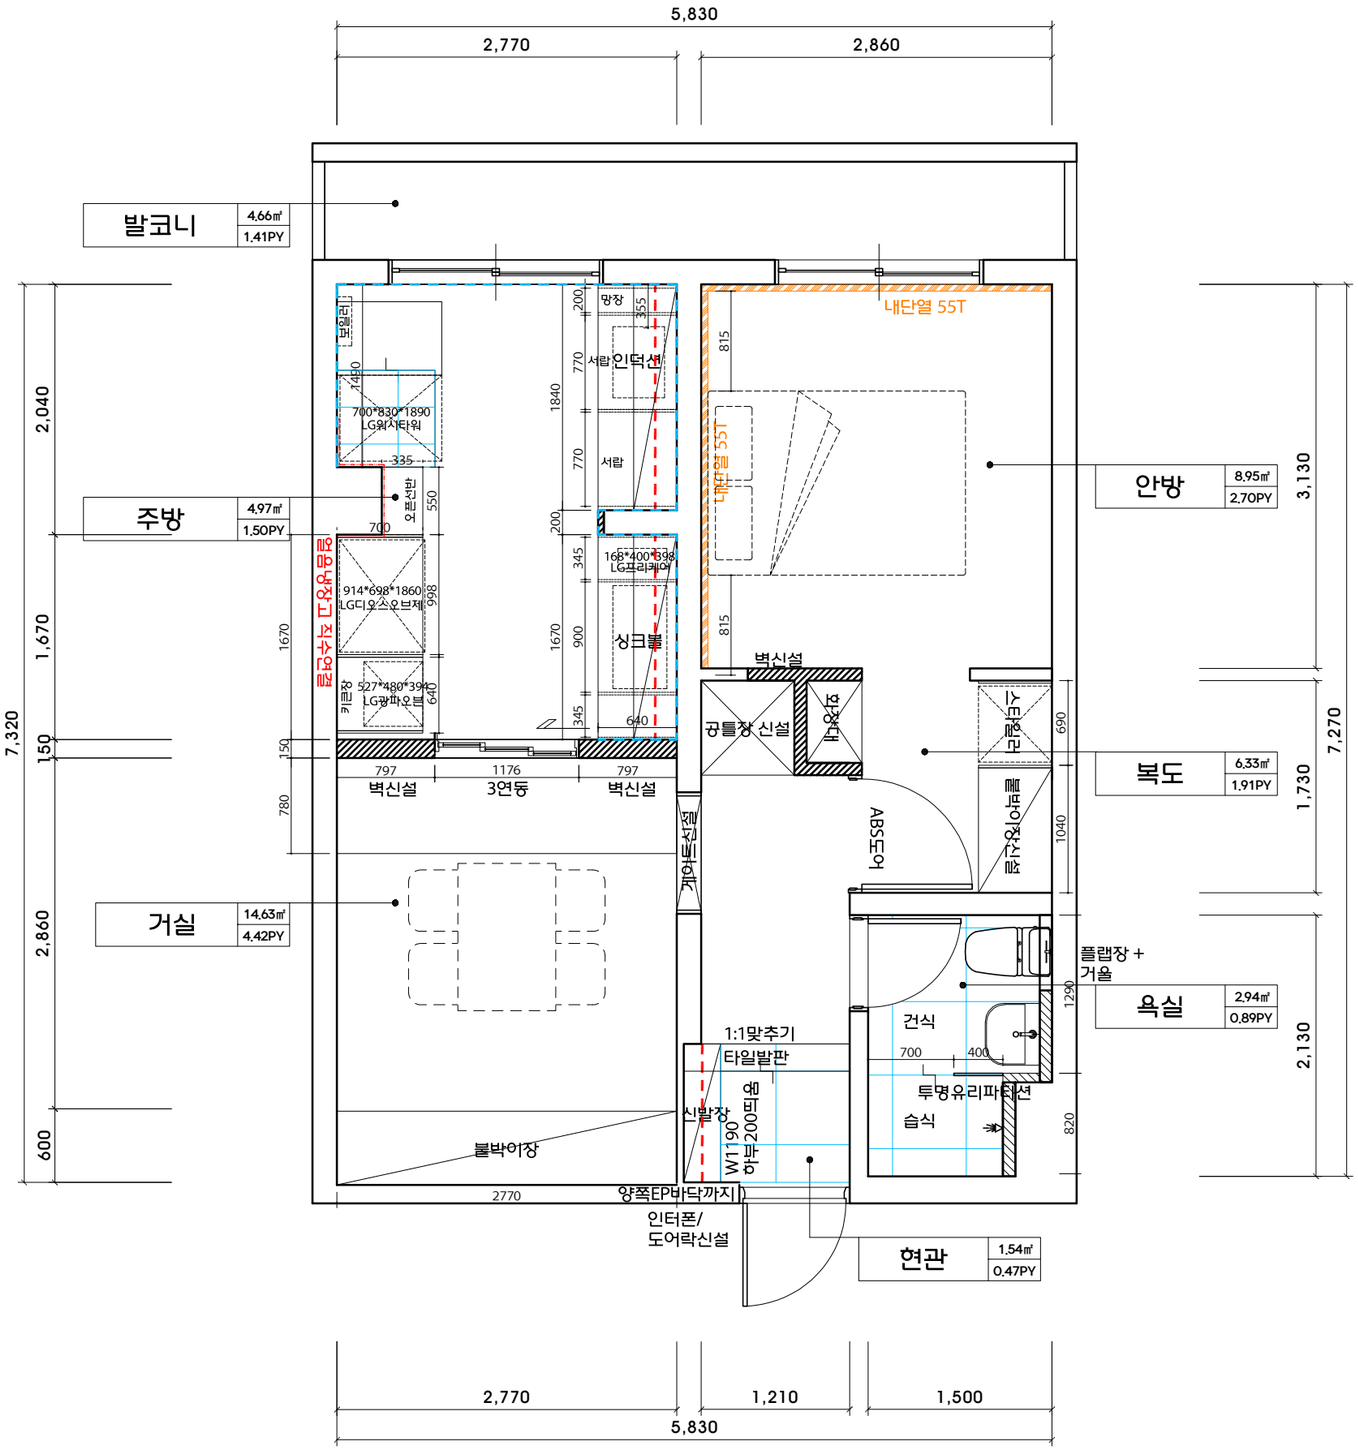


DESIGN BY.

M2

디 자 인 엠 제 곱

@_m2design_

m2gmg@naver.com

REMARK.

*철거

도어셋(욕실,거실)-2SET
안방우물천정
욕실:벽, 바닥 전체철거,
주방벽타일, 현관바닥철거
가구:안방/거실 붙박이장, 신발장
기타:에어컨부분 철거, 걸레받이,몰딩
빨래건조대,전기 조명, 콘센트외 철거

욕실도어세트, 거실 게이트,커텐박스
안방천정 평탄화, 에어컨 등박스
도배:베스띠(따뜻한 화이트)
바닥:강마루
가구:거실 붙박이(화장대포함),
복도 붙박이, 신발장
필름공사:창호, 방화문뒷면
기타:인터폰,도어락,(안정고리X,말발굽X)
시스템 에어컨 2대

SITE CONDITIONS.

ADDRESS.

제주시 원노형5길 34
재영샤르빌1002

AREA.

48.10 m2 / 14.55py

HEIGHT.

2250~2300mm(거실)

PROJECT TYPE.

오피스텔 리모델링

PROJECT TITLE.

재영샤르빌1002호

DRAWING TITLE.

평면도

SCALE.

A1:1/25 A3:1/50

DATE.

25. 02. 20

DRAWN BY.	CHECKED BY.
YOURNAME	

DRAWING No.	SHEET No.
I-000	000

- 본 도서는 어떠한 경우에도 무단으로 도용할 수 없으며 도용시 '지적재산권' 보호에 관한 법률에 의거, 법적 분쟁이 발생합니다. 또한 본 도서에 관한 모든 저작권은 당사에 있습니다. -