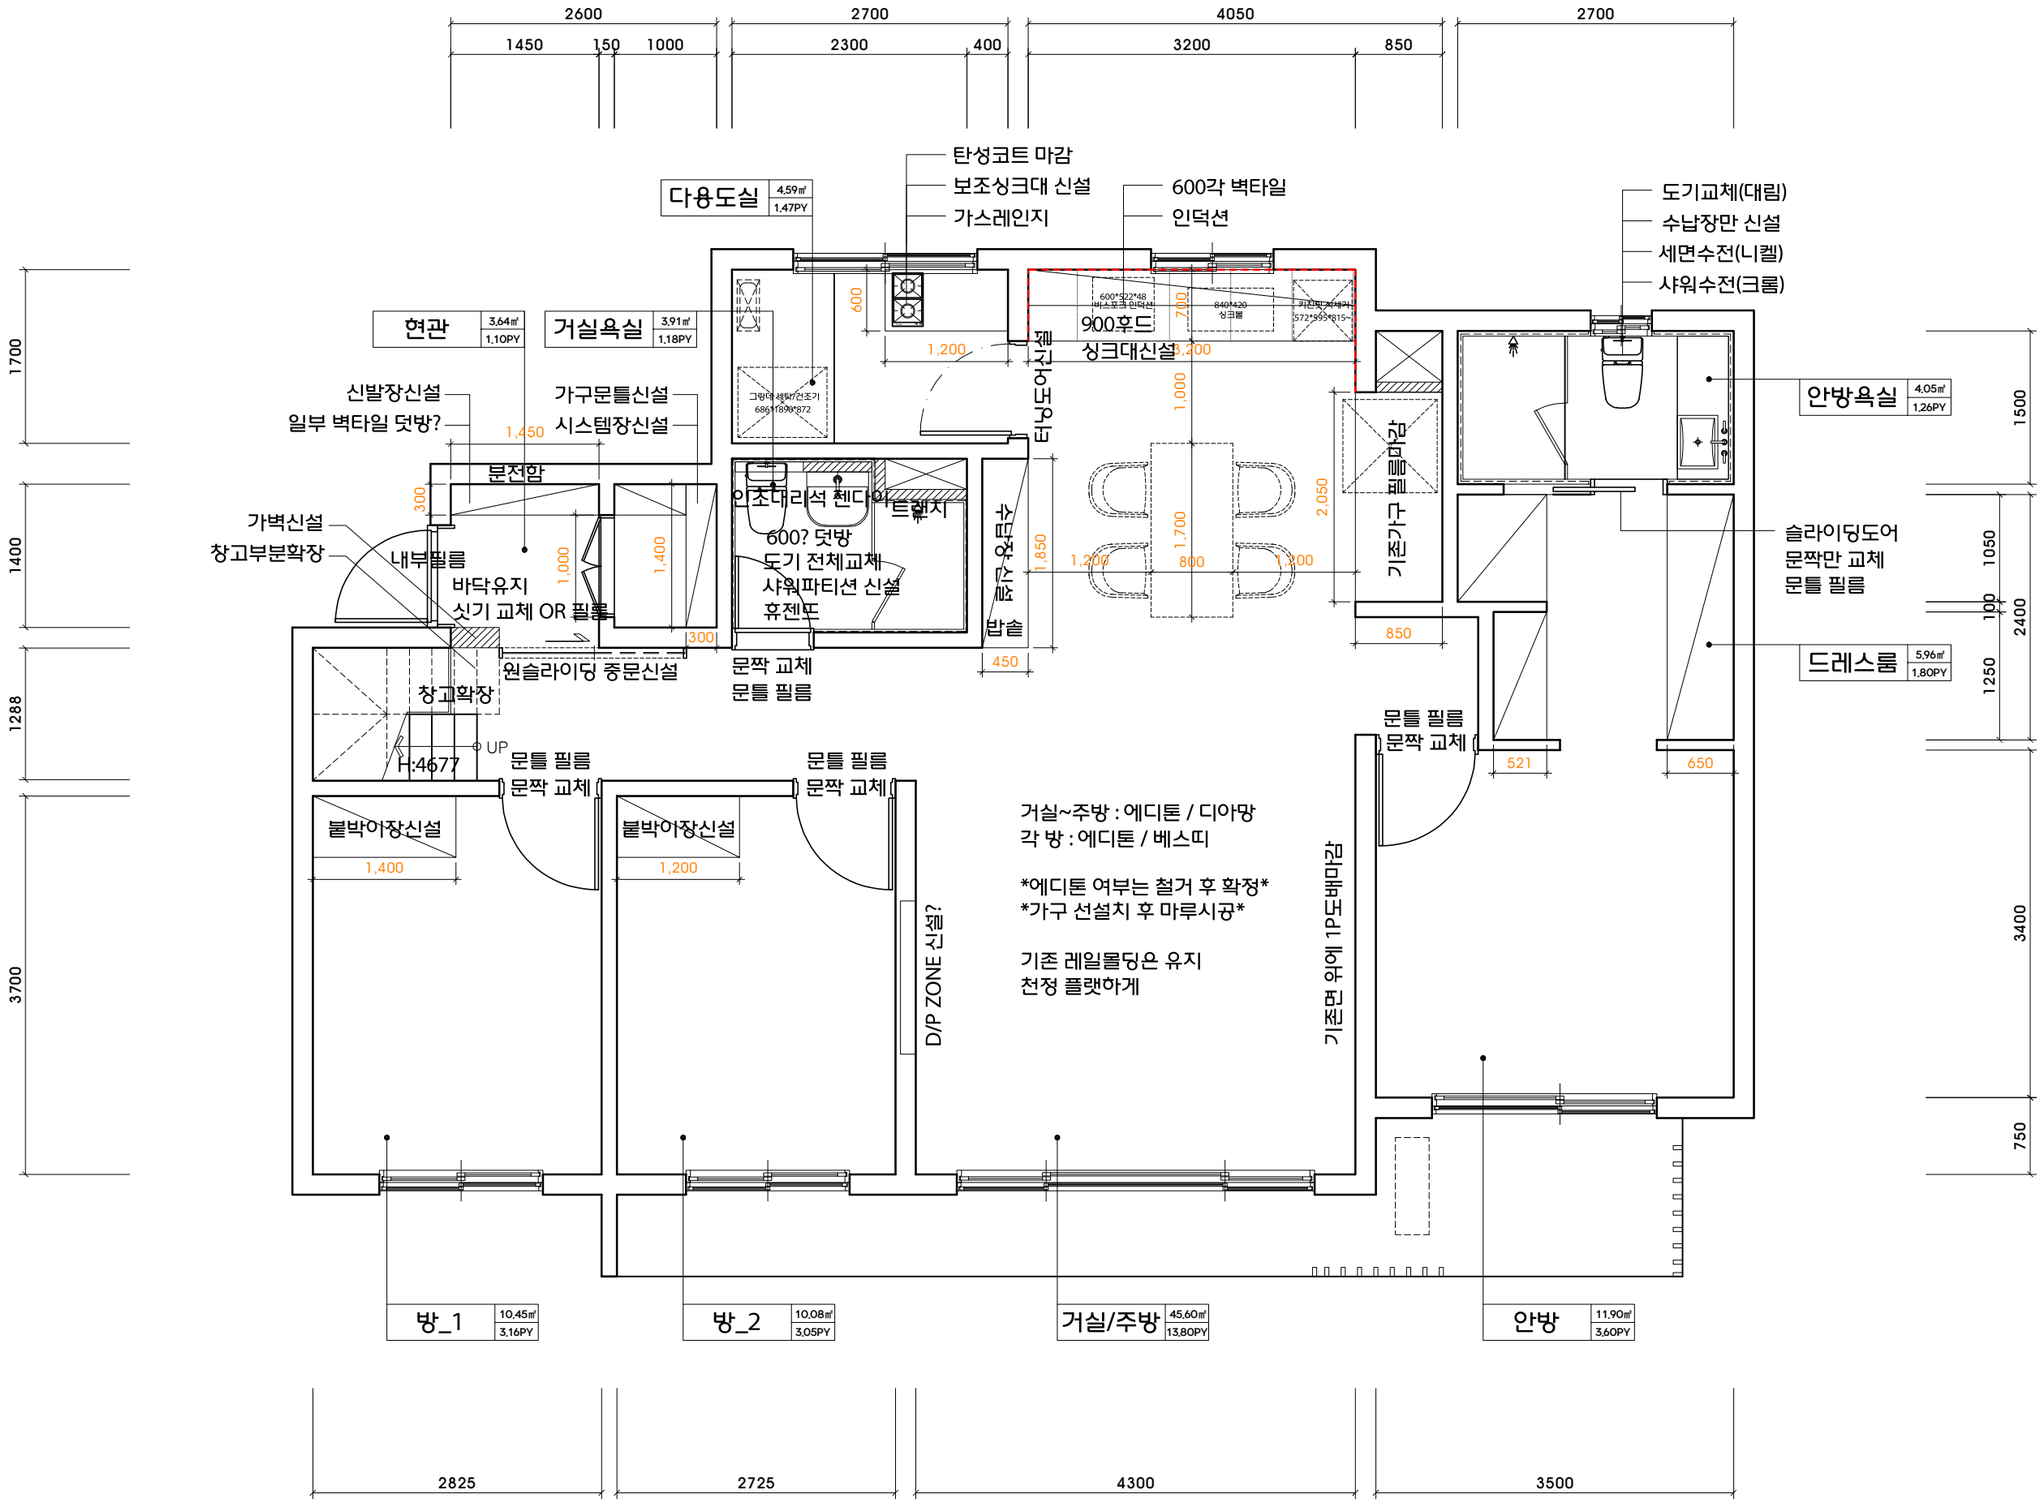


DESIGN BY.

GM
황 금 손 인 테 리 어

@__gmdesign__
goldenhand99@naver.com

*보조주방 가스관(h:980)
-가스관노즐적게 보이게
-방 몰딩사진 필요(액자레일유지)
-거실9T 합판마감
-D/P ZONE 테두리 라운드몰딩
-필름(안방욕실 슬라이딩 모노크림

*전기-현관일괄소등,매입,엣지,
인덕션/휴젠트 단독선(확인요망)
현관에 일괄스위치 신설
*목공:도어,거실벽체, 창고부분?
2층 누수벽체,중문인방마감
아트월 : 면치고 도배마감
*타일-안방욕실(샤워수전,변기,
세면대수전)
-거실욕실:덧방시 유가유무 확인?
450*600점검구,조명위치,
휴젠트위치?타일마감 코너비트
*필름-문틀,냉장고빌트인가구,
D/P ZONE, 현관장공틀장
*가구-빌트인가구 걸레받이 가구
할때 컷팅

SITE CONDITIONS.

ADDRESS.
연삼로 197-7
헤르지아하임1차 103동 302호

AREA.
106.65m2 / 32.26py

HEIGHT.
2350mm

PROJECT TYPE.
103-302

PROJECT TITLE.
연삼로 197-7

DRAWING TITLE.
평 면 도

SCALE.
A1:1/30 A3:1/60

DATE.
24.11.22

DRAWN BY.	CHECKED BY.
DRAWING No.	SHEET No.

- 본 도서는 어떠한 경우에도 무단으로 도용할 수 없으며 도용시 '지적재산권' 보호에 관한 법률에 의거, 법적 분쟁이 발생합니다. 또한 본 도서에 관한 모든 저작권은 당사에 있습니다. -