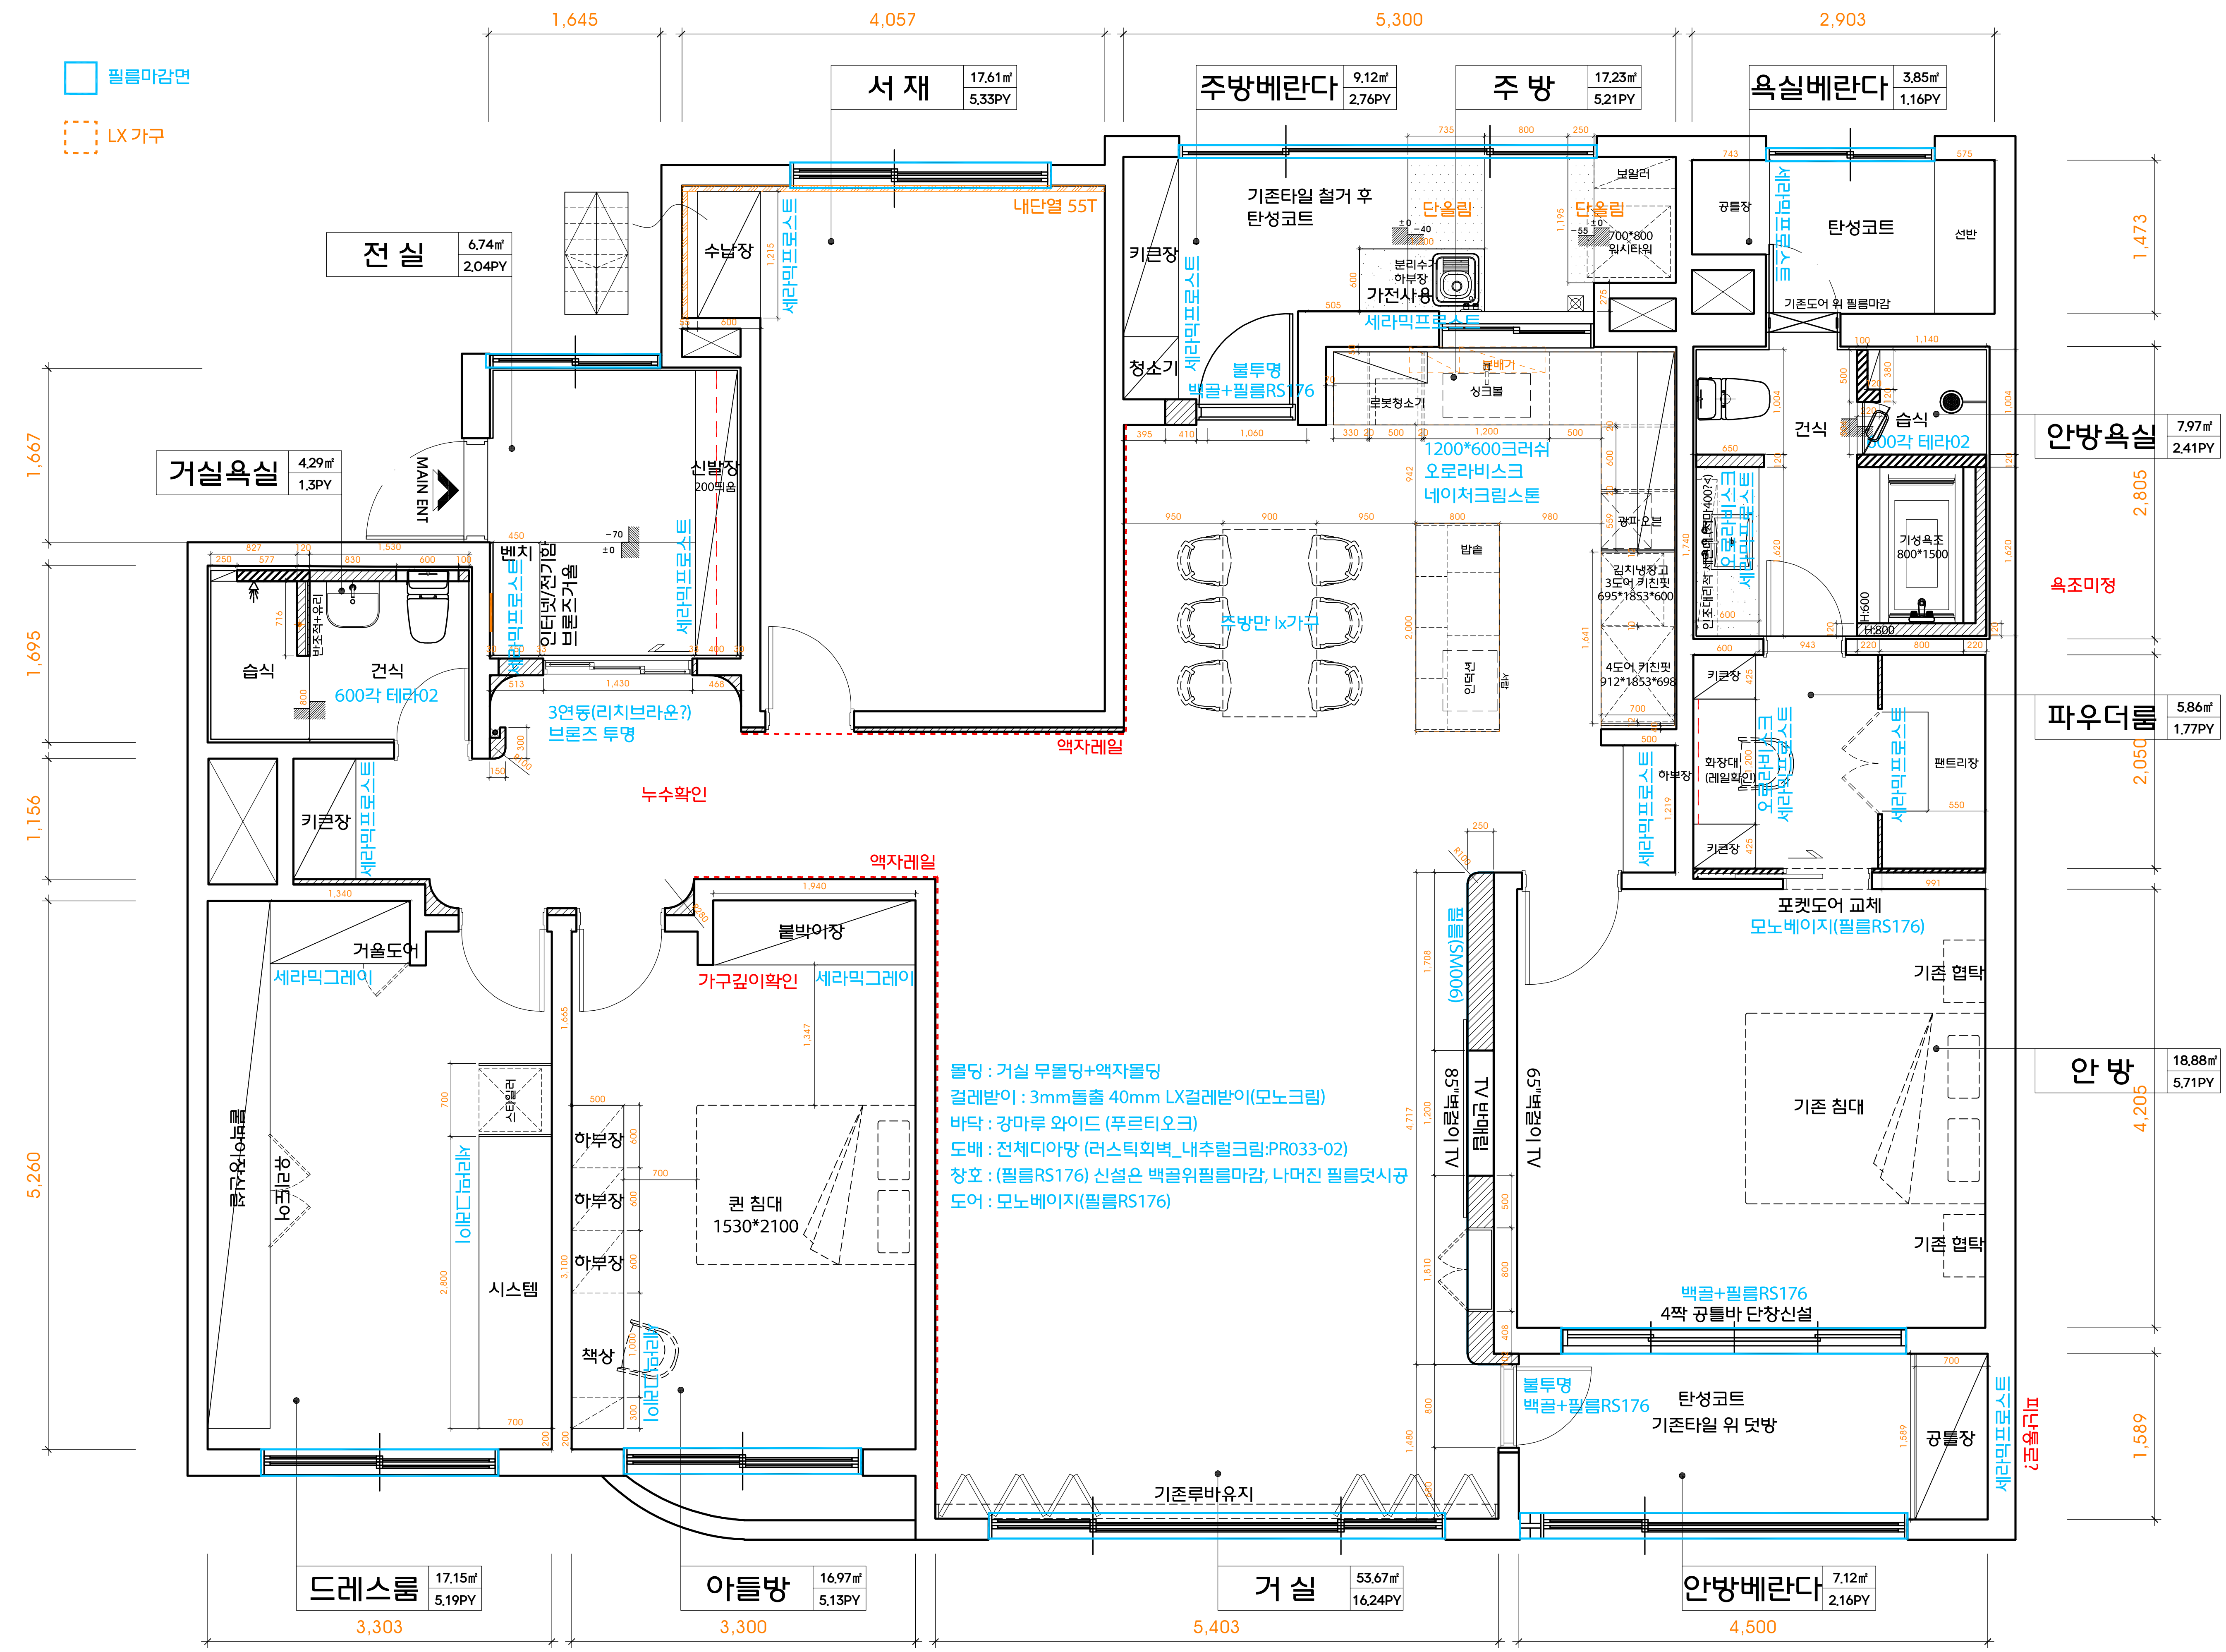

필름마감면
LX 가구
1,645
4,057
5,300
2,903
서 재 17.61㎡ 5.33PY
주방베란다 9.12㎡ 2.76PY
주 방 17.23㎡ 5.21PY
욕실베란다 3.85㎡ 1.16PY
전 실 6.74㎡ 2.04PY
거실욕실 4.29㎡ 1.3PY
안방욕실 7.97㎡ 2.41PY
파우더룸 5.86㎡ 1.77PY
안 방 18.88㎡ 5.71PY
드레스룸 17.15㎡ 5.19PY
아들방 16.97㎡ 5.13PY
거 실 53.67㎡ 16.24PY
안방베란다 7.12㎡ 2.16PY
3,303
3,300
5,403
4,500
1,667
1,695
1,156
5,260
1,473
2,805
2,050
4,205
1,589
MAIN ENT
수납장
세라믹프로스트
내단열 55T
기존타일 철거 후 탄성코트
단올림
키큰장
청소기
불투명 백골+필름RS176
분리수거 하부장
가전사용
보일러
700*800 워시타워
공틀장
탄성코트
선반
기존도어 위 필름마감
로봇청소기
음식물처리기
싱크볼
건식
습식
600각 테라02
1200*600크러쉬 오로라비스크 네이처크림스톤
광파오븐
밥솥
김치냉장고 3도어 키친핏 695*1853*600
4도어 키친핏 912*1853*698
기성욕조 800*1500
욕조미정
신발장 200띄움
벤치
인터넷/전기함 브론즈거울
주방만 lx가구
3연동(리치브라운?) 브론즈 투명
액자레일
누수확인
반조적+유리
키큰장
화장대 (레일확인)
하부장
팬트리장
키큰장
포켓도어 교체 모노베이지(필름RS176)
기존 협탁
기존 침대
85"벽걸이 TV
TV 매립박스
65"벽걸이 TV
(900MS)몰딩
거울도어
세라믹그레이
붙박이장
가구깊이확인
퀸 침대 1530*2100
하부장
책상
시스템
스타일러
세라믹그레이
붙박이장
백골+필름RS176 4짝 공틀바 단창신설
불투명 백골+필름RS176
탄성코트 기존타일 위 덧방
공틀장
기존루바유지

몰딩 : 거실 무몰딩+액자몰딩
걸레받이 : 3mm돌출 40mm LX걸레받이(모노크림)
바닥 : 강마루 와이드 (푸르티오크)
도배 : 전체디아망 (러스틱회벽_내추럴크림:PR033-02)
창호 : (필름RS176) 신설은 백골위필름마감, 나머진 필름덧시공
도어 : 모노베이지(필름RS176)

DESIGN BY.

GM
황금손인테리어

@_m2design_
m2gmg@naver.com

REMARK.

SITE CONDITIONS.

ADDRESS.
제주시 노형동 2585-1
미리내마을중흥S 107동 502호

AREA.
186.46m2 / 56.40py

HEIGHT.
2350mm()

PROJECT TYPE.
아파트 리모델링

PROJECT TITLE.
미리내 107동 502호

DRAWING TITLE.
평면도

SCALE.
A1:1/30 A3:1/60

DATE.
25.06.19

DRAWN BY.
CHECKED BY.

DRAWING No.
I-000

SHEET No.
000

– 본 도서는 어떠한 경우에도 무단으로 도용할 수 없으며 도용시 '지적재산권' 보호에 관한 법률에 의거, 법적 분쟁이 발생합니다. 또한 본 도서에 관한 모든 저작권은 당사에 있습니다. –