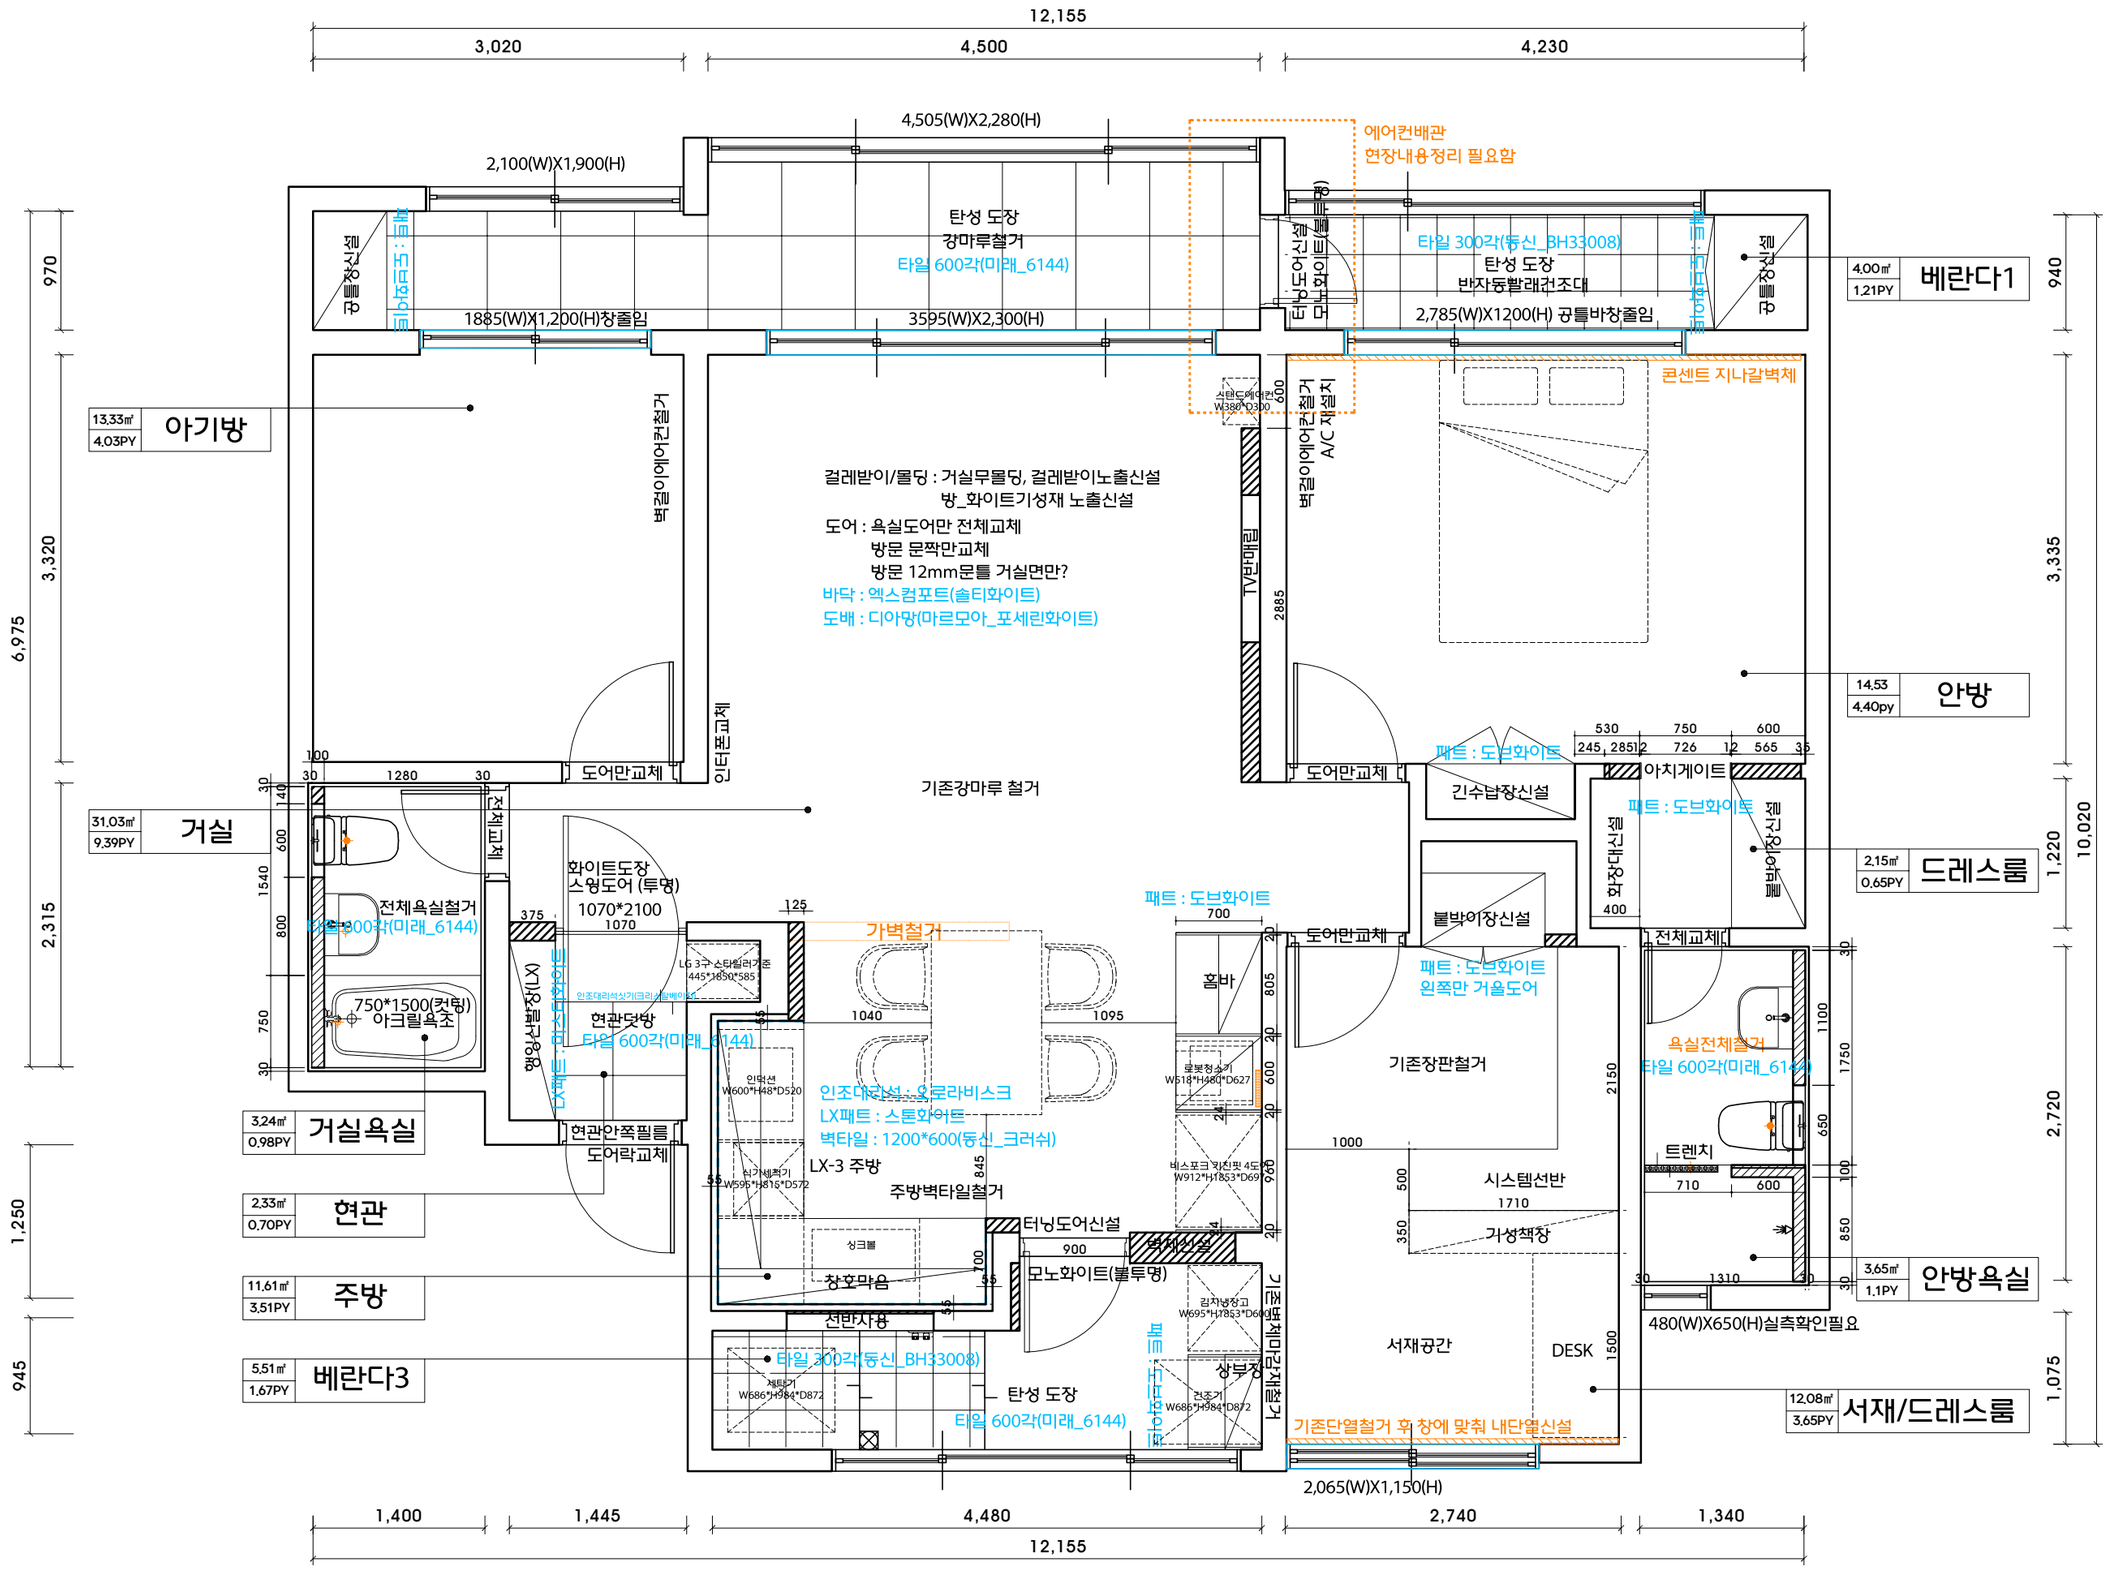


DESIGN BY.

M2
디 자 인 엠 제 곱

@_m2design_
m2gmg@naver.com

REMARK.

*철거
샷시-거실내창, 안방내창,아기방내창
주방내창, 주방내창PJ창
도어-도어(4EA), 도어셋(2)
주방벽하스리,거실 우물천정철거
안방욕실 전체철거,
거실욕실 욕조, 도기, 욕실장 철거
타일-주방베란다 바닥
가구-안방붙박이장, 화장대,
드레스룸장, 주방 싱크대
신발장, 안방/아가방 베란다 공틀장
기타-거실우물천정, 주방벽체마감재,
걸레받이,몰딩,조명,스위치,콘센트
도배지, A/C, 주방벽체 마감,기타외
방:창짠, 거실/주방:강마루철거

설비: 벽배수,배관이설
조적: 세면대 젠다이 반조적, 샴푸조적

SITE CONDITIONS.

ADDRESS.
제주시 국기로 14
연동대림1차 105동601호

AREA.
112.21m2 / 34py

HEIGHT.
2280mm()

PROJECT TYPE.
아파트 리모델링

PROJECT TITLE.
연동대림 105-602

DRAWING TITLE.
평 면 도

SCALE.
A1:1/30 A3:1/60

DATE.
25.06.16

DRAWN BY.	CHECKED BY.
DRAWING No.	SHEET No.

- 본 도서는 어떠한 경우에도 무단으로 도용할 수 없으며 도용시 '지적재산권' 보호에 관한 법률에 의거, 법적 분쟁이 발생합니다. 또한 본 도서에 관한 모든 저작권은 당사에 있습니다. -