
DESIGN BY.

GM
황 금 손 인 테 리 어

@__gmdesign__
goldenhand99@naver.com

REMARK.
* 신설부분 *
각방에어컨 4대 + 거실 1대 (5마력)
각방에어컨 출력 약한걸로 해서 맞추기
거실에만 욕스위치 사용
주방,거실 터닝도어 모노와이트
안방 터닝도어 라이트베이지
전체 창호 라이트베이지

조명(팬던트, 벽등), 욕실거울장(여닫이)

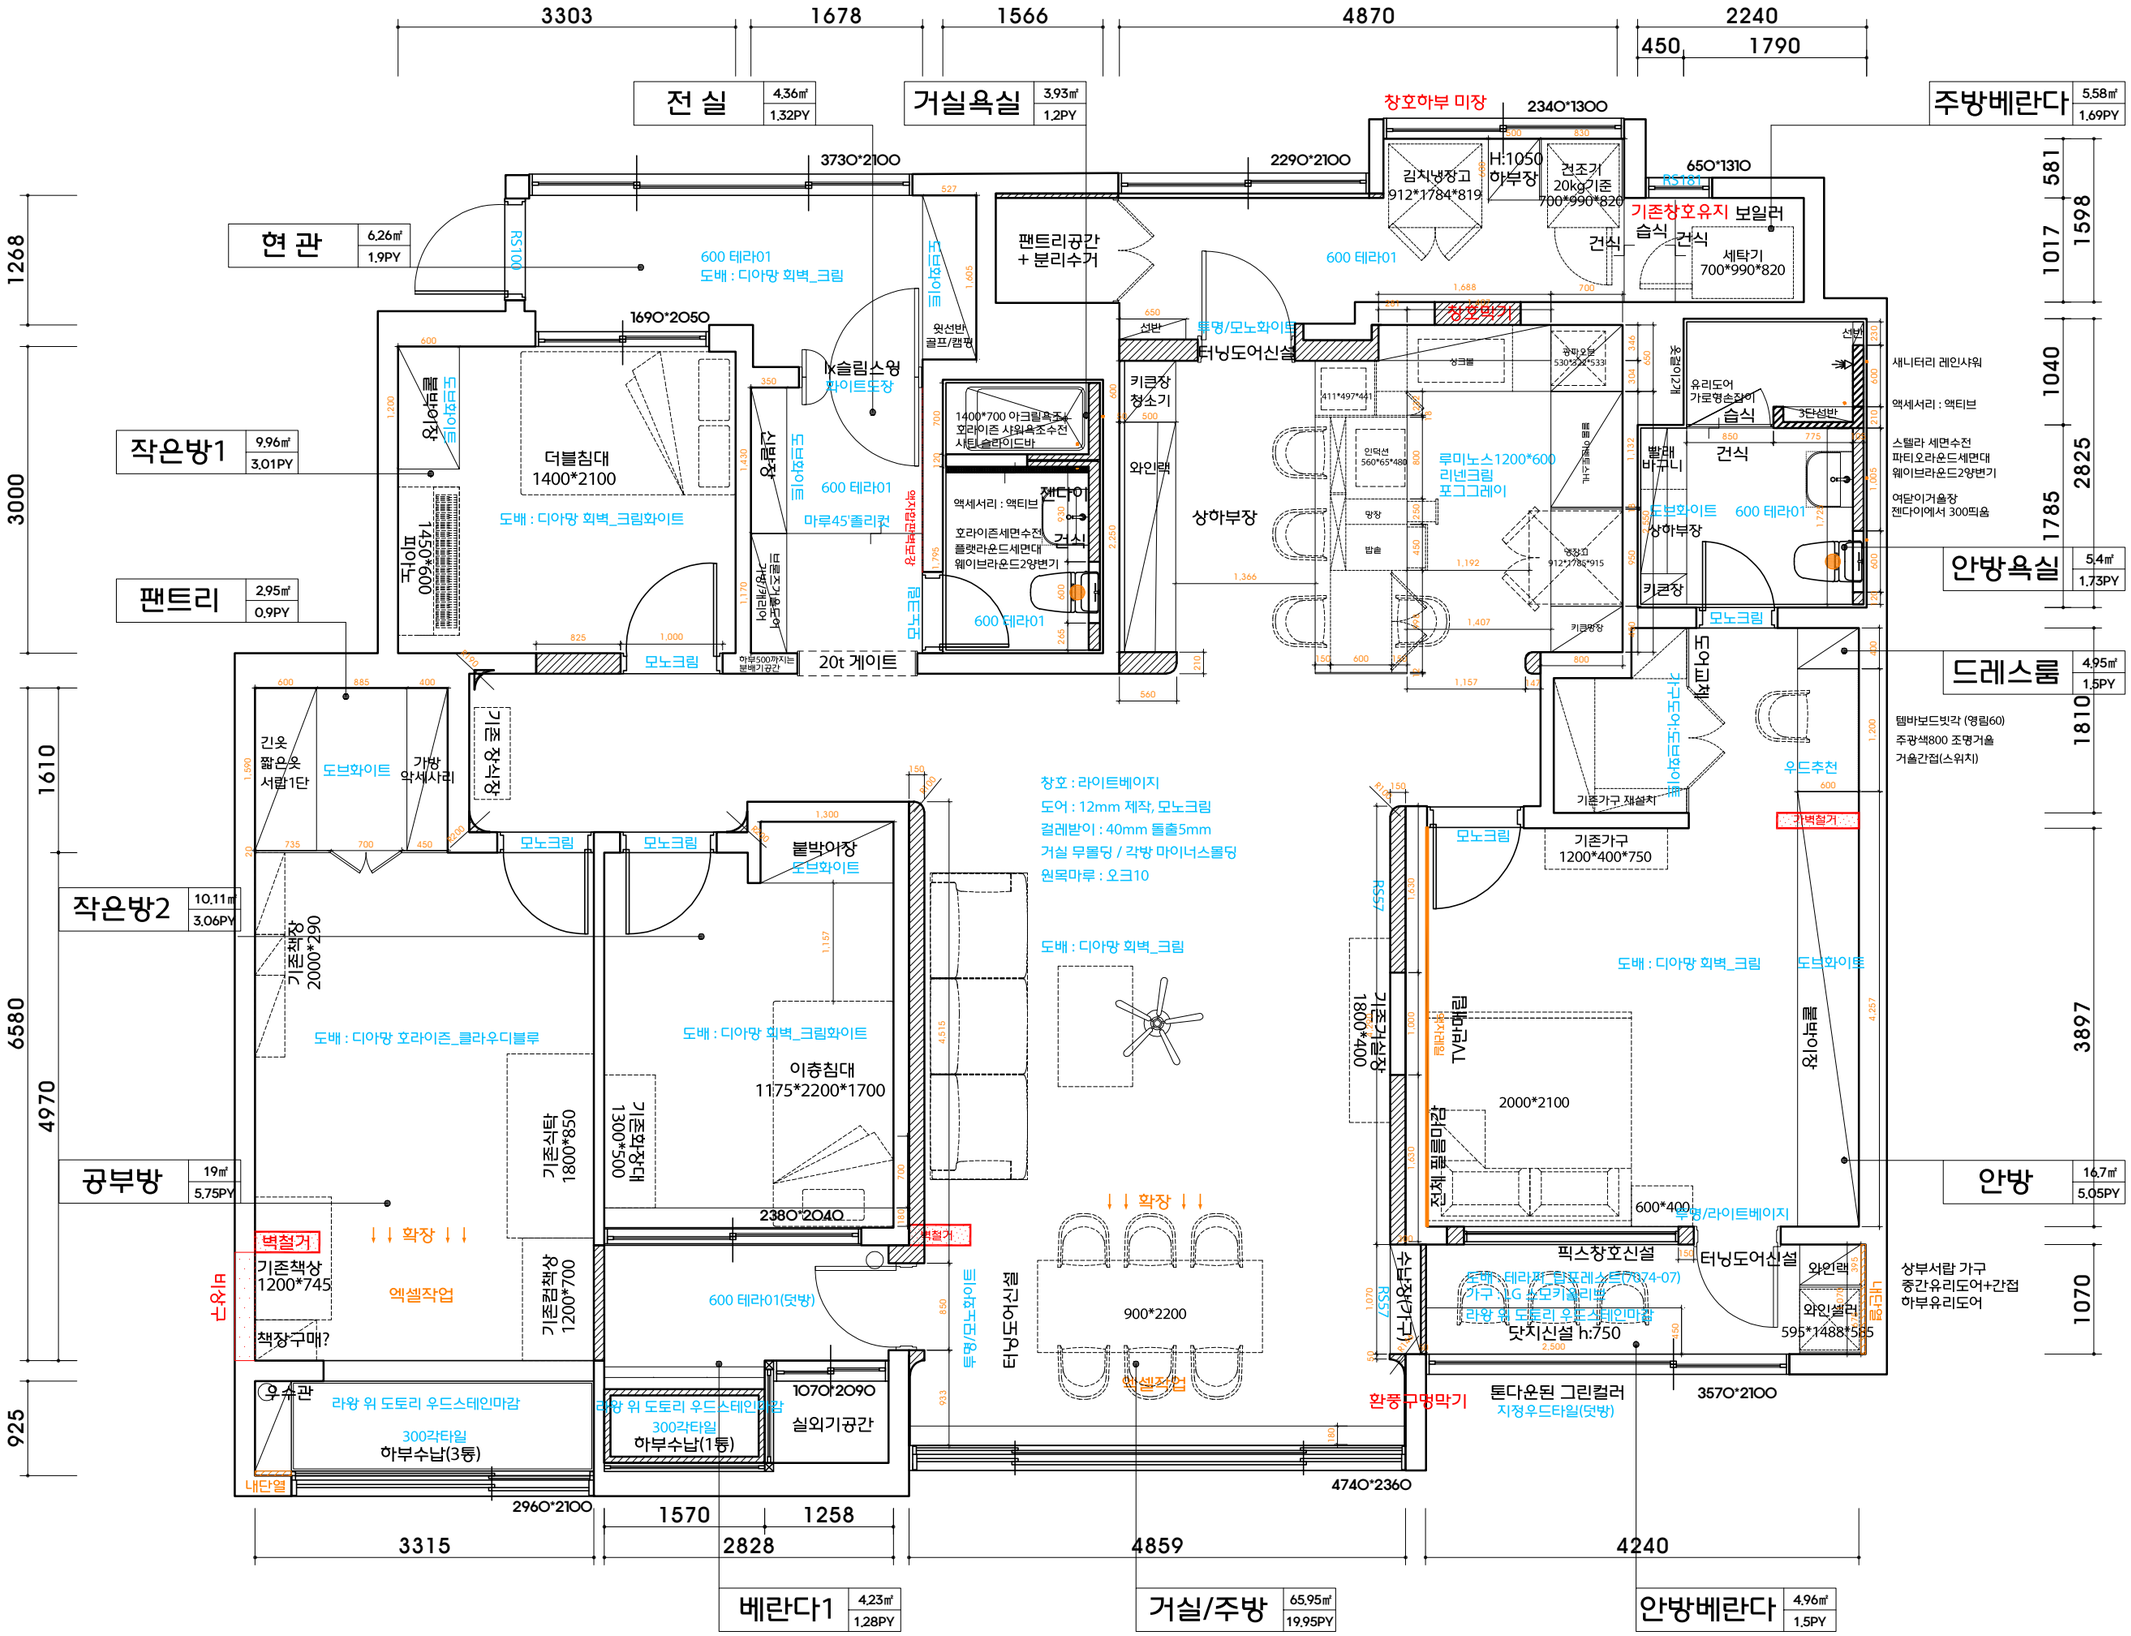

SITE CONDITIONS.

ADDRESS.
노형 대림 아파트
노형동 2585-2

AREA.
181.06 m2 / 54.77py

HEIGHT.
2280mm(최고2318mm)

PROJECT TYPE.
아파트 리모델링

PROJECT TITLE.
노형대림 103-1401

DRAWING TITLE.
평 면 도

SCALE.
A1:1/00 A3:1/60

DATE.
25.04.21

DRAWN BY.	CHECKED BY.
DRAWING No.	SHEET No.

- 본 도서는 어떠한 경우에도 무단으로 도용할 수 없으며 도용시 '지적재산권' 보호에 관한 법률에 의거, 법적 분쟁이 발생합니다. 또한 본 도서에 관한 모든 저작권은 당사에 있습니다. -