
DESIGN BY.

M2
디 자 인 엠 제 곱

@_m2design_
m2gmg@naver.com

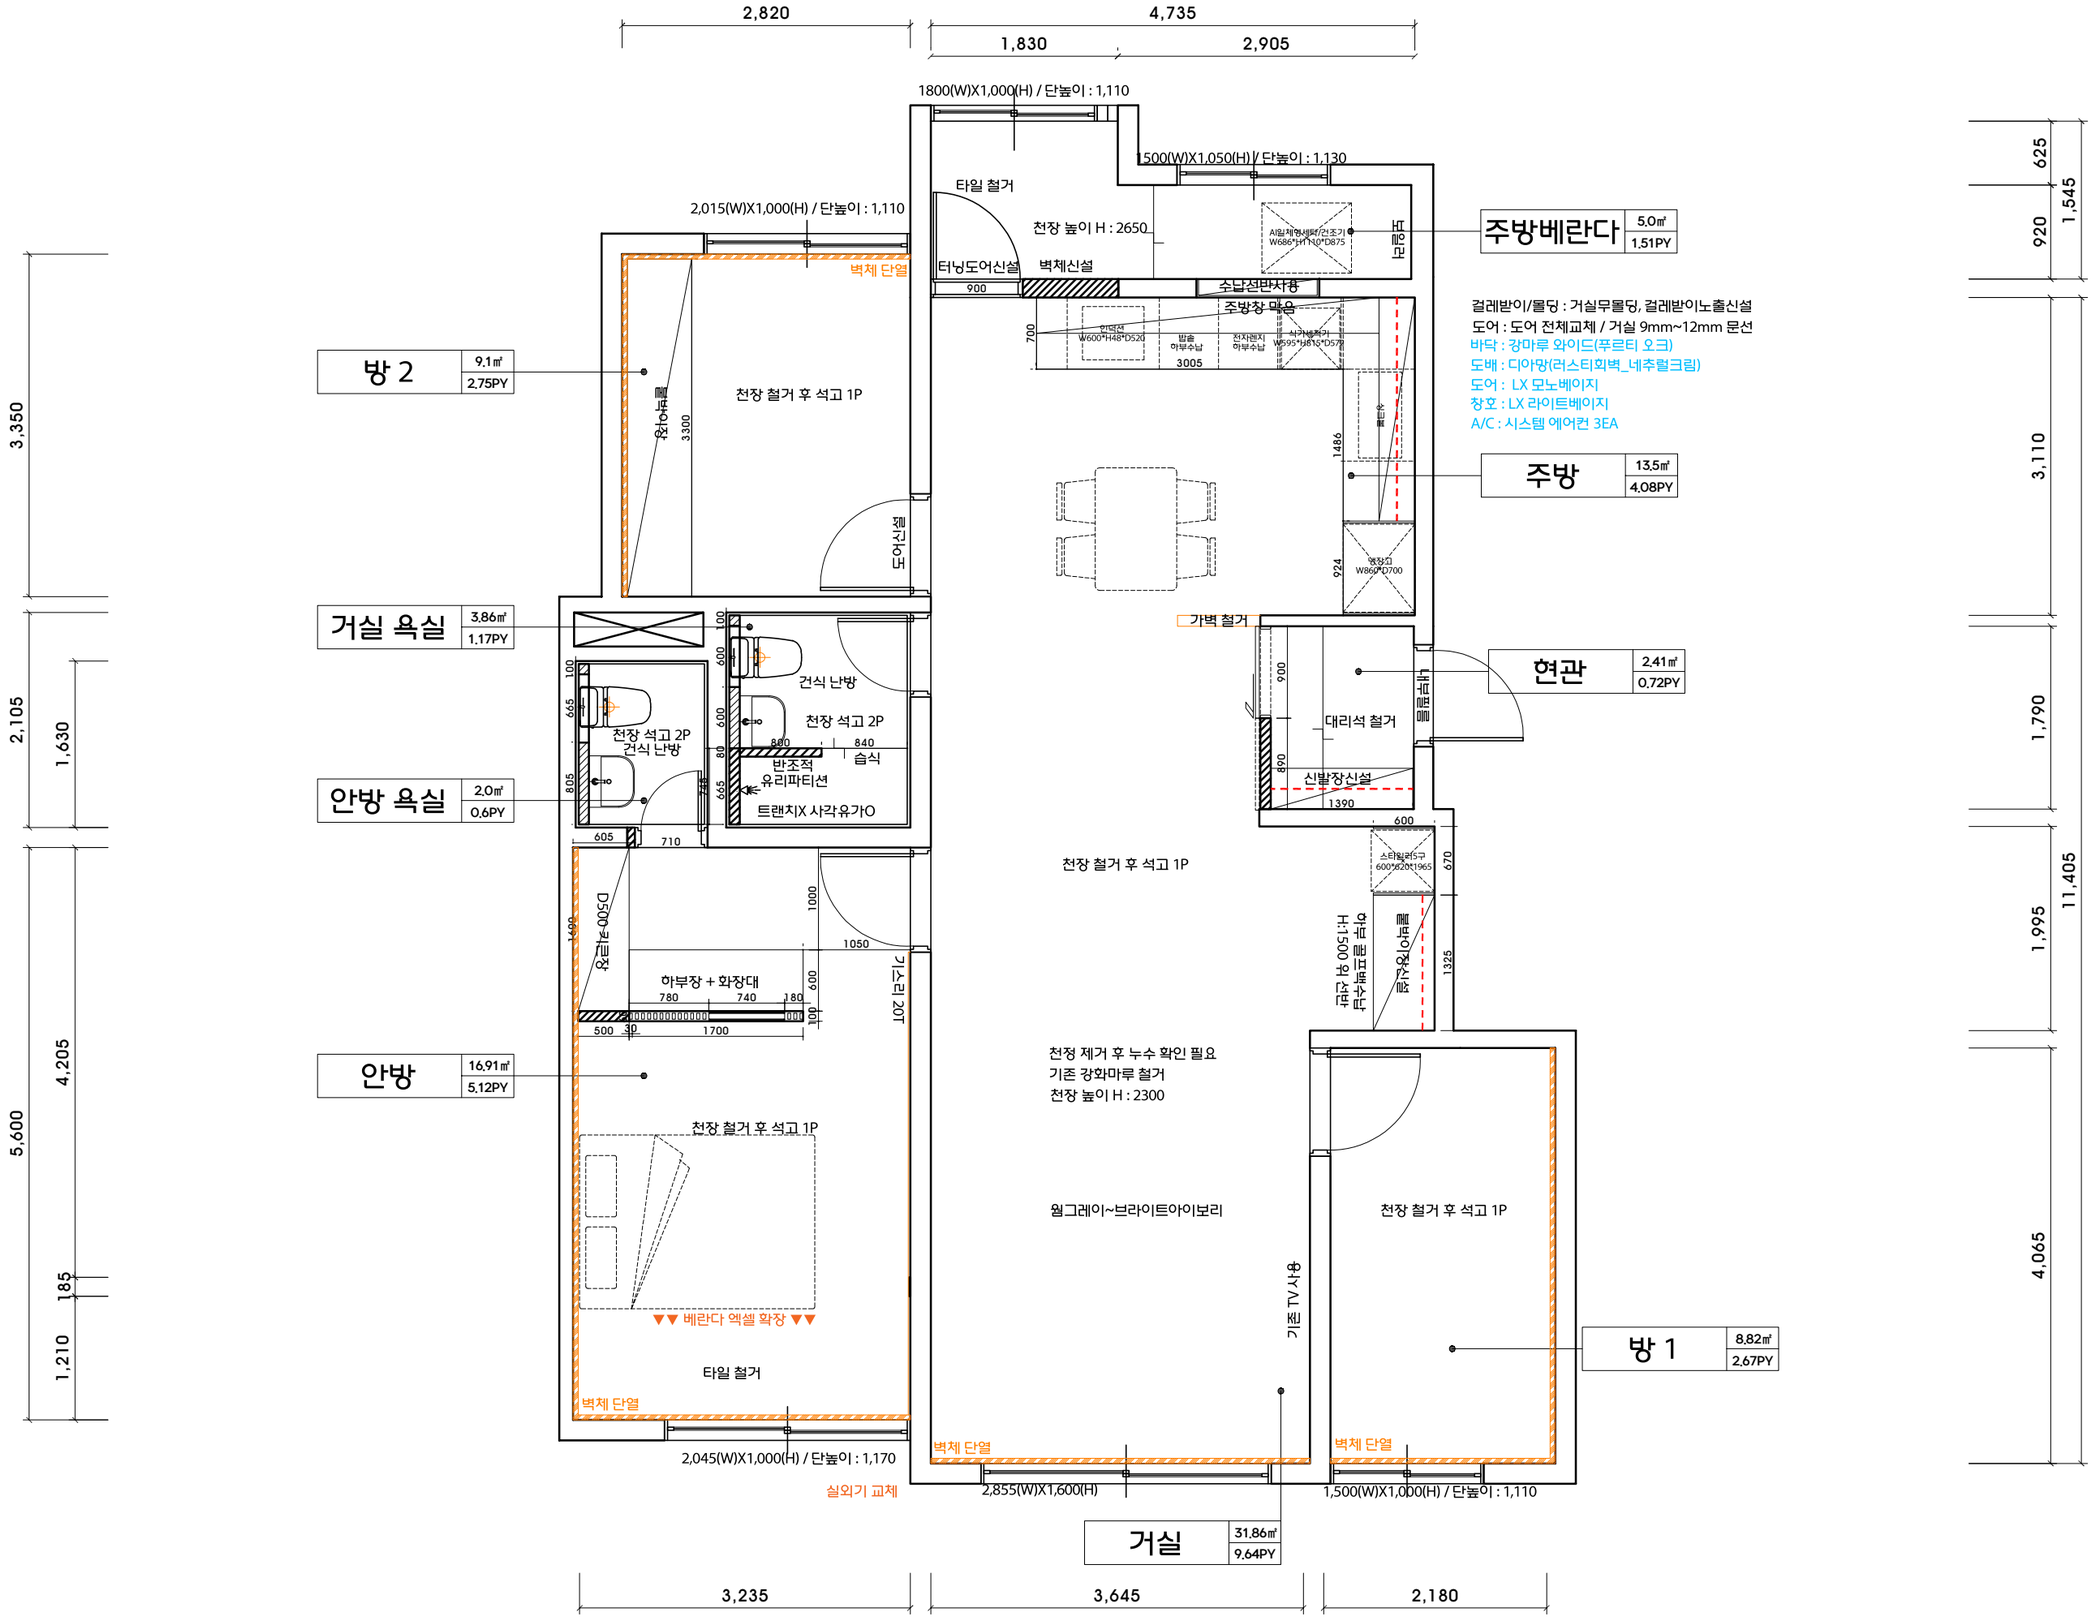


REMARK.

*철거
현관 대리석 바닥 및 싯기 철거,
샷시-주방 베란다 외창 2개, 주방 내창, 방2 외창
안방 외창, 거실 외창, 방1 외창, 주방 베란다내창
도어-도어(5EA), 중문 철거
천장 확인 후 전체 철거, 거실 우물천정철거
거실욕실 욕조, 도기, 욕실장 철거
안방욕실 도기, 욕실장 철거
타일-주방베란다/안방베란다 바닥, 화장실(2EA)
가구-신발장, 거실 수납장, 안방 수납장,
방 내부 키큰장/서랍장, 주방 싱크대/상부장

기타-거실아트월, 거실 문틀 주방벽체마감재,
걸레받이,몰딩,조명,스위치,콘센트
도배지, A/C, 주방벽체 마감,기타외

설비: 벽배수,배관이설
조적: 세면대/욕조 젠다이 반조적

SITE CONDITIONS.

ADDRESS.
제주시 연동 253-7
굿윌카운티 1205호

AREA.
93.46m2 / 28py

HEIGHT.
2300mm(2650mm)

PROJECT TYPE.
아파트 리모델링

PROJECT TITLE.
굿윌카운티 1205호

DRAWING TITLE.
평 면 도

SCALE.
A1:1/25 A3:1/60

DATE.
25.09.23

| DRAWN BY. | CHECKED BY. |
|---|---|
| | |

| DRAWING No. | SHEET No. |
|---|---|
| | |

- 본 도서는 어떠한 경우에도 무단으로 도용할 수 없으며 도용시 '지적재산권' 보호에 관한 법률에 의거, 법적 분쟁이 발생합니다. 또한 본 도서에 관한 모든 저작권은 당사에 있습니다. -