
DESIGN BY.

GM
황 금 손 인 테 리 어

@__gmdesign__
goldenhand99@naver.com

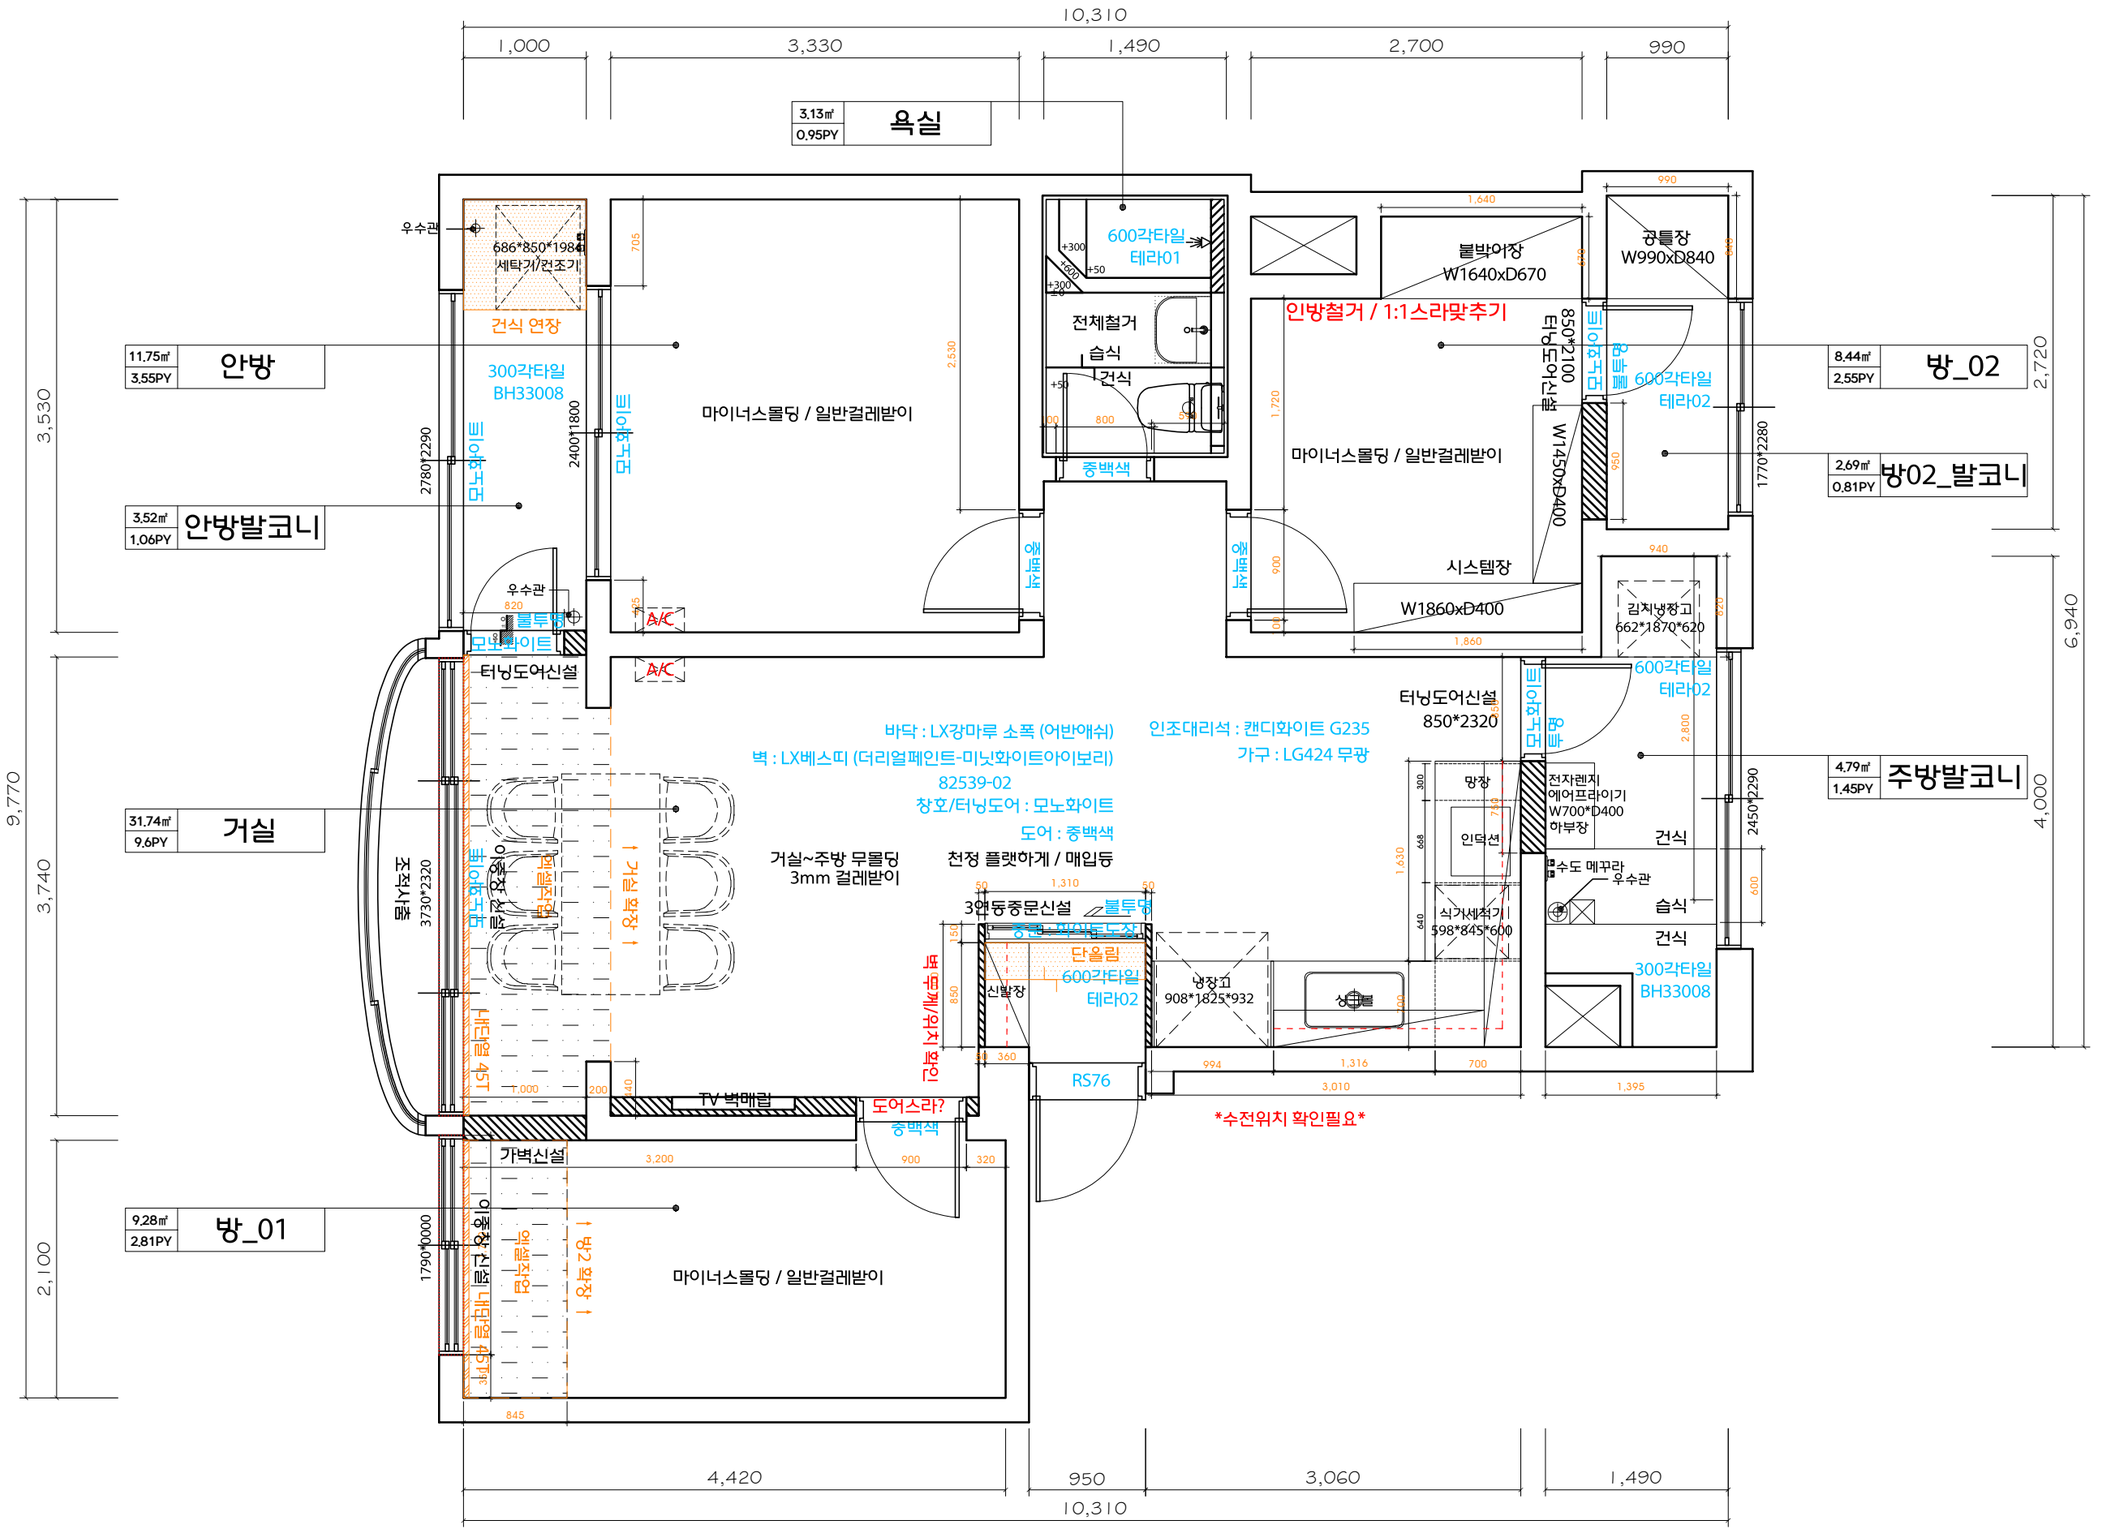

PROJECT.

* 철거부분
도어 : 도어 4개, 창호(내창) 3개
창호도어 2개
현관 : 신발장
거실 : 확장(내창, 바닥, 천정), 장판
주방 : 싱크대, 베란다 창호도어
주방베란다 : 가구일체
거실베란다 : 가구일체
안방 : 가구일체
방1 : 가구일체, 확장(내창,바닥,천정),내창
안방발코니 :
방2 : 가구일체, 확장(바닥,천정),내창
욕실 : 전체철거

비브랜드 제품이여도 니켈로
에어컨은 스탠드/벽걸이형

SITE CONDITIONS.

ADDRESS.
해오름아파트
104동 1401호

AREA.
81.71m2 / 24.72py

HEIGHT.
2300mm(거실)

PROJECT TYPE.
아파트 리모델링

PROJECT TITLE.
해오름104동 1401호

DRAWING TITLE.
평 면 도

SCALE.
A1:1/00 A3:1/50

DATE.
25.03.05

DRAWN BY.	CHECKED BY.
DRAWING No.	SHEET No.

– 본 도서는 어떠한 경우에도 무단으로 도용할 수 없으며 도용시 '지적재산권' 보호에 관한 법률에 의거, 법적 분쟁이 발생합니다. 또한 본 도서에 관한 모든 저작권은 당사에 있습니다. –