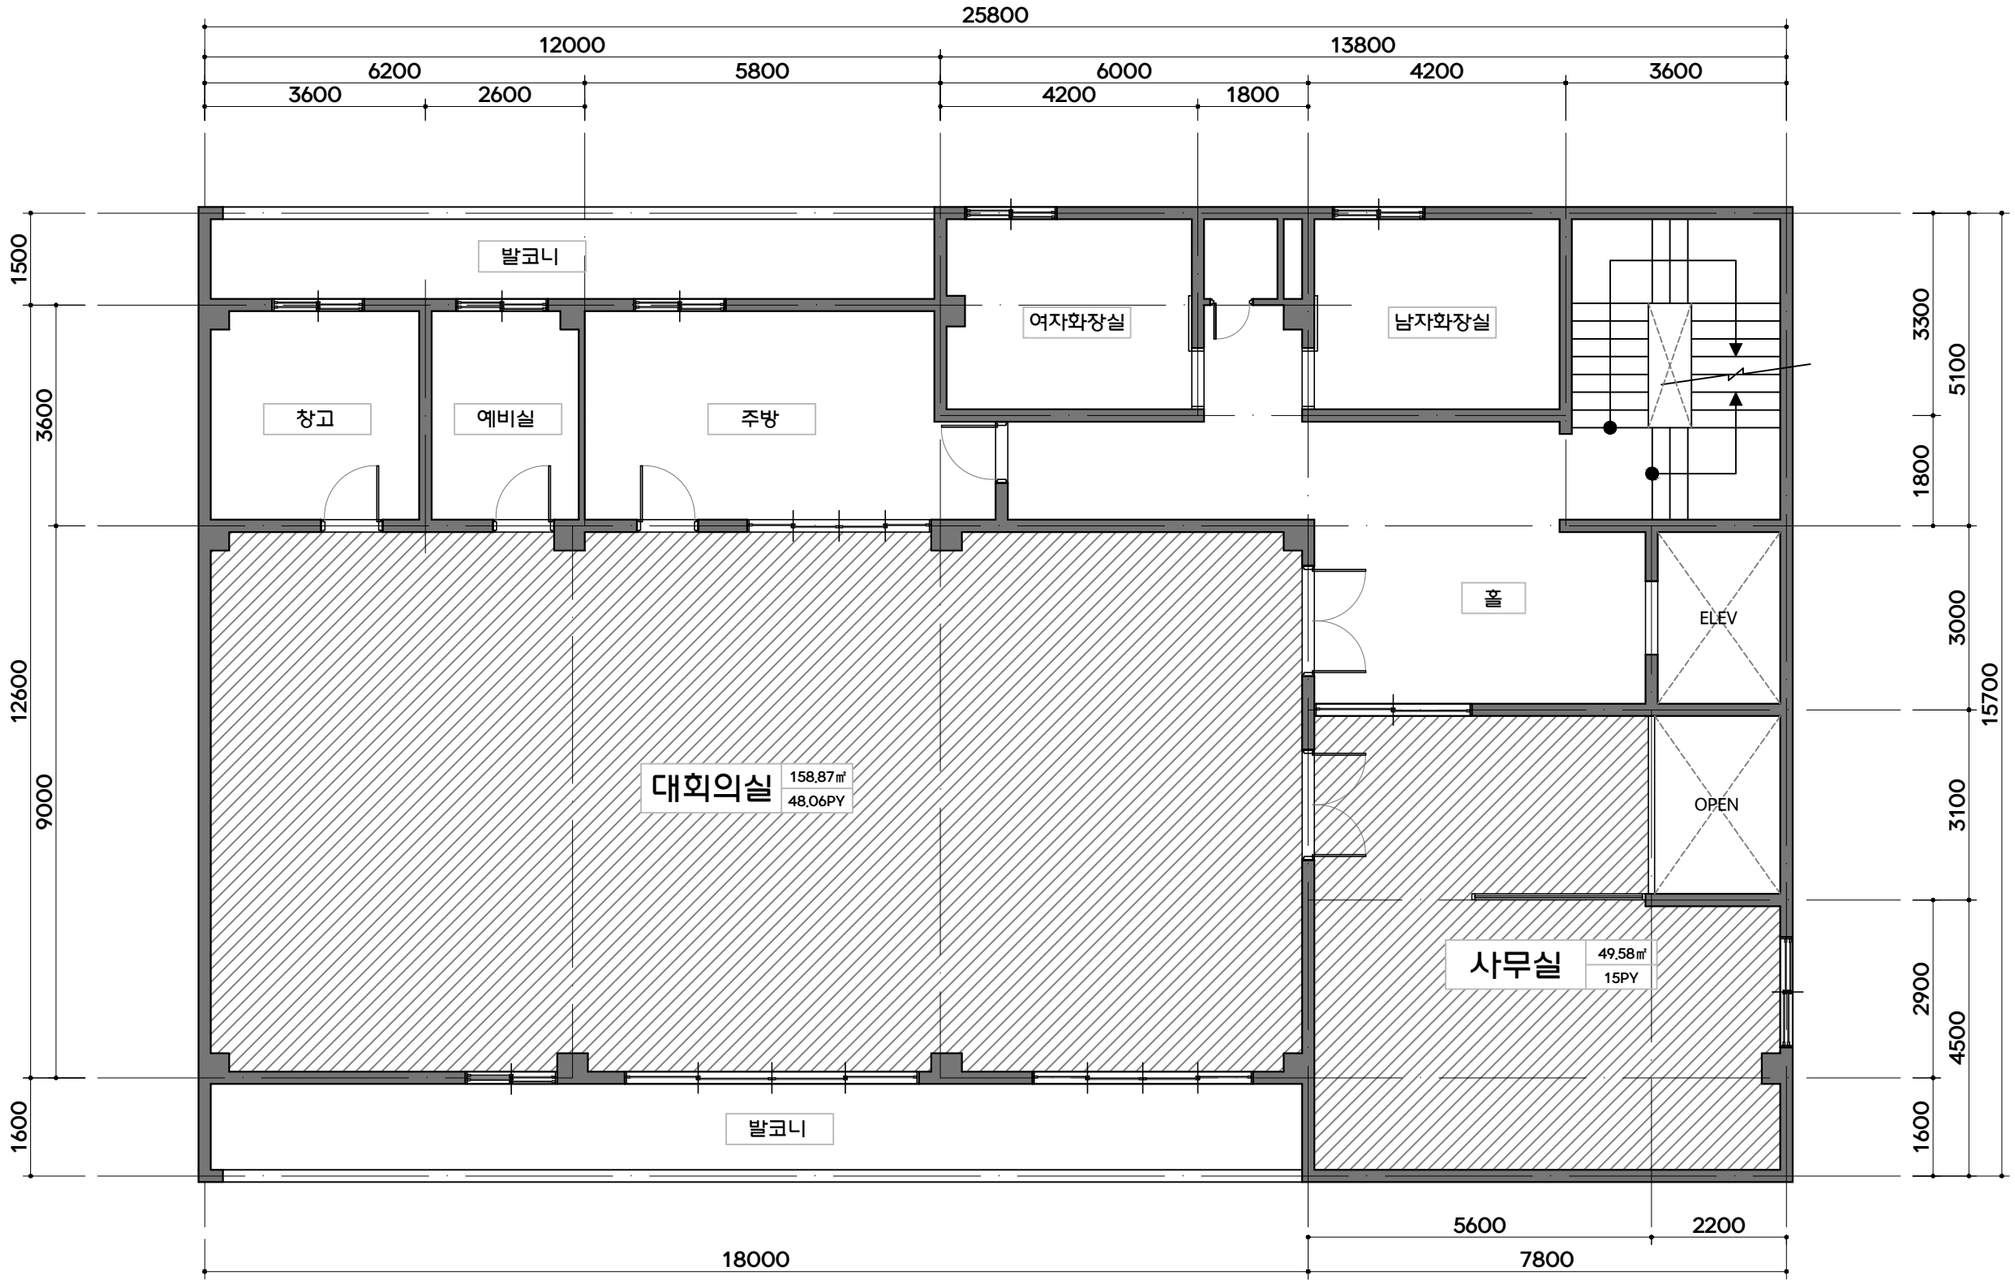


<타일물량 산출근거>

158.87㎡ + 49.58㎡ X 10% = 230㎡ (반올림)
(대회의실+사무실) X 로스율 10% = 타일 총 물량

1 FLOOR PLAN

SCALE 1 / 100

DESIGN M²

NOTE:

PROJECT: 성산읍 오조리 종합복지관 2층		SCALE: 1 / 100	DATE: 23. 12. 05
NAME OF DRAWING: FLOOR PLAN			
DRAWN BY:		SHEET NO: 001	DRAWN NO: I-01
CHECKED BY:	APPROVAL :		