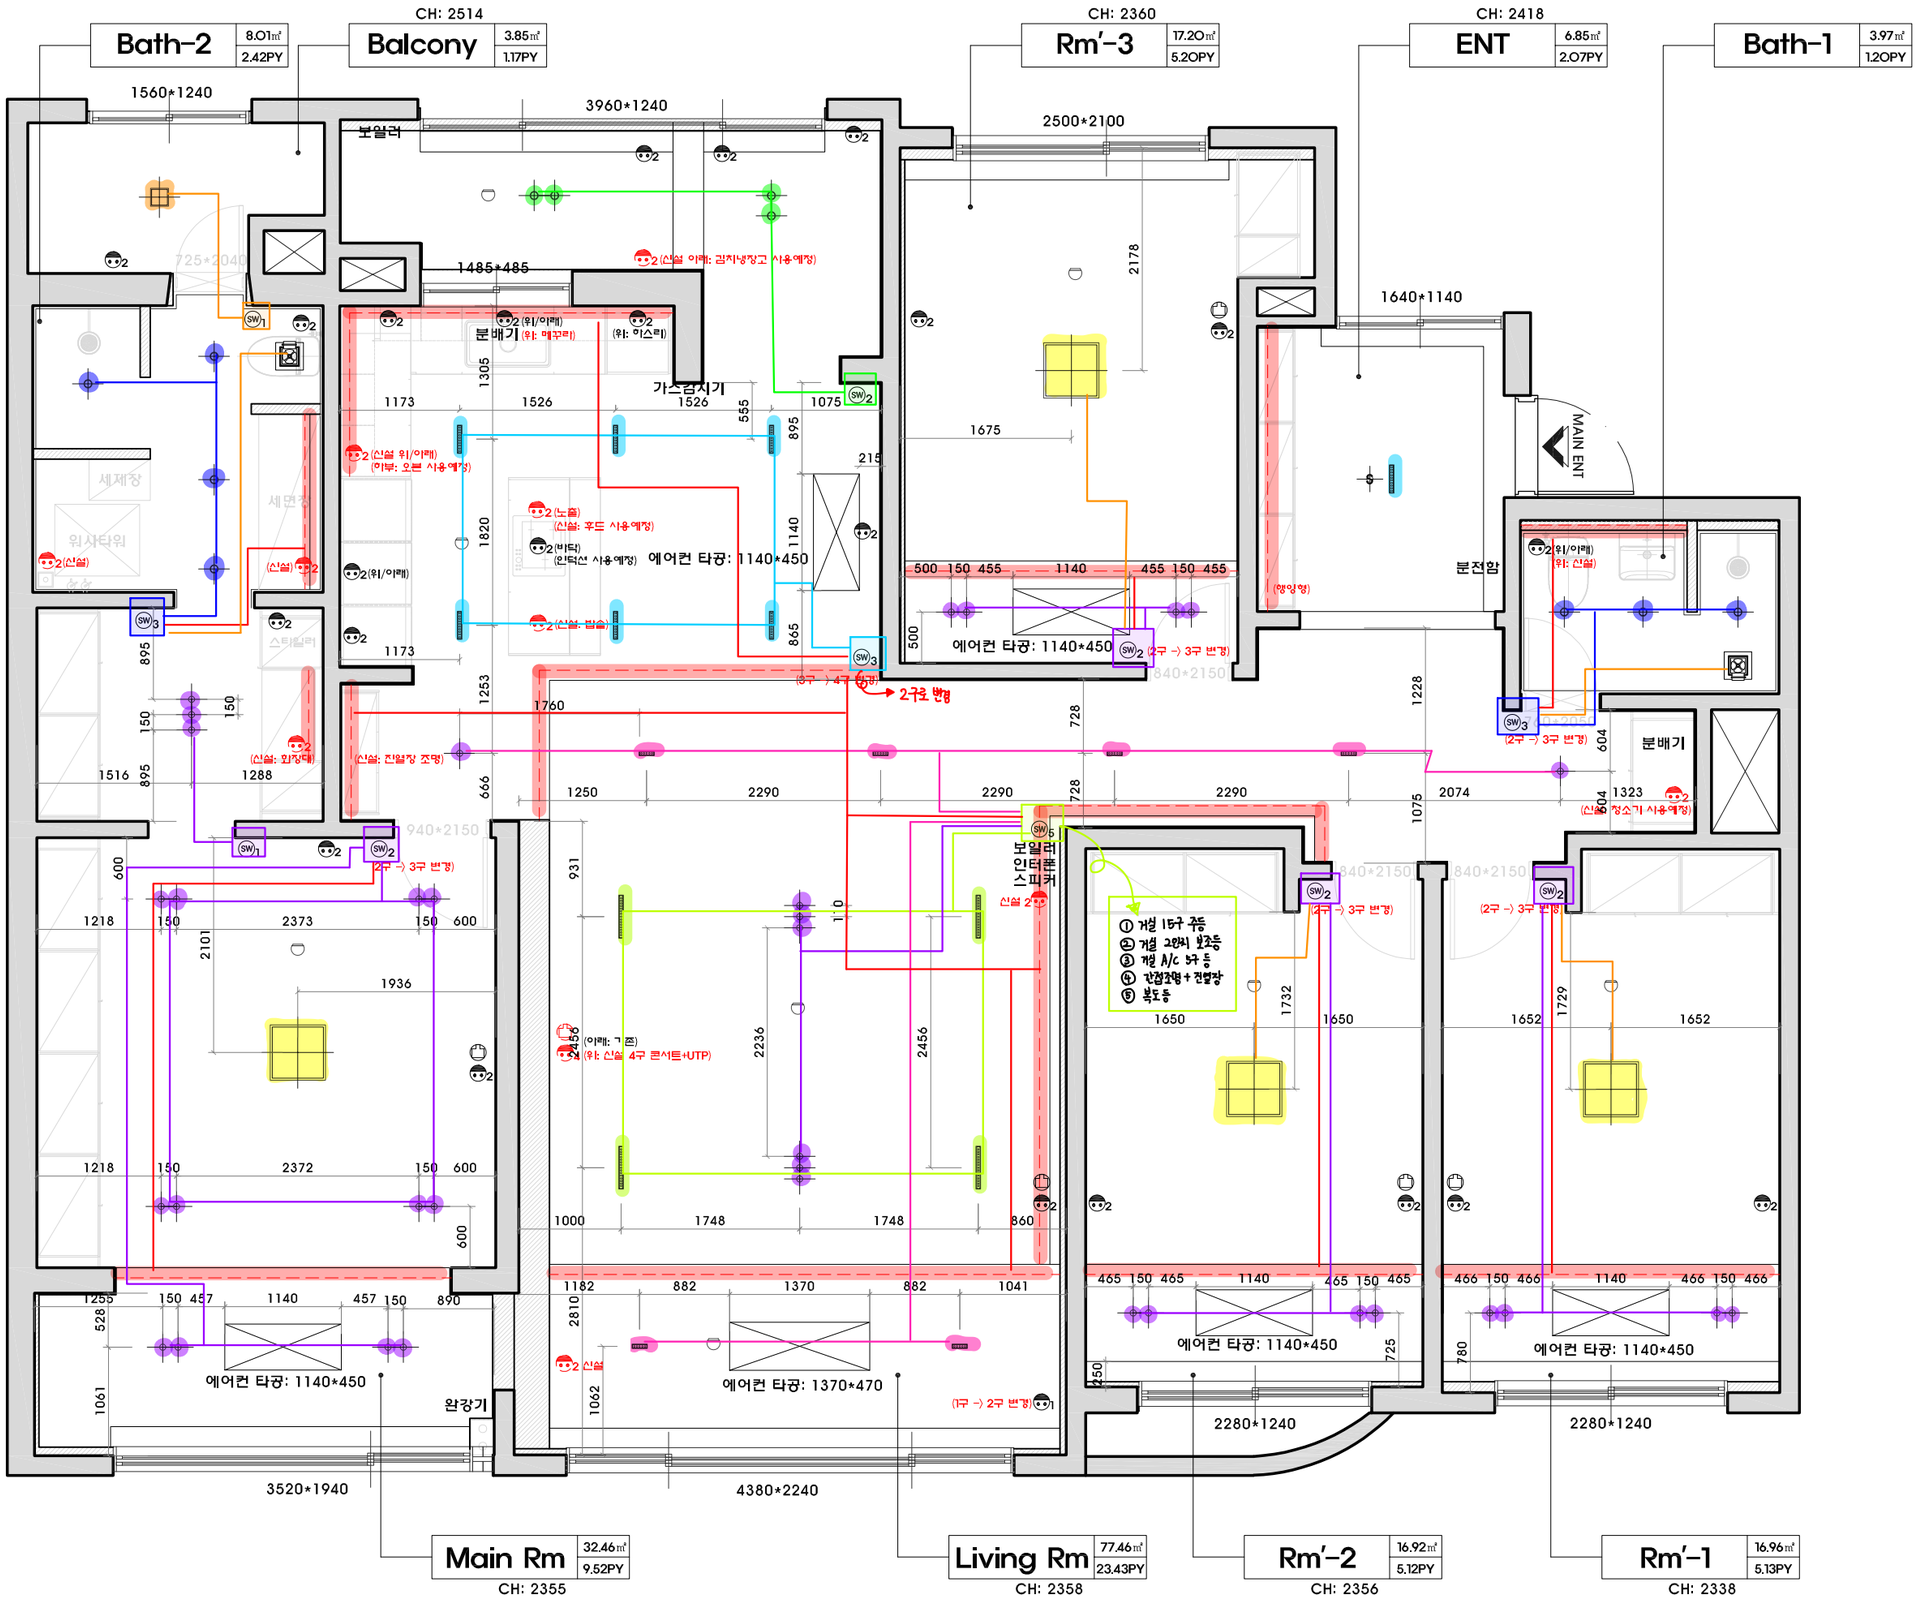


DESIGN BY.

DESIGN M²

@_m2design_
m2gmg@naver.com

PROJECT.

천정도

REMARK.

- S 이든센서 1개
- 2인치 매입등 35개
- 3인치 매입등 4개
- 3인치 매입 방습등 7개
- 6인치 사각 직부등 1개
- 작하 엣지등 4개
- T5 간접조명
- 사각 매입 다운라이트 15구 (타공: 410*33) 4개
- 사각 매입 다운라이트 10구 (타공: 265*33) 7개
- 사각 매입 다운라이트 5구 (타공: 140*33) 6개

SITE CONDITIONS.

ADDRESS.
제주도 제주시 광평동로 66
미리내중흥S클래스 107동 501호

AREA.
000.00 m2 / 000py

HEIGHT.
0000.00mm

PROJECT TYPE.
전체공사

PROJECT TITLE.
미리내중흥S클래스107-501

DRAWING TITLE.
Floor Plan

SCALE.
A1:1/30 A3:1/60

DATE.
23.12.06

DRAWN BY.	CHECKED BY.
CHACHA	KIM

DRAWING No.	SHEET No.
I-001	001

- 본 도서는 어떠한 경우에도 무단으로 도용할 수 없으며 도용시 '지적재산권' 보호에 관한 법률에 의거, 법적 분쟁이 발생합니다. 또한 본 도서에 관한 모든 저작권은 당사에 있습니다. -