
■ LEGEND

SYMBOL	DESCRIPTION
	센서(현관)
	2인치 다운라이트
	3인치 다운라이트
	4.5인치 다운라이트
	6인치 다운라이트
	벽등
	펜던트등
	LED 엣지등
	간접조명
	시스템에어컨
	실링팬
SW1	1구 스위치
SW2	2구 스위치
SW3	3구 스위치
SW5	5구 스위치
SW6	6구 스위치
1	1구 콘센트
2	2구 콘센트
4	4구 콘센트
2 (방우)	2구 콘센트(방우)
보일러	보일러 조절기
	인터넷
	환풍기
	차동식 스포트 감지기

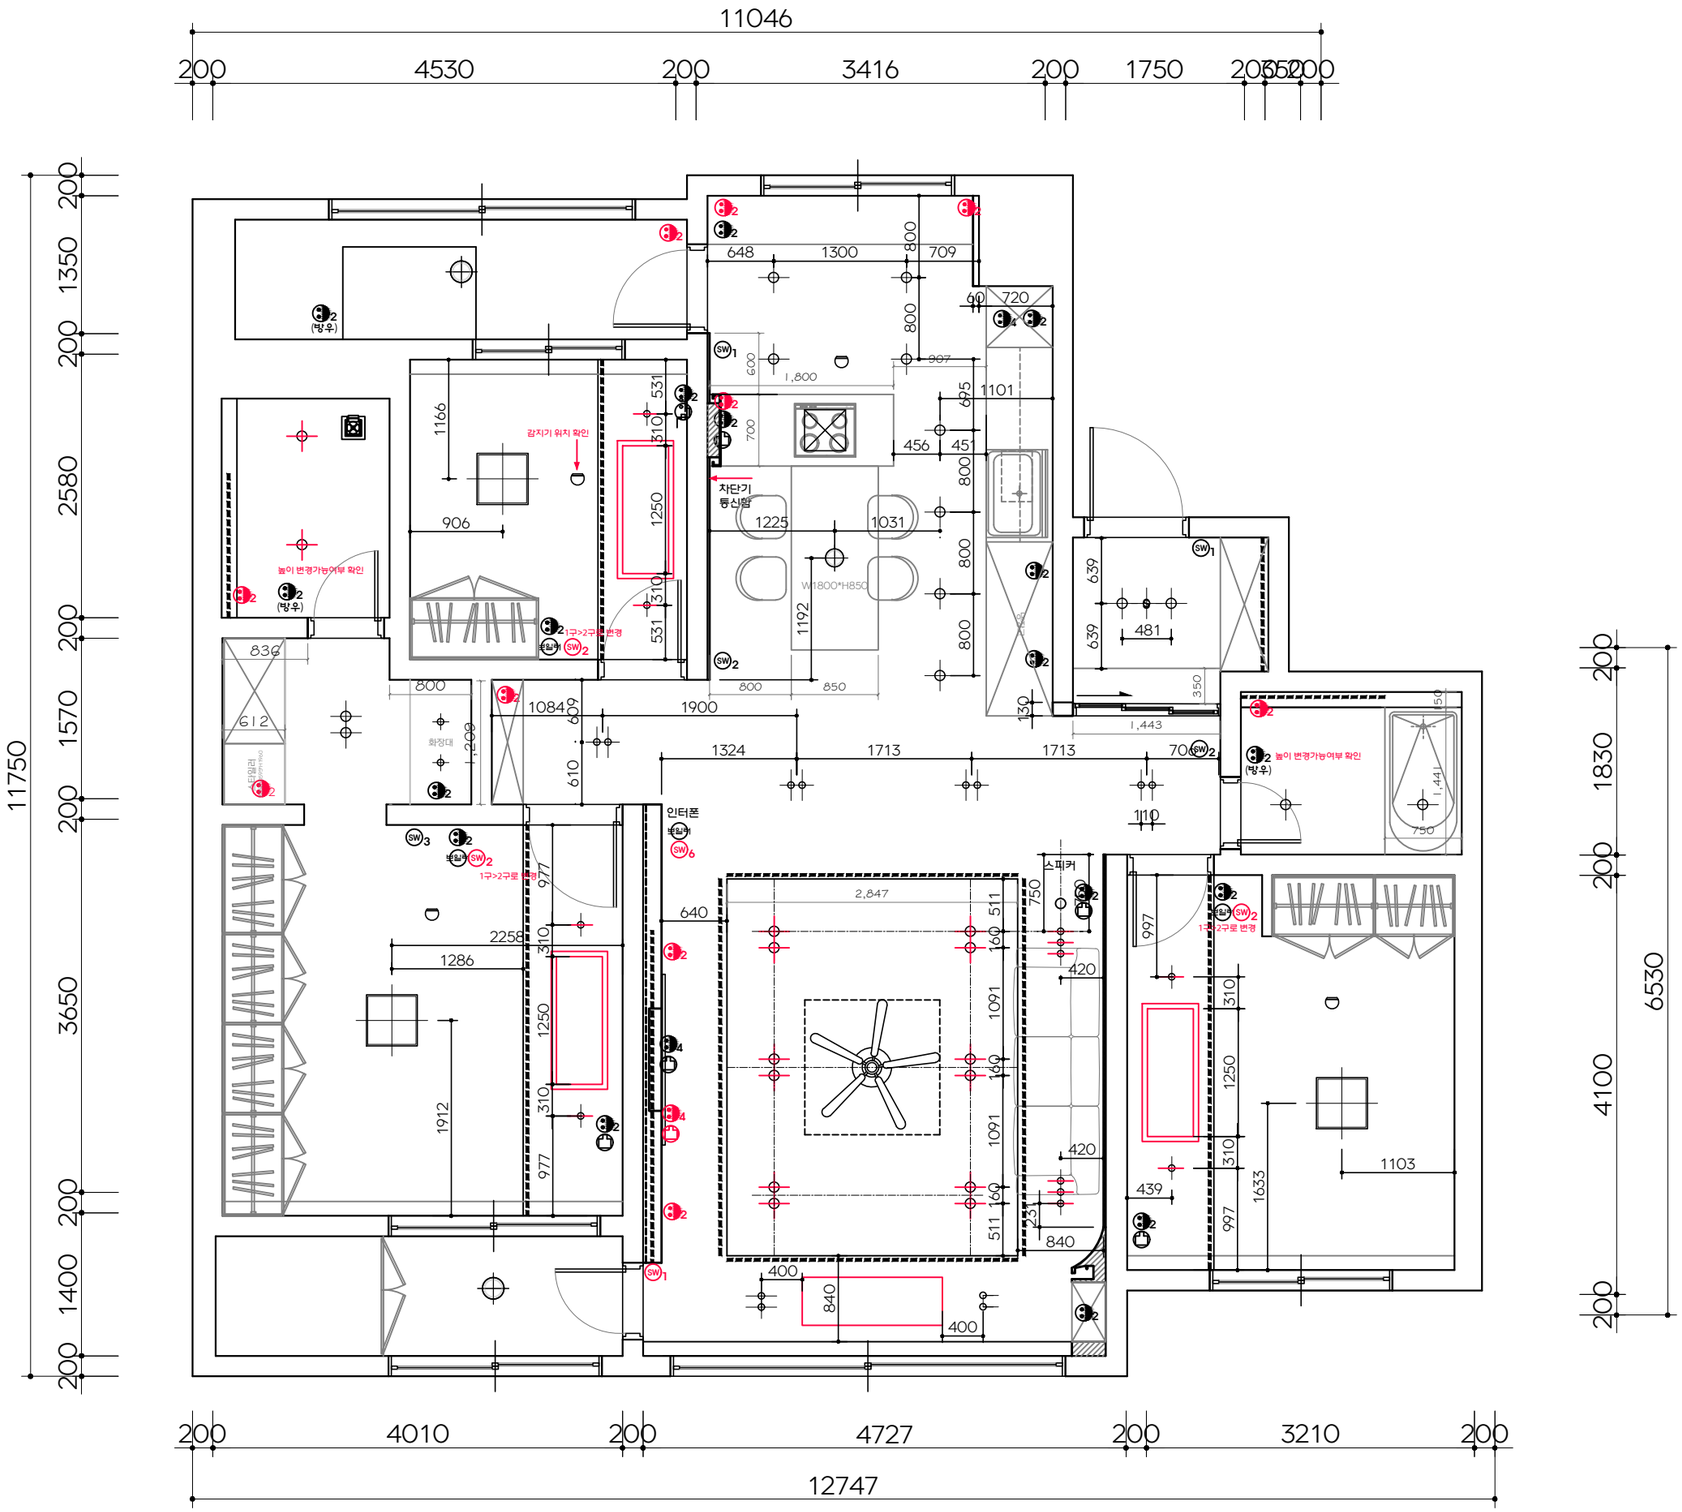

1 FLOOR PLAN

SCALE 1 / 60

DESIGN M²

NOTE: 층 면적 113.99㎡ / 34.54PY

PROJECT: 삼화 부영아파트 201동 802호	SCALE: 1 / 60	DATE: 23. 11. 08
NAME OF DRAWING: FLOOR PLAN		
DRAWN BY:	SHEET NO: 001	DRAWN NO: I-01
CHECKED BY: APPROVAL :		