
\\admin-pc01\공유폴더\■ 황금손01_현장\260119_노형 현대 아이파크 103동 402호 인테리어공사\02_도면\260227_현대아이파크 103동 802호 도면.dwg,2026-0

총 면적 : 107.28㎡ / 32.5PY

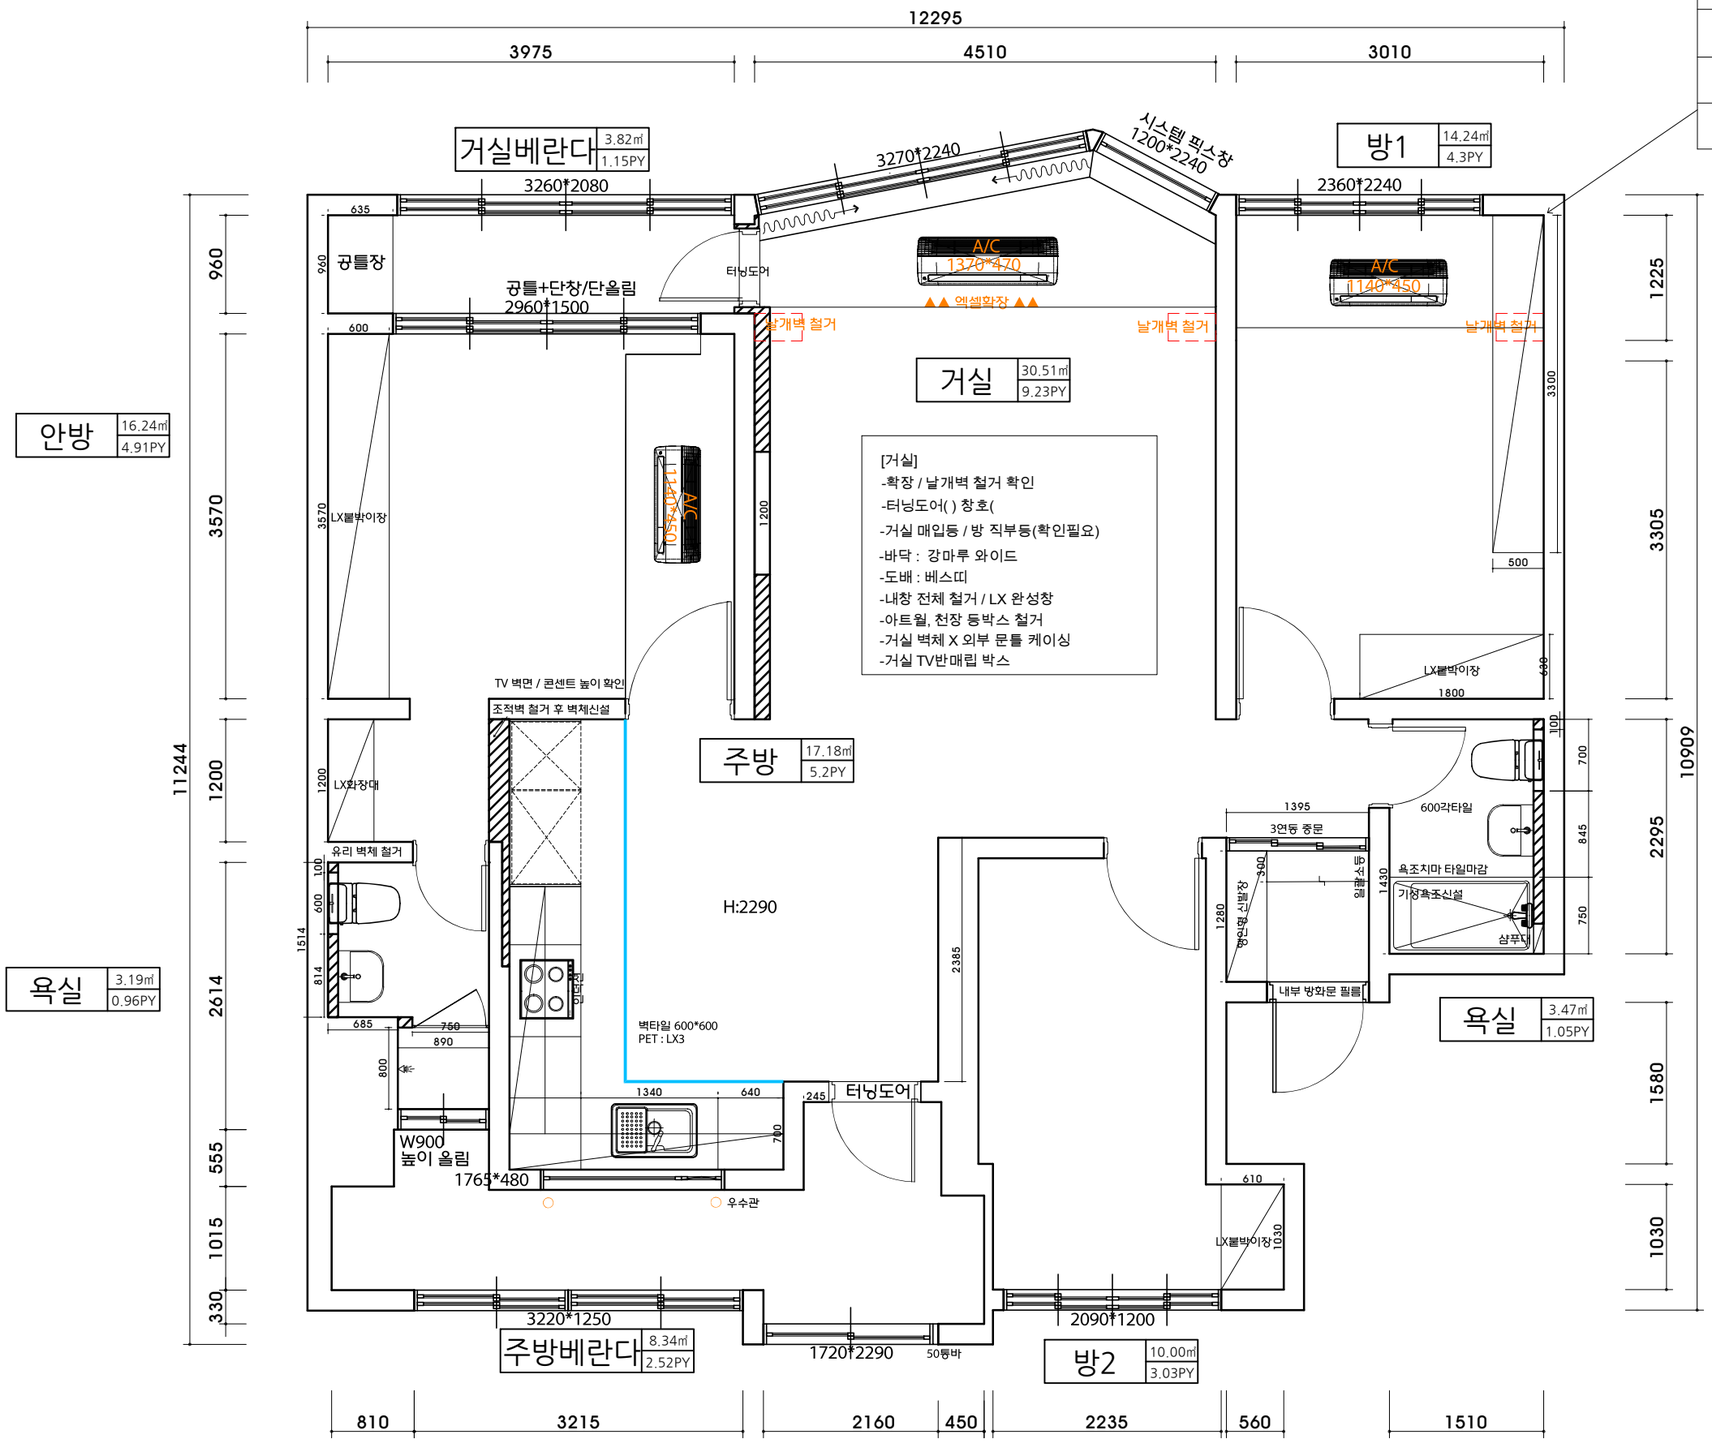

[거실]
-확장 / 날개벽 철거 확인
-터닝도어( ) 창호(
-거실 매입등 / 방 직부등(확인필요)
-바닥 : 강마루 와이드
-도배 : 베스띠
-내창 전체 철거 / LX 완성창
-아트월, 천장 등박스 철거
-거실 벽체 X 외부 문틀 케이싱
-거실 TV반매립 박스

[안방]
-창호 높이 조절

[주방]
-창호 교체
-후드 : 빌트인 매립후드
-벽체 철거 후 4도어 냉장고(냉장고+김치냉장고)
-터닝도어 신설

[거실욕실] 600각
-조적 샴푸대/욕조/해바라기X
-욕조 샤워수전, 돔천장

[안방욕실] 600각
-창 높이 줄임
-샤워 부스 신설
-돔천장,트렌치유가,해바라기 X

[방1]
-시스템에어컨
-붙박이장/수납+책장 신설
-날개벽 철거

[방2]
-붙박이장 신설

[에어컨]
-시스템 에어컨 3개 : 방2개+거실

[디자인]
-도어 :
-마루 : LX와이드마루
-도배 : 전체 베스띠
-거실 몰딩/걸레받이

[주방,안방 베란다]
-300각 타일 / 벽면 탄성

DESIGN BY.

M2
디 자 인 엠 제 곱

@_m2design_
m2gmg@naver.com

PROJECT.

SITE CONDITIONS.

ADDRESS.
제주시 원노형로 90
노형아이파크 103-402

AREA.
m2 / py

HEIGHT.
0000mm

PROJECT TYPE.
천 정 도

PROJECT TITLE.
노형아이파크 103-402

DRAWING TITLE.

SCALE.
A1:1/30 A3:1/60

DATE.
26.02.27

DRAWN BY.	CHECKED BY.
DRAWING No.	SHEET No.

- 본 도서는 어떠한 경우에도 무단으로 도용할 수 없으며 도용시 '지적재산권' 보호에 관한 법률에 의거, 법적 분쟁이 발생합니다. 또한 본 도서에 관한 모든 저작권은 당사에 있습니다. -