
DESIGN BY.

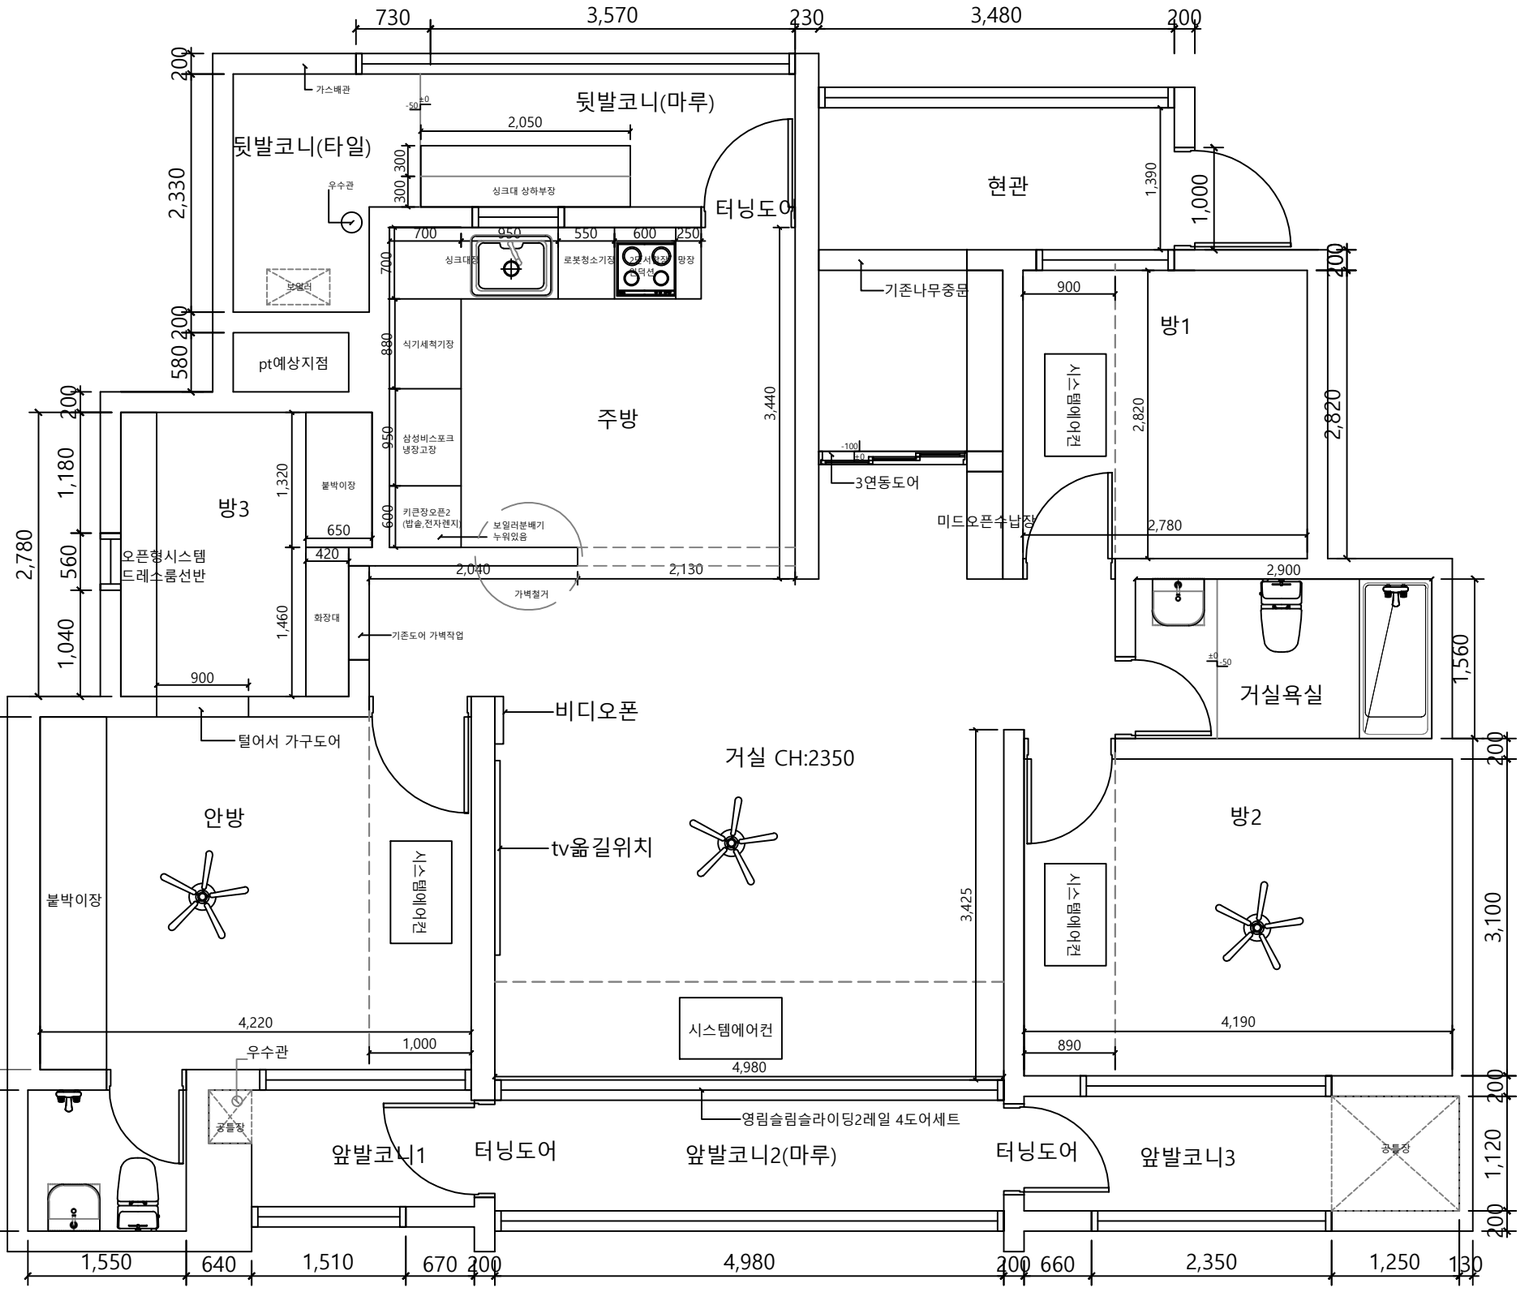

공통

보일러싱글제어기 멀티제어기로변경
누운보일러세워야함
전체도배마감
탄성페인트(뒷발코니,앞발코니1,2,3, 현관일부)
에어컨단내림4개(방1,2,안방,거실)
실링팬3개(방2,안방,거실)
조명,스위치 전체교체 2인치or3인치
바닥타일600각(뒷발코니,현관,앞발코니1,3)
강마루
전체 몰딩 걸레받이교체
전체외창필름
전체내창 창호교체(거실은 4980sl미닫이)
앞발코니1,3 공틀장(앞발코니3단열필요)
방문5개 문틀까지 재시공(기존목문)

현관

외창하부 기존필름벽 필름마감(탄성마감으로변경)
천장돌출된 우물에 목작업해서 간접조명(평천장으로변경
기존나무중문쪽벽은 탄성마감
나무중문철거하고 문선작업
3연동중문
신발장옆가벽
현관문필름
현관장시공

욕실(안방,거실)

거실욕실(변경있음)
조적파티션1개,변기,장세면기,욕조,일반장1개,
휴젠뜨,상부장600*800(거울1,일반2)

안방욕실(변경있음)
외부닿는 ㄱ자 단열(30t)
변기,세면기,샤워수전,대리석선반,거울장,휴젠뜨
해바라기수전

거실,안방욕실 둘다 세면기 벽배수로 바꿔야함
타일600각 시공
거실,안방욕실 콘센트 기존위치에서 이동필요

거실

천장평탄화
tv반매립박스
tv위치 오른쪽벽에서 왼쪽으로 옮기기
거실만 르그랑아테오스위치

주방

싱크대,타일교체
천장철거후재시공
인덕션기존거 재사용

안방

붙박이장화장대시공
기존가벽털고 가구도어시공

영림슬림슬라이딩2레일 4도어세트(예가발주예정 제품250만원)

DESIGN M²

@__gmdesign__
goldenhand99@naver.com

견적사항

*철거
- 올철거(욕실2개, 공용욕실 대형)
문와꾸 9틀, 신발장, 주방가구, 안방붙박이장,
북쪽방 책장 2벽면세트,
- 공용부 알판철거
- 공용부 바닥 장판, 각방 데코타일
- 내창철거/교체
- 현관, 발코니바닥타일 덧방
- 주방거실 사이 비내력벽 철거
-

*설비
- 공용욕실 매립수전
- 온수분배기 교체
- 각방 온도조절기
- 욕실 2개소 방수
- 건식단
- 조적파티션 샴푸대

*창호
- 내창만 창호교체
- 터닝도어 2개

*전기
- 인덕션 단독선
- 휴젠트 2대 단독
- 에어컨 단독선
- 실링팬 4대
- 에어컨박스 or 커튼박스 간접배선
- 주방 상부장, 욕실 은경장 하부 간접배선, 신발장 하부

*목공
- 거실 창호벽 및 측면 양쪽벽 단열작업
- 안방욕실 외벽부 ㄱ자 벽 단열작업
- 시스템에어컨 4대
- 발코니 공틀장 단열
- 각방 문틀부 벽면만 가베작업, 나머지공용부는
기스리 안침
- 거실 비확장부 슬라이딩 도어: 제조사 미정
(길이 넓어서 4짝 양개형 슬라이딩 도어 가능여부 확인)
- 현관 : 3연동 중문
- 안방 맞은편방 기존 문와꾸 막음작업
- 거실 반매립 티비벽
- LX 슬림문틀 5세트

*타일
- 현관, 발코니 바닥타일 덧방
- 욕실 2개소 타일

*욕실
- 매립수전(공용욕실만)
- 공용욕실 욕조
- 돔천정(간접)
- 공용욕실 은경장 길게 벽면 꽉채워서
- 휴젠트 2대

*필름
- 외창 필름리폼
- 방화문 내부 1면 리폼

*도장
- 천실, 발코니4개 도장

*도배
- 전체 베스띠 도배

*마루
- 강그린 와이드

*가구
- 주방가구, 주방발코니 가구, 신발장(행잉), 안방 붙박이
안방 맞은편방 시스템가구, 공용욕실 세면대 하부장,

*에어컨
- 시스템에어컨 4대, 외부 장비(실외기 앵글)

*기타공사
- 각방 온도조절기
- 인터폰 도어락(연동비 필수 넣을것)
- 폐기물

DRAWN BY.	CHECKED BY.
DRAWING No.	SHEET No.

- 본 도서는 어떠한 경우에도 무단으로 도용할 수 없으며 도용시 '지적재산권' 보호에 관한 법률에 의거, 법적 분쟁이 발생합니다. 또한 본 도서에 관한 모든 저작권은 당사에 있습니다. -