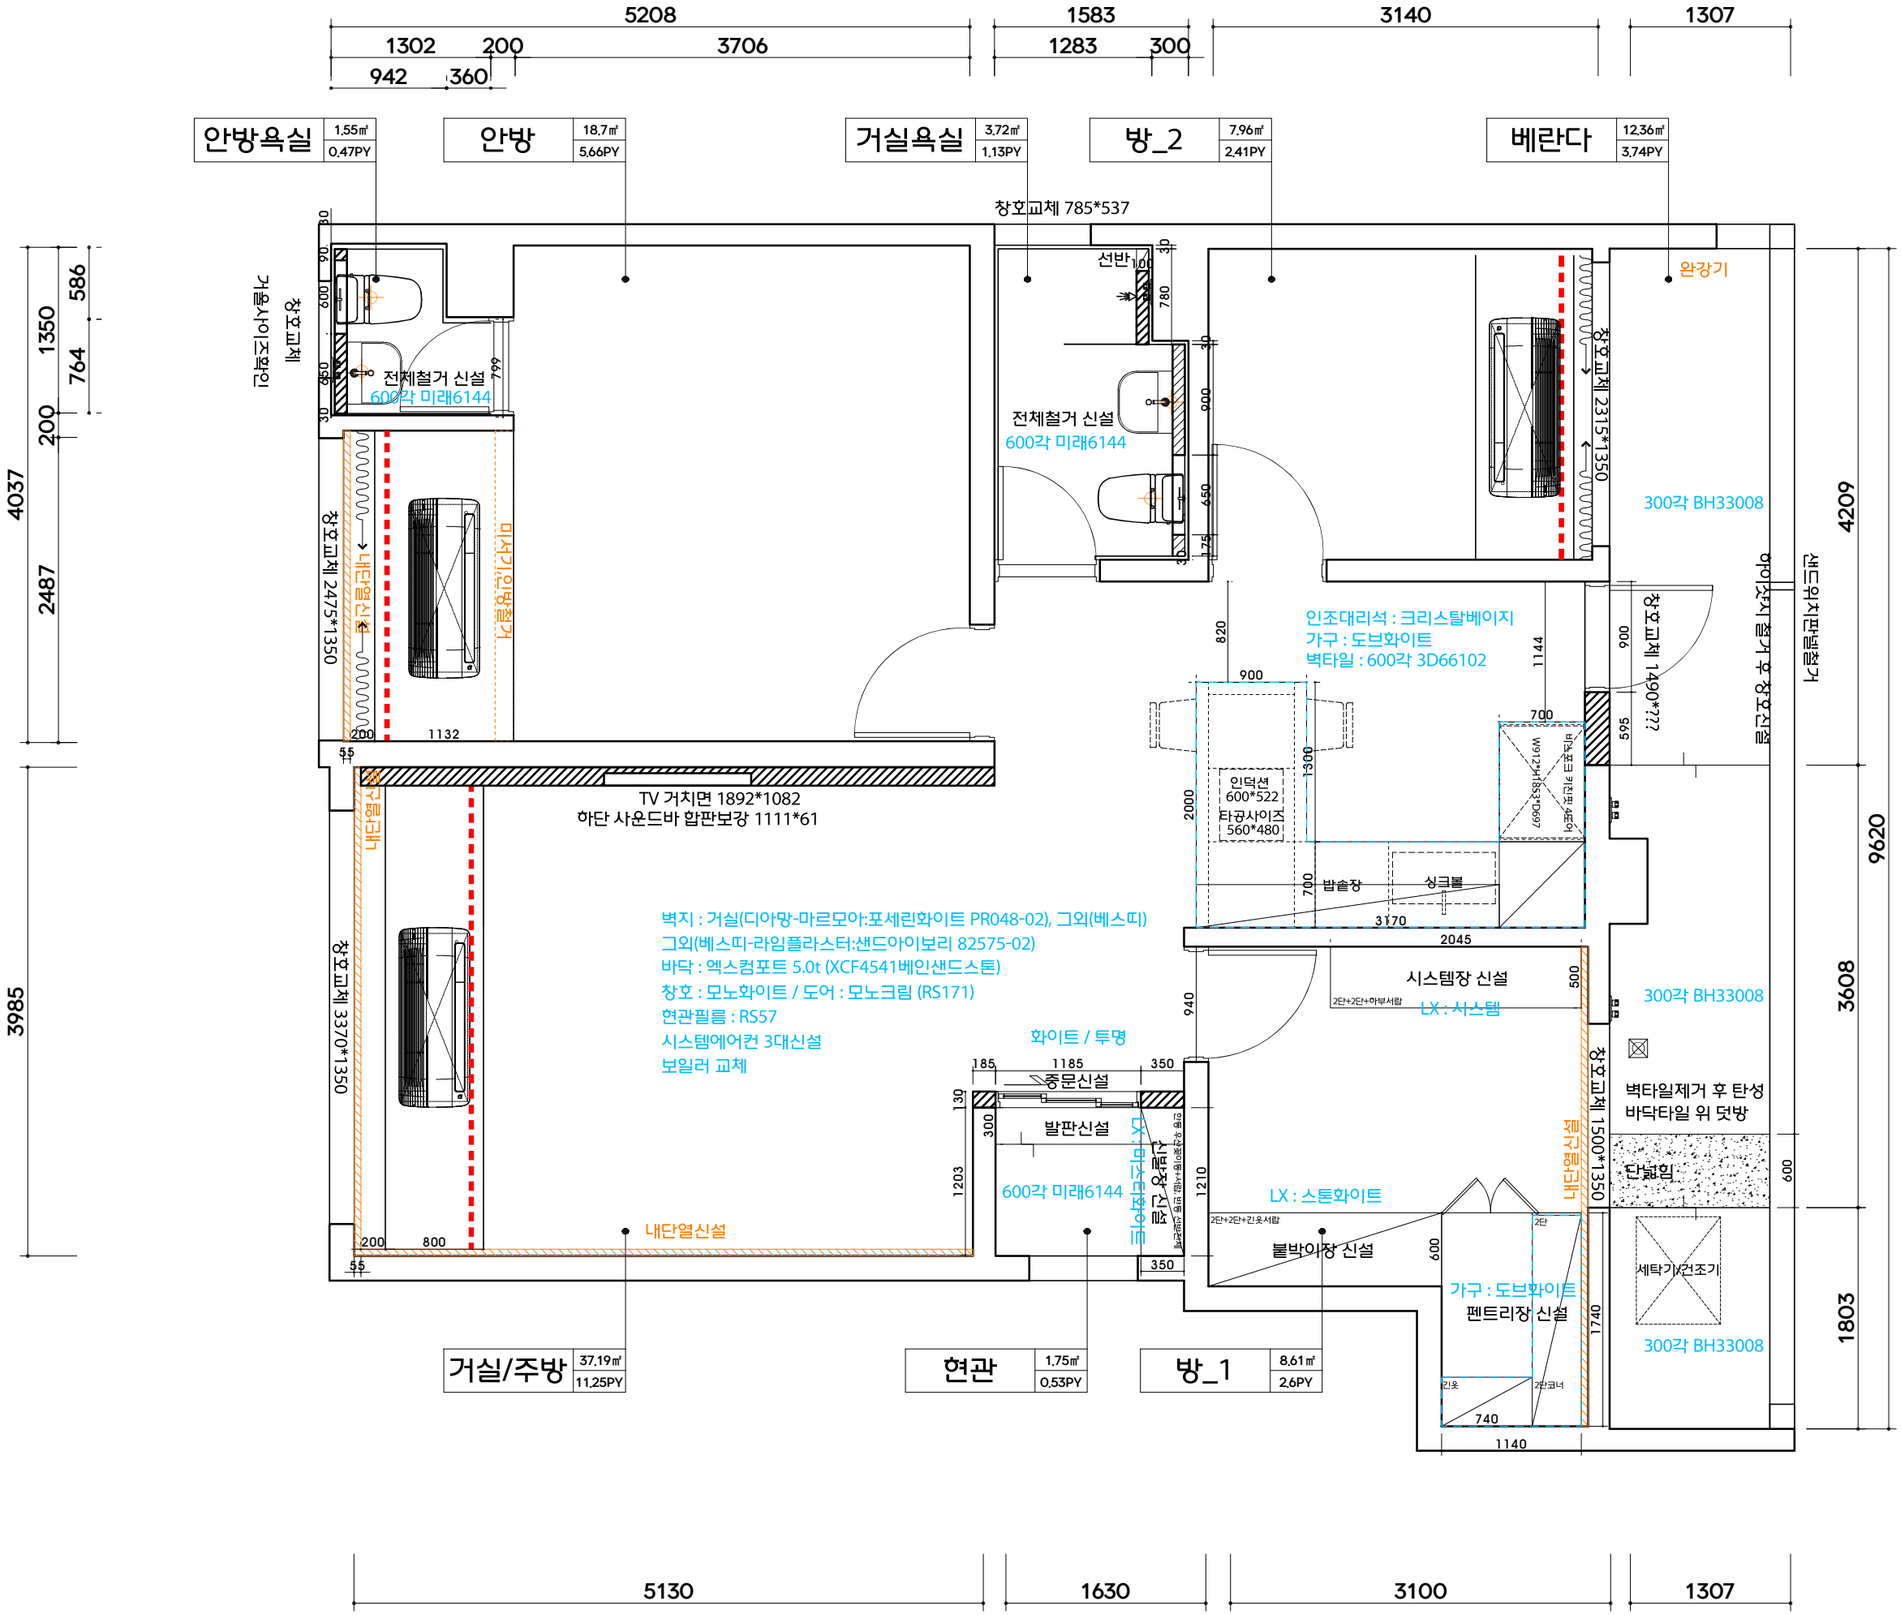


DESIGN BY.

GM
황 금 손 인 테 리 어

@_m2design_
m2gmg@naver.com

REMARK.
*철거
샷시-안방욕실창 제외 모두 철거

도어-방도어셋트3개,욕실도어셋트1개
거실 욕실 전체철거

타일-주방베란다 벽/바닥, 현관 벽/바닥

가구-신발장, 주방싱크대, 방1붙박이장
안방붙박이장,

기타-거실/안방 에어컨박스,
안방 미서기인방 철거
주방베란다(샌드위치판넬,하이샷시철거
걸레받이,몰딩,조명,스위치,콘센트
도배지, A/C, 주방벽체 마감,기타외

방:장판, 거실/주방:강마루철거

설비: 거실욕실벽배수,배관이설, 수전이동
조적: 세면대 젠다이 반조적, 샴푸조적

SITE CONDITIONS.

ADDRESS.
제주시 선덕로6길 32
수목아파트 가동 502호

AREA.
99.79m2 / 30.19py

HEIGHT.
2276mm(거실)

PROJECT TYPE.
아파트 리모델링

PROJECT TITLE.
수목아파트 가동 502호

DRAWING TITLE.
평 면 도

SCALE.
A1:1/25 A3:1/50

DATE.
25.08.04

DRAWN BY.	CHECKED BY.
DRAWING No.	SHEET No.

– 본 도서는 어떠한 경우에도 무단으로 도용할 수 없으며 도용시 '지적재산권' 보호에 관한 법률에 의거, 법적 분쟁이 발생합니다. 또한 본 도서에 관한 모든 저작권은 당사에 있습니다. –

\\admin-pc01\공유폴더\■ 황금손\01_현장\★250624_연동 수목아파트 가동 502호 인테리어공사\02_도면\250804_수목가동502호.dwg,2025-08-27 09:25:34,Microsoft PDF