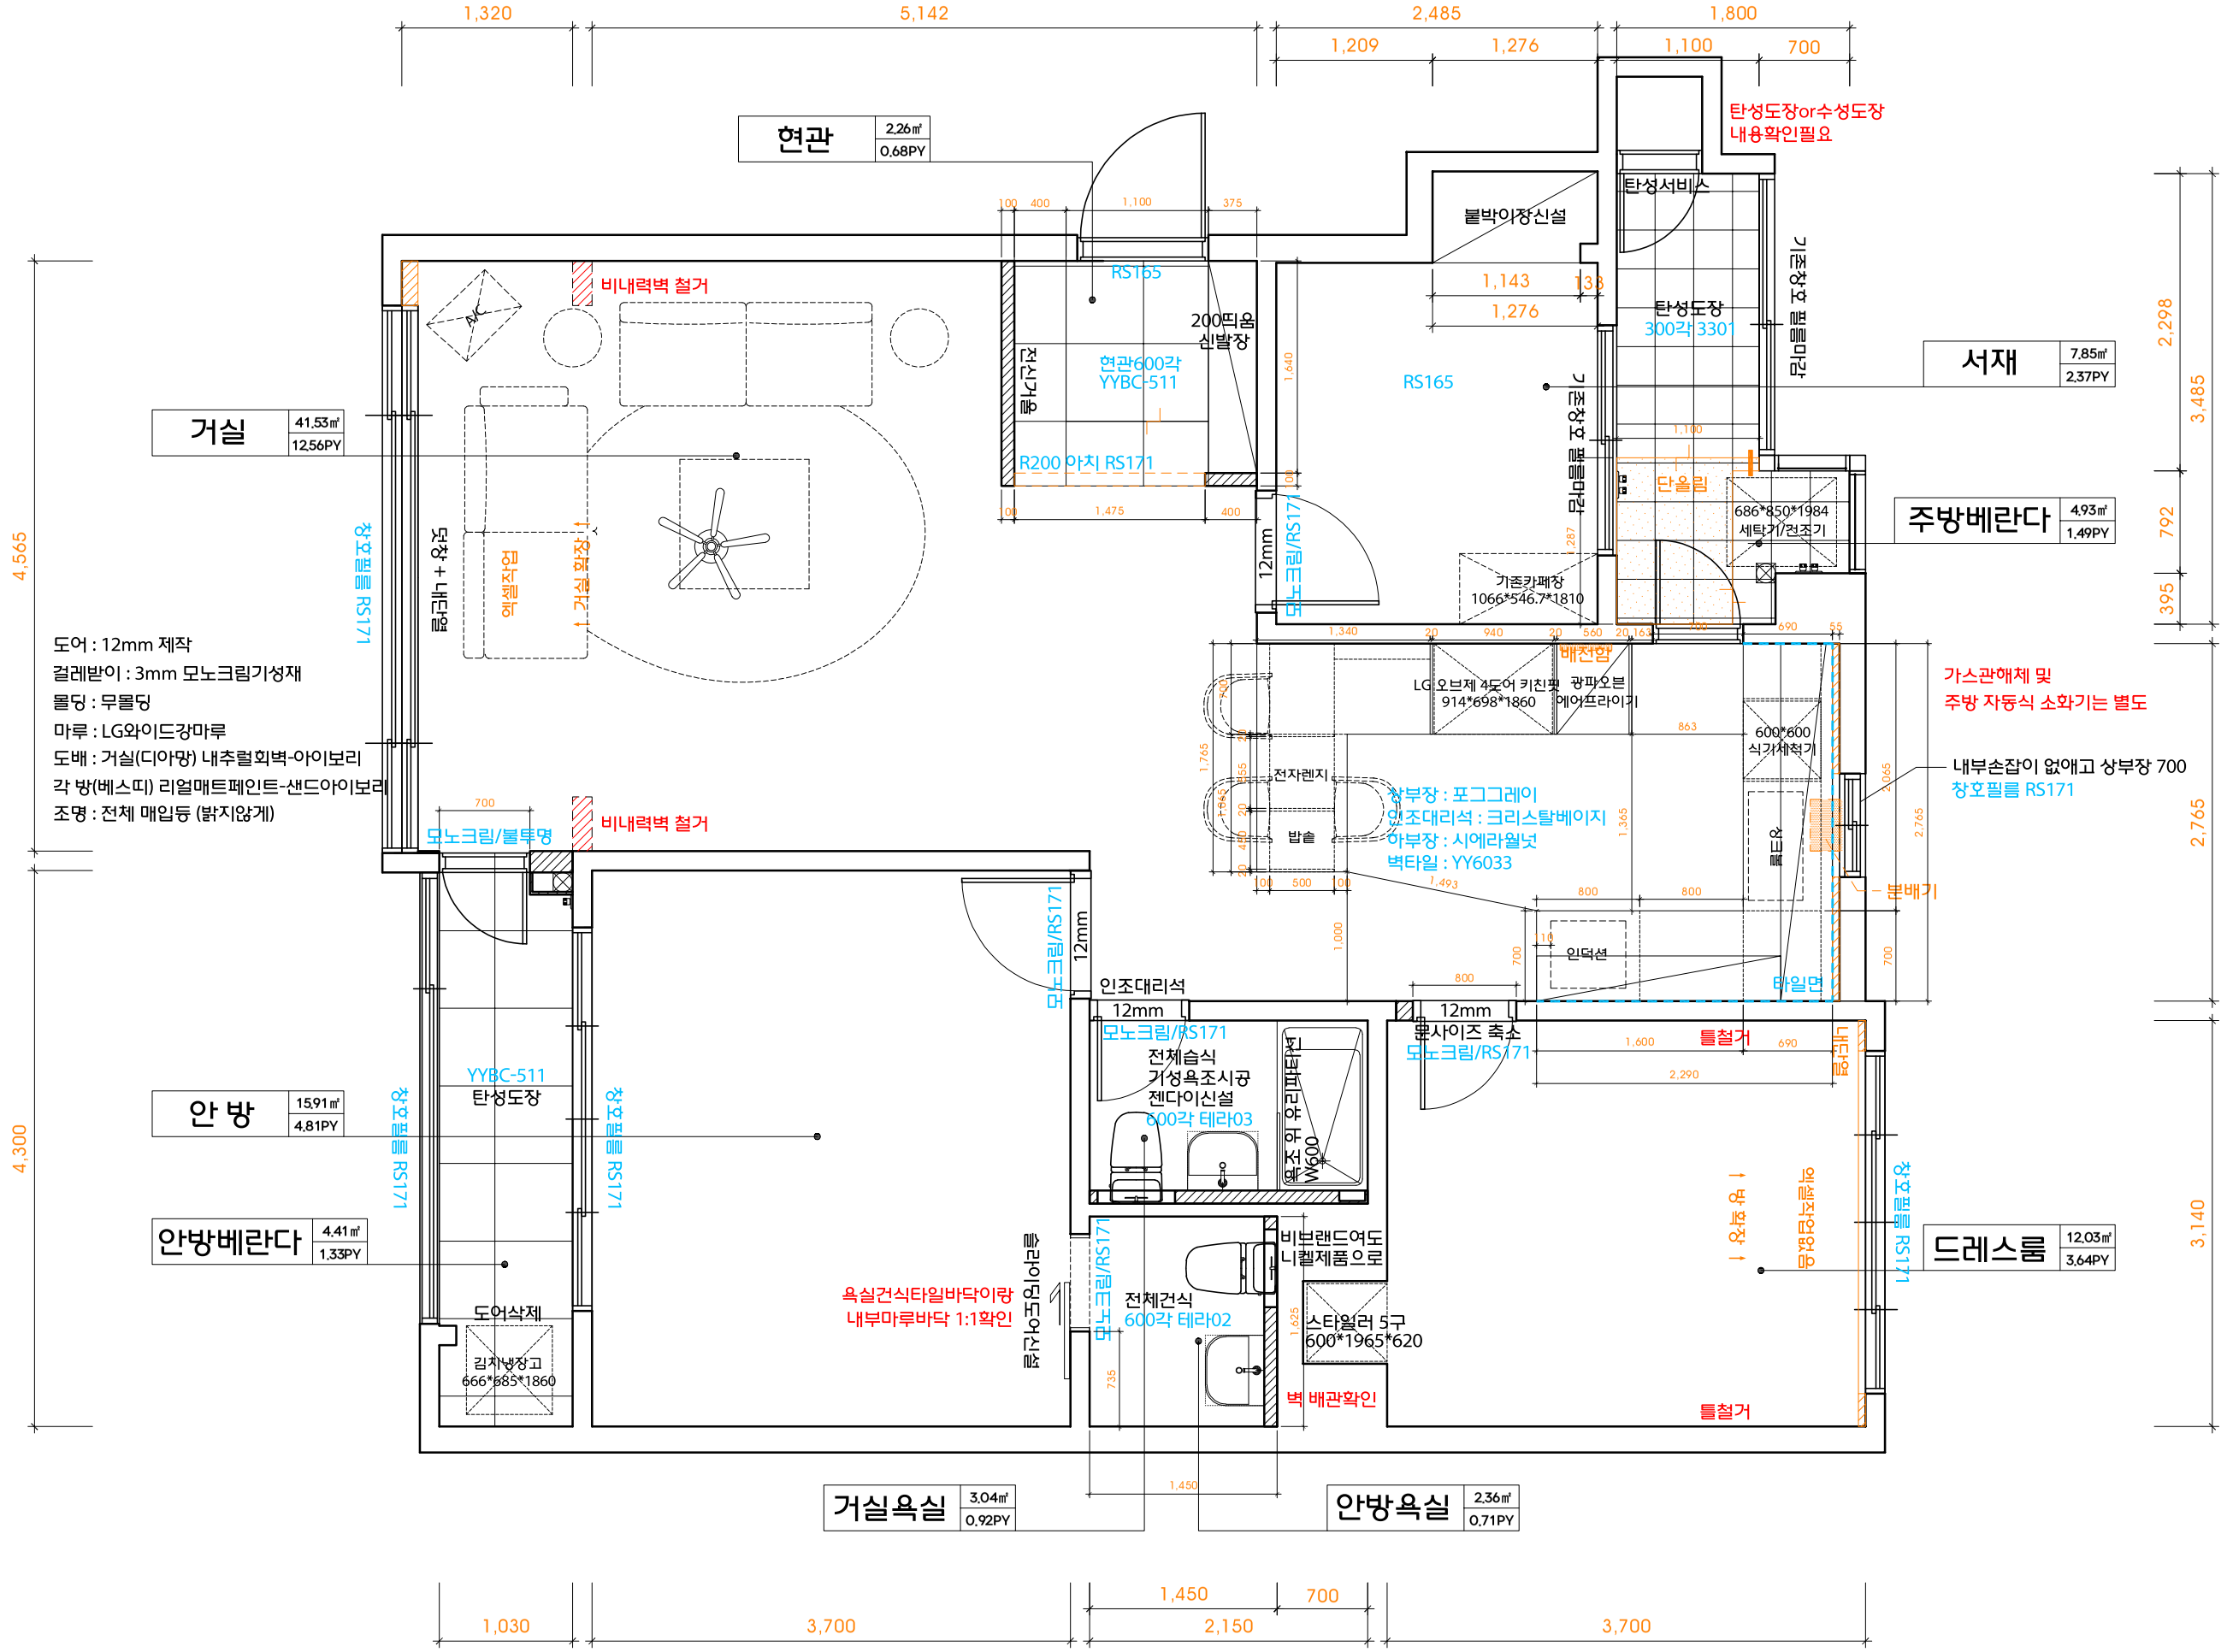


DESIGN BY.

GM
황 금 손 인 테 리 어

@__gmdesign__
goldenhand99@naver.com

REMARK.

철거부분
현관 : 중문, 프레임일체, 인조대리석
거실 : 내창, 내창양옆벽체, 확장부분 바닥 및 천정
주방 : 타일벽면, 기존가구일체
안방 :
서재 : 기존 장
드레스룸 : 기존 장
주방베란다 : 빨래대철거, 도어?
안방베란다 : 공틀장 도어
전체 : 각 방 도어철거(5조)
신설부분
현관 : 덧방, 가벽, 현관필름, 신발장
거실 : TV반매립, 터닝도어(1조+1?)
덧창, 내단열, 확장부분엑셀+천정
주방 : ㄱ+ㄴ주방, 창호손잡이+필름
벽 타일 신설
안방 : 기존창호필름, 욕실슬라이딩도어
서재 : 붙박이장, 기존창호필름
드레스룸 : 확장(엑셀없음), 내단열,천정
기존창호 필름마감
주방베란다 : 단높임, 출입문필름, 터닝?
공틀장도어 위 도장마감, 덧방
안방베란다 : 덧방, 기존창호필름
전체 : 기존창호/도어 필름마감

SITE CONDITIONS.

ADDRESS.
일도대유대림
309동 502호

AREA.
100.91 m2 / 30.53py

HEIGHT.
2280mm(최고2318mm)

PROJECT TYPE.
아파트 리모델링

PROJECT TITLE.
일도대유대림 309-502

DRAWING TITLE.
평 면 도

SCALE.
A1:1/00 A3:1/50

DATE.
25.01.16

DRAWN BY.	CHECKED BY.
DRAWING No.	SHEET No.

비번 0608

- 본 도서는 어떠한 경우에도 무단으로 도용할 수 없으며 도용시 '지적재산권' 보호에 관한 법률에 의거, 법적 분쟁이 발생합니다. 또한 본 도서에 관한 모든 저작권은 당사에 있습니다. -