
총 면적 : 107.28㎡ / 32.5PY

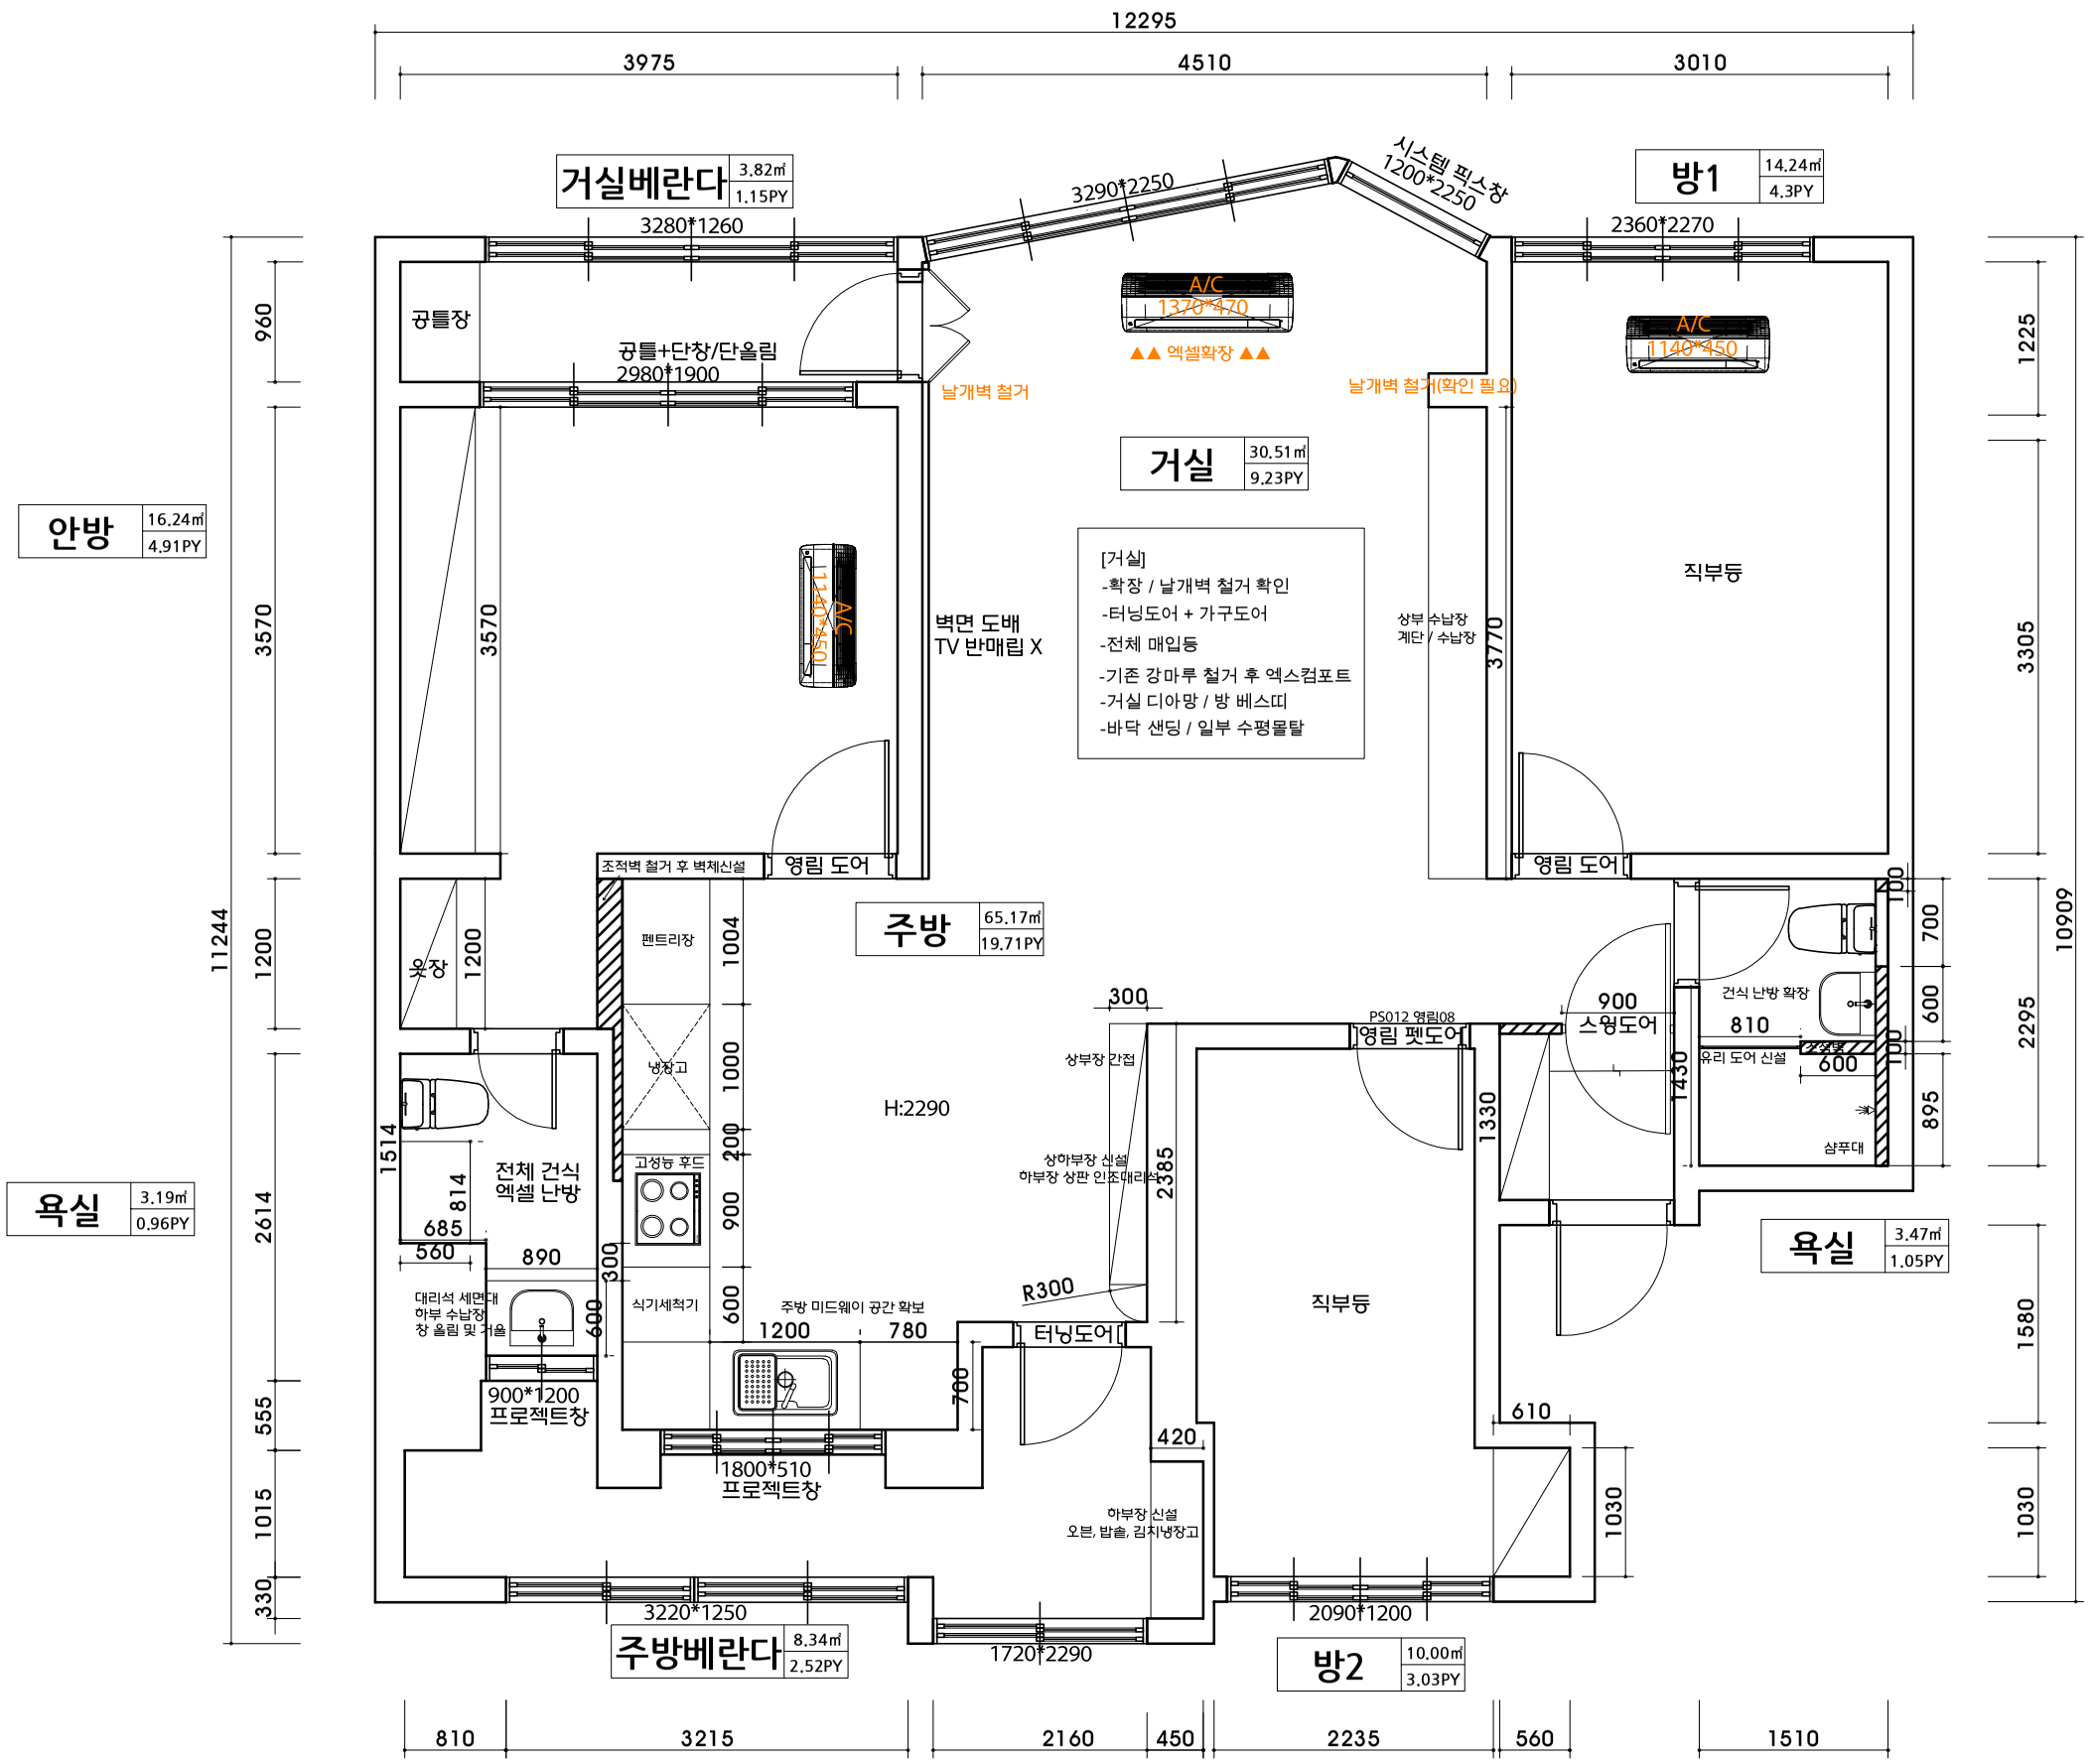

[안방]
-창호 높이 조절

[주방]
-창호 프로젝트창
-인덕션 이동? / 고성능후드
-벽체 철거 후 냉장고 / 펜트리장
-터닝도어 신설 / 벽면 상하부장(미드웨이)

[거실욕실]
-조적 샤푸대/조적파티션/유리도어
-건식 엑셀 난방

[안방욕실]
-전체 건식 / 엑셀 난방
-대리석 세면대 / 하부장
-창 높이 줄임 / 거울 부착

[방1]
-직부등 / 시스템에어컨
-붙박이장 여부 확인 필요

[방2]
-붙박이장 신설

[에어컨]
-시스템 에어컨 3개 : 방2개+거실

[디자인]
-도어 : 영림 도어
-마루 : 엑스컴포트
-도배 : 거실 디아망 / 방 베스띠
-거실 무몰딩

[주방 베란다]
-세탁기, 건조기
-터닝도어 / 하부장 신설

DESIGN BY.

M2
디 자 인 엠 제 곱

@_m2design_
m2gmg@naver.com

PROJECT.

SITE CONDITIONS.

ADDRESS.
제주시 원노형로 90
노형아이파크 103-802

AREA.
m2 / py

HEIGHT.
0000mm

PROJECT TYPE.
평 면 도

PROJECT TITLE.
노형아이파크 103-802

DRAWING TITLE.

SCALE.
A1:1/30 A3:1/60

DATE.
25.12.26

DRAWN BY.	CHECKED BY.
DRAWING No.	SHEET No.

- 본 도서는 어떠한 경우에도 무단으로 도용할 수 없으며 도용시 '지적재산권' 보호에 관한 법률에 의거, 법적 분쟁이 발생합니다. 또한 본 도서에 관한 모든 저작권은 당사에 있습니다. -