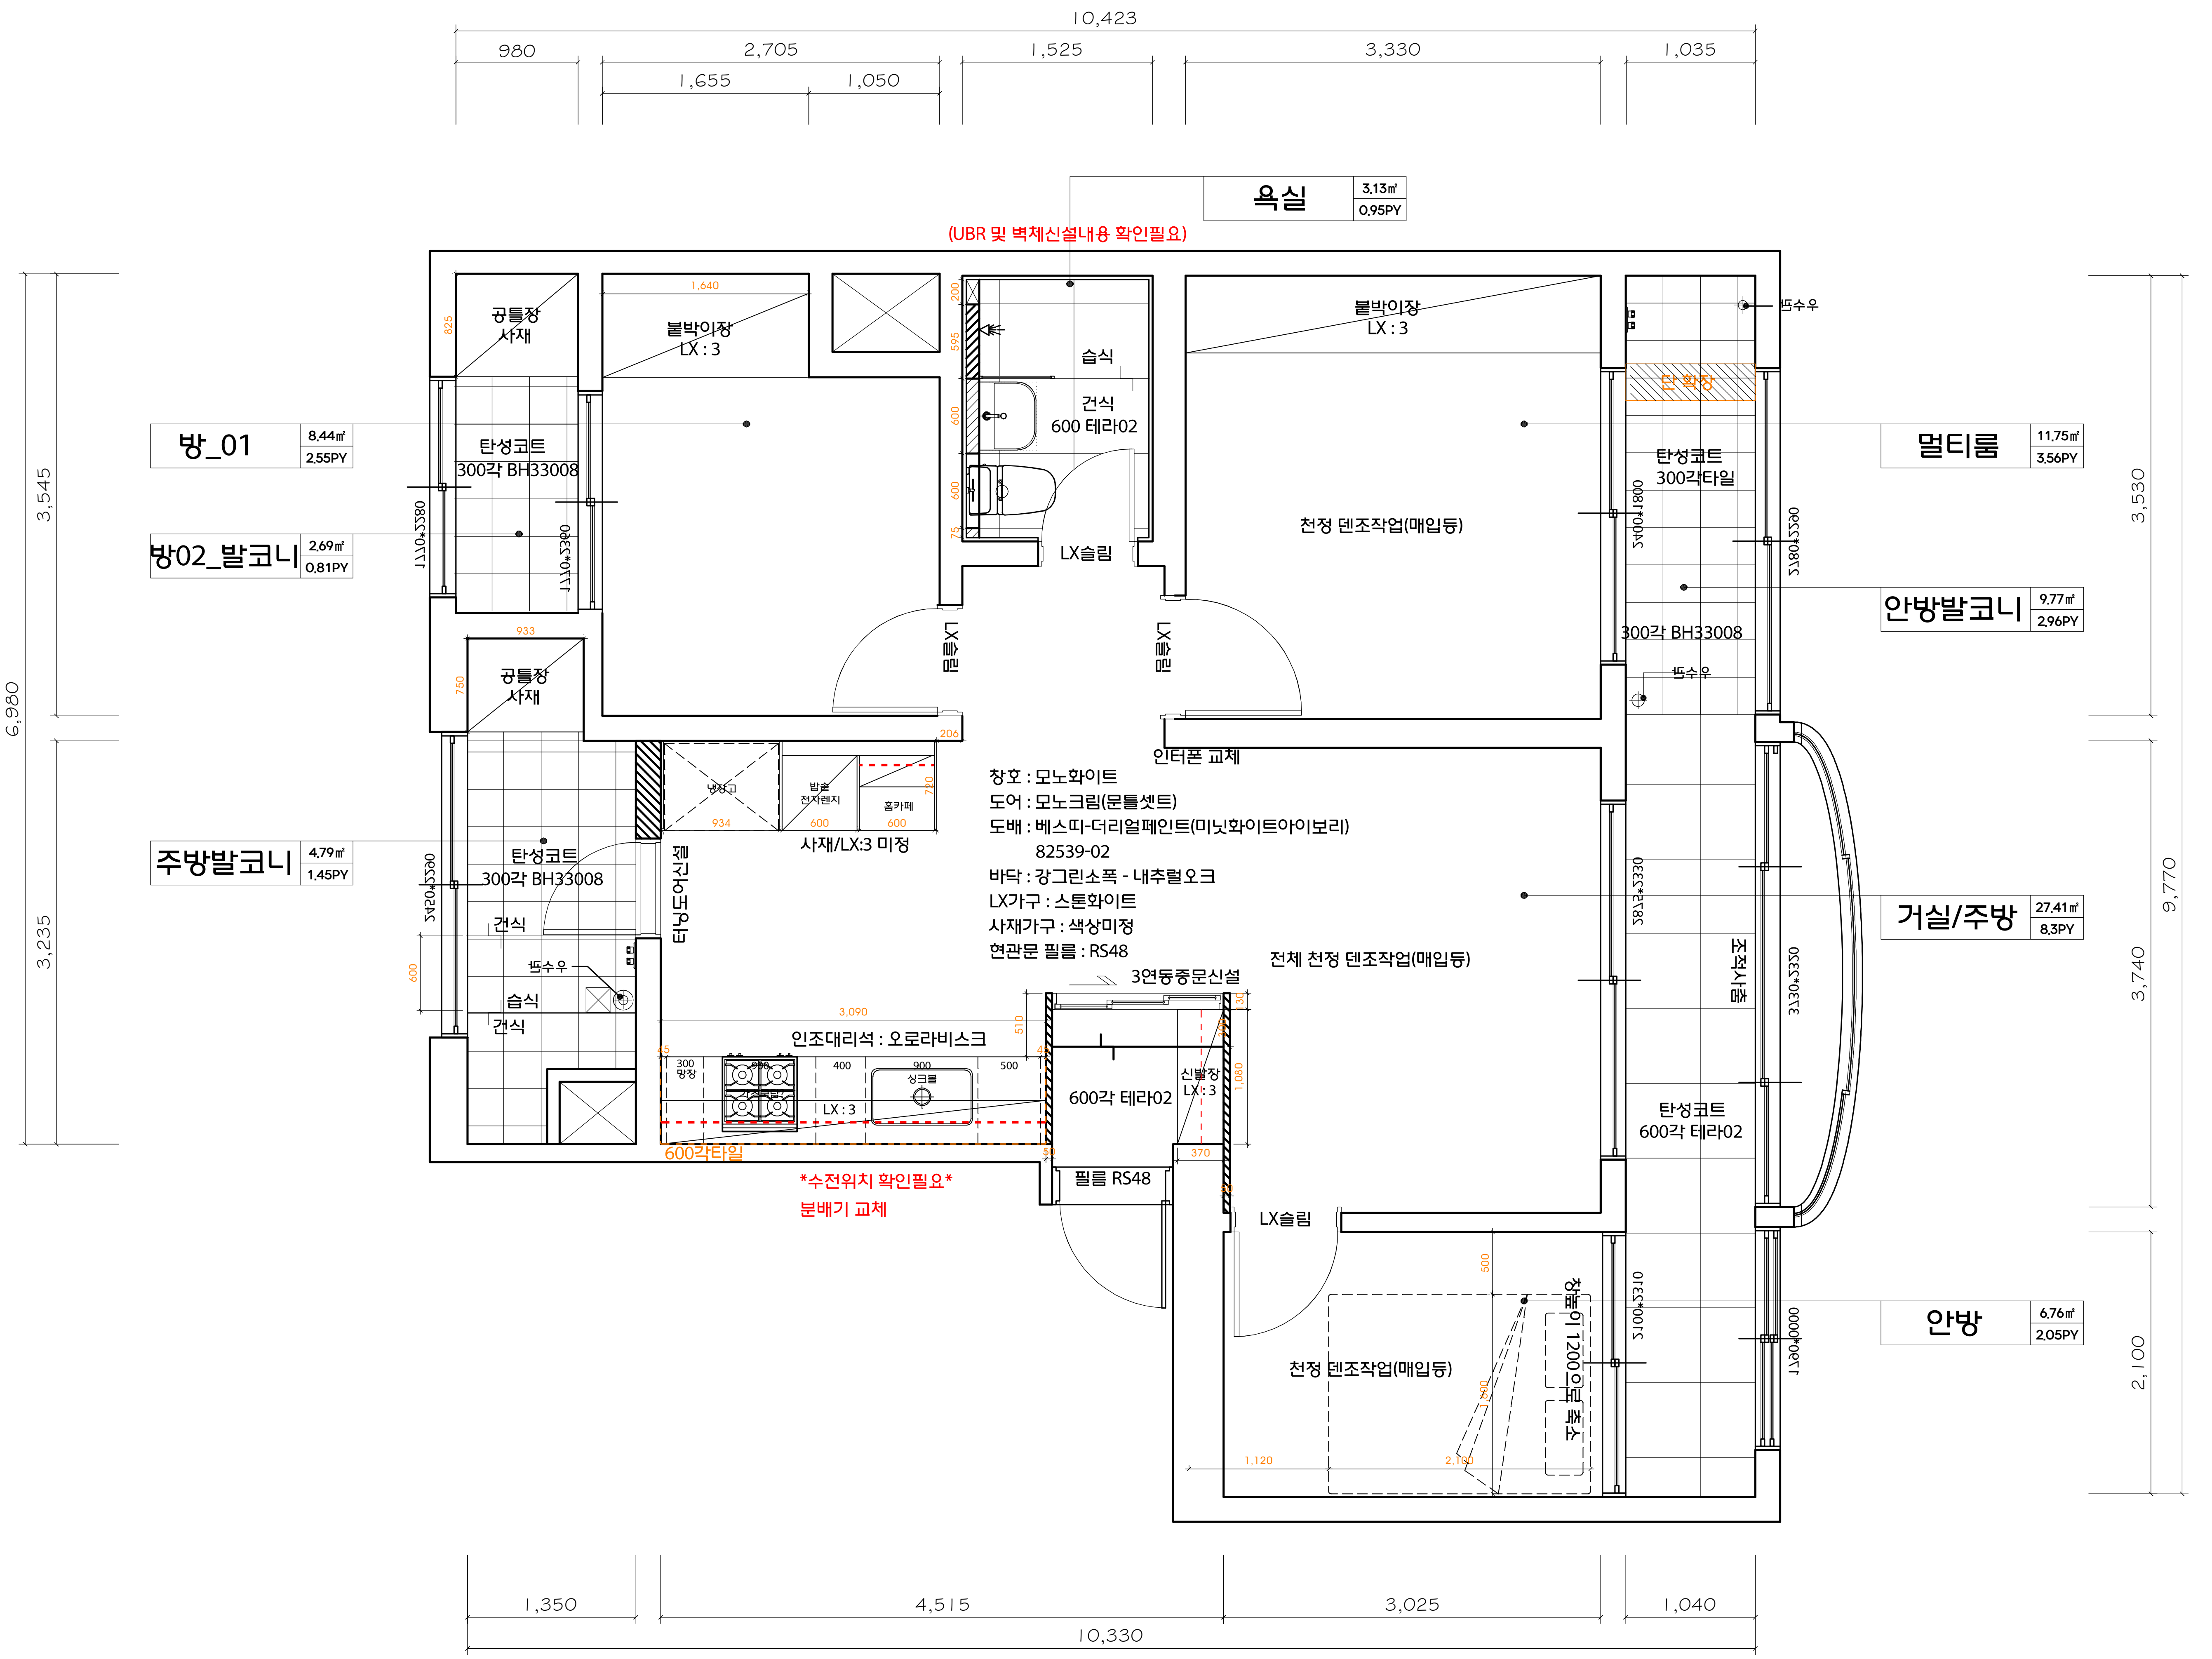
10,423
980
2,705
1,525
3,330
1,035
1,655
1,050
욕실 3.13㎡ 0.95PY
(UBR 및 벽체신설내용 확인필요)
공틀장 사재
1,640
붙박이장 LX : 3
습식
건식
600 테라02
LX슬림
붙박이장 LX : 3
단 확장
뜨수우
방_01 8.44㎡ 2.55PY
탄성코트 300각 BH33008
방02_발코니 2.69㎡ 0.81PY
멀티룸 11.75㎡ 3.56PY
탄성코트 300각타일
천정 덴조작업(매입등)
안방발코니 9.77㎡ 2.96PY
300각 BH33008
뜨수우
933
공틀장 사재
LX슬림
LX슬림
인터폰 교체
냉장고
밥솥 전자렌지
홈카페
934
600
600
720
206
사재/LX:3 미정
주방발코니 4.79㎡ 1.45PY
탄성코트 300각 BH33008
터닝도어신설
건식
뜨수우
습식
건식
600
전체 천정 덴조작업(매입등)
3연동중문신설
3,090
인조대리석 : 오로라비스크
300 망장
900
400
900 싱크볼
500
LX : 3
45
45
510
600각 테라02
신발장 LX : 3
130
300
1,080
370
50
50
600각타일
수전위치 확인필요
분배기 교체
필름 RS48
LX슬림
거실/주방 27.41㎡ 8.3PY
조적사춤
탄성코트 600각 테라02
안방 6.76㎡ 2.05PY
천정 덴조작업(매입등)
장롱이 1200으로 축소
500
1,120
2,100
1,350
4,515
3,025
1,040
10,330
3,545
3,235
6,980
3,530
3,740
2,100
9,770

창호 : 모노화이트
도어 : 모노크림(문틀셋트)
도배 : 베스띠-더리얼페인트(미닛화이트아이보리)
82539-02
바닥 : 강그린소폭 - 내추럴오크
LX가구 : 스톤화이트
사재가구 : 색상미정
현관문 필름 : RS48

DESIGN BY.

GM
황금손인테리어

@__gmdesign__
goldenhand99@naver.com

PROJECT.

* 철거부분
창호 : 전체 / 도어 : 4 셋트
가구 : 신발장, 안방/방1 붙박이장
방1베란다/베란다 공틀장
천정 : 거실~주방, 안방 (덴조새로칠것)
욕실 : 전체철거 후 신설
(UBR 및 벽체신설내용 확인필요)

SITE CONDITIONS.

ADDRESS.
해오름아파트
103동 804호

AREA.
81.71m2 / 24.72py

HEIGHT.
2300mm(거실)

PROJECT TYPE.
아파트 리모델링

PROJECT TITLE.
해오름103동 804호

DRAWING TITLE.
평 면 도

SCALE.
A1:1/00 A3:1/50

DATE.
25.11. 06

DRAWN BY.	CHECKED BY.
DRAWING No.	SHEET No.

- 본 도서는 어떠한 경우에도 무단으로 도용할 수 없으며 도용시 '지적재산권' 보호에 관한 법률에 의거, 법적 분쟁이 발생합니다. 또한 본 도서에 관한 모든 저작권은 당사에 있습니다. -