\\admin-pc01\공유폴더\■ 황금손\01_현장\★250701_대원길 13 영도그린힐 102동402호 인테리어공사\02_도면\250728_영도그린힐102동402호.dwg,2025-07-2

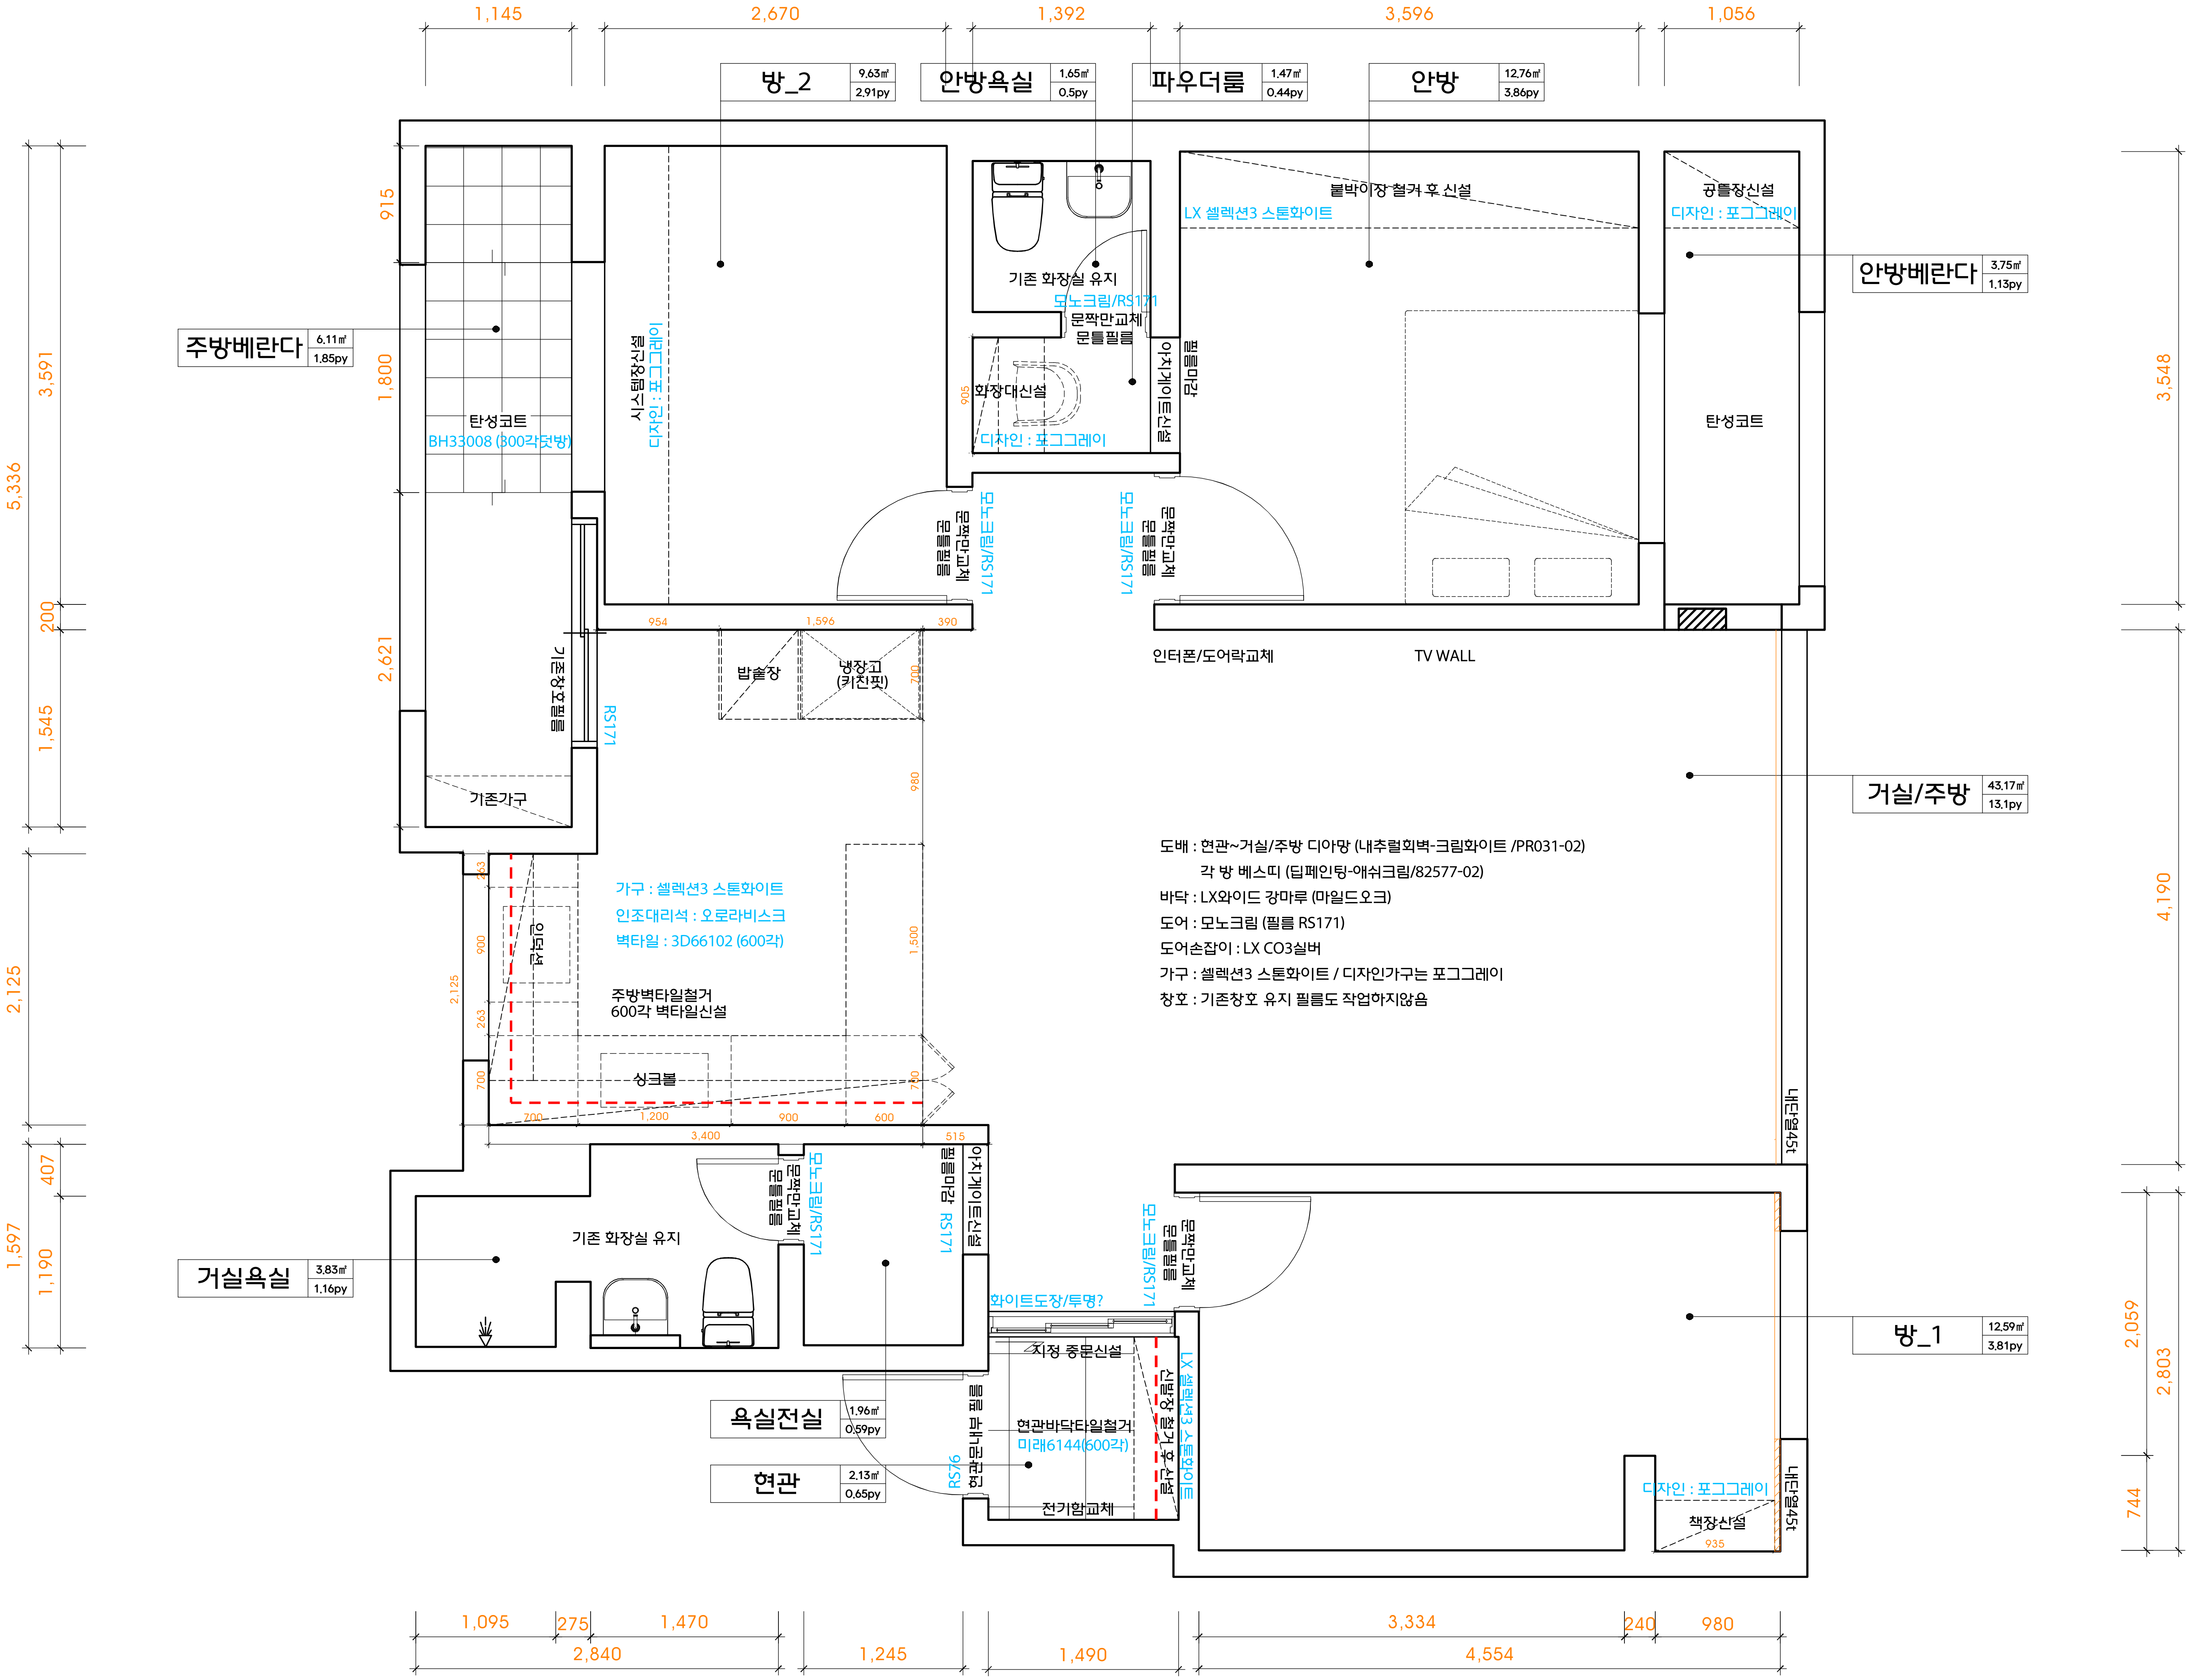

도배 : 현관~거실/주방 디아망 (내추럴회벽-크림화이트 /PR031-02)
각 방 베스띠 (딥페인팅-애쉬크림/82577-02)
바닥 : LX와이드 강마루 (마일드오크)
도어 : 모노크림 (필름 RS171)
도어손잡이 : LX CO3실버
가구 : 셀렉션3 스톤화이트 / 디자인가구는 포그그레이
창호 : 기존창호 유지 필름도 작업하지않음

DESIGN BY.

M2
디 자 인 엠 제 곱

@_m2design_
m2gmg@naver.com

REMARK.

** 철거부분 **
가구 : 싱크대, 주방장, 안방붙박이장, 신발장
거실욕실 앞 붙박이장, 안방베란다장
도어 : 중문, 각 도어 문짝 5개
타일 : 주방벽타일, 현관바닥타일
기타 : 몰딩,걸레받이, 조명/스위치/콘센트 등
전체바닥 마루/장판, 인터폰
필름 : 현관문내부, 전체창호
도배 : 거실(디아망), 각 방(베스띠)
바닥 : 강마루 와이드
도어 : 5짝 도어문짝만 교체
걸레받이/몰딩 : 신설
에어컨박스 : 3개 신설
거실 실링팬부분 합판보강
주방베란다 미닫이문 철거 후 터닝도어신설
중문 : 3연동으로 추천
도장 : 주방베란다, 안방베란다 탄성코트

SITE CONDITIONS.

ADDRESS.
제주시 대원길 13
영도그린힐 102동 402호

AREA.
108.03m2 / 32.68py

HEIGHT.
2413mm

PROJECT TYPE.
아파트 리모델링

PROJECT TITLE.
영도그린힐 102동402호

DRAWING TITLE.
평 면 도

SCALE.
A1:1/25 A3:1/50

DATE.
25.07.28

DRAWN BY.
CHECKED BY.

DRAWING No.
SHEET No.

– 본 도서는 어떠한 경우에도 무단으로 도용할 수 없으며 도용시 '지적재산권' 보호에 관한 법률에 의거, 법적 분쟁이 발생합니다. 또한 본 도서에 관한 모든 저작권은 당사에 있습니다. –