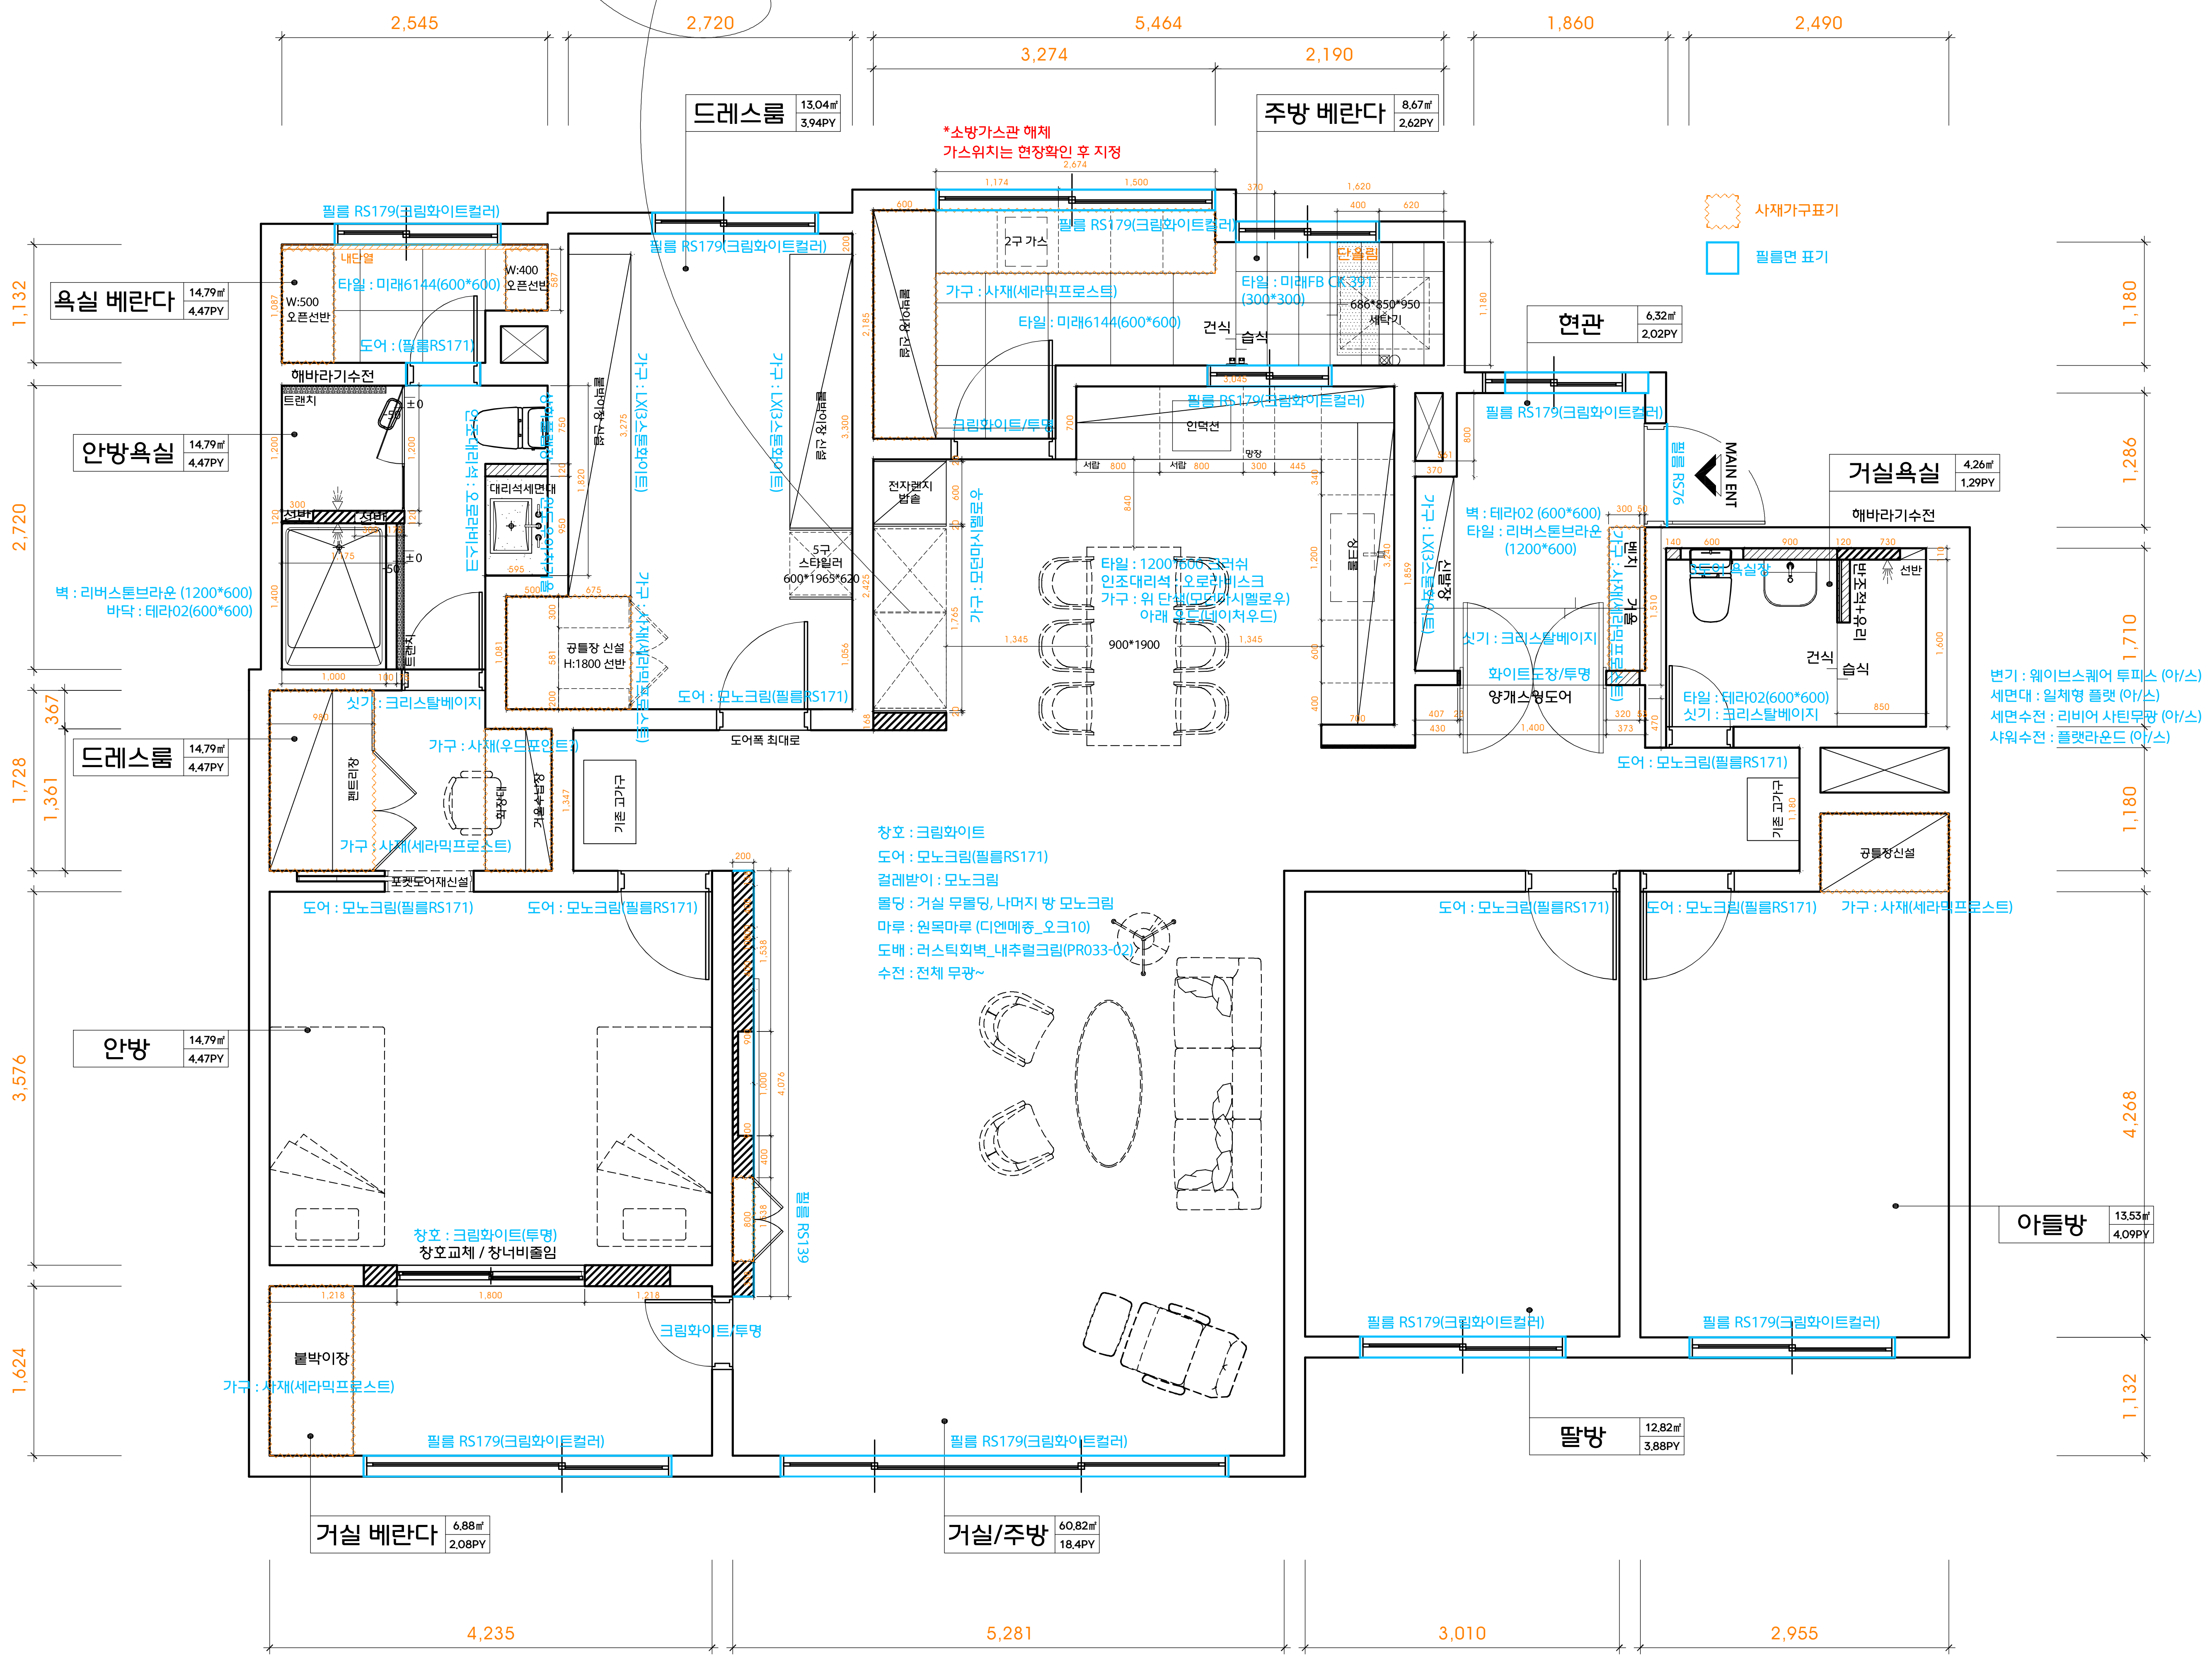
2,545
2,720
5,464
3,274
2,190
1,860
2,490
드레스룸 13.04㎡ 3.94PY
주방 베란다 8.67㎡ 2.62PY
*소방가스관 해체
가스위치는 현장확인 후 지정
필름 RS179(크림화이트컬러)
사재가구표기
필름면 표기
욕실 베란다 14.79㎡ 4.47PY
내단열
타일 : 미래6144(600*600)
W:400 오픈선반
W:500 오픈선반
도어 : (필름RS171)
해바라기수전
트랜치
안방욕실 14.79㎡ 4.47PY
벽 : 리버스톤브라운 (1200*600)
바닥 : 테라02(600*600)
대리석세면대
가구 : LX(3스톤화이트)
2구 가스
가구 : 사재(세라믹프로스트)
타일 : 미래6144(600*600)
건식
습식
타일 : 미래FB CK391 (300*300)
단열필
686*850*950 세탁기
현관 6.32㎡ 2.02PY
필름 RS179(크림화이트컬러)
인덕션
크림화이트/투명
전자렌지 밥솥
5구 스타일러 600*1965*620
가구 : 모던사멜로우
타일 : 1200*600 크러쉬
인조대리석 : 오로라비스크
가구 : 위 단재(모던시멜로우)
아래 우드(네이처우드)
900*1900
필름 RS76
MAIN ENT
벽 : 테라02 (600*600)
타일 : 리버스톤브라운 (1200*600)
신발장
싯기 : 크리스탈베이지
화이트도장/투명
양개스윙도어
거실욕실 4.26㎡ 1.29PY
해바라기수전
도어욕실장
선반
반조적+유리
건식
습식
타일 : 테라02(600*600)
싯기 : 크리스탈베이지
변기 : 웨이브스퀘어 투피스 (아/스)
세면대 : 일체형 플랫 (아/스)
세면수전 : 리버어 사틴무광 (아/스)
샤워수전 : 플랫라운드 (아/스)
도어 : 모노크림(필름RS171)
공틀장 신설 H:1800 선반
드레스룸 14.79㎡ 4.47PY
싯기 : 크리스탈베이지
가구 : 사재(우드포인트)
가구 : 사재(세라믹프로스트)
포켓도어재신설
도어폭 최대로
기존 고가구
창호 : 크림화이트
도어 : 모노크림(필름RS171)
걸레받이 : 모노크림
몰딩 : 거실 무몰딩, 나머지 방 모노크림
마루 : 원목마루 (디앤메종_오크10)
도배 : 러스틱회벽_내추럴크림(PR033-02)
수전 : 전체 무광~
공틀장신설
가구 : 사재(세라믹프로스트)
안방 14.79㎡ 4.47PY
창호 : 크림화이트(투명)
창호교체 / 창너비줄임
필름 RS139
크림화이트/투명
붙박이장
가구 : 사재(세라믹프로스트)
아들방 13.53㎡ 4.09PY
딸방 12.82㎡ 3.88PY
거실 베란다 6.88㎡ 2.08PY
거실/주방 60.82㎡ 18.4PY
1,132
2,720
1,728
367
1,361
3,576
1,624
1,180
1,286
1,710
1,180
4,268
1,132
4,235
5,281
3,010
2,955

DESIGN BY.

GM
황 금 손 인 테 리 어

@_m2design_
m2gmg@naver.com

REMARK.

SITE CONDITIONS.

ADDRESS.
제주시 노형동 2585-1
미리내마을중흥S 102동 203호

AREA.
142.65m2 / 43.14py

HEIGHT.
mm()

PROJECT TYPE.
아파트 리모델링

PROJECT TITLE.
미리내 102동 203

DRAWING TITLE.
평 면 도

SCALE.
A1:1/30 A3:1/60

DATE.
25.07.10

DRAWN BY.	CHECKED BY.
DRAWING No.	SHEET No.

- 본 도서는 어떠한 경우에도 무단으로 도용할 수 없으며 도용시 '지적재산권' 보호에 관한 법률에 의거, 법적 분쟁이 발생합니다. 또한 본 도서에 관한 모든 저작권은 당사에 있습니다. -