
* 현장철거 후 실측 필수 *

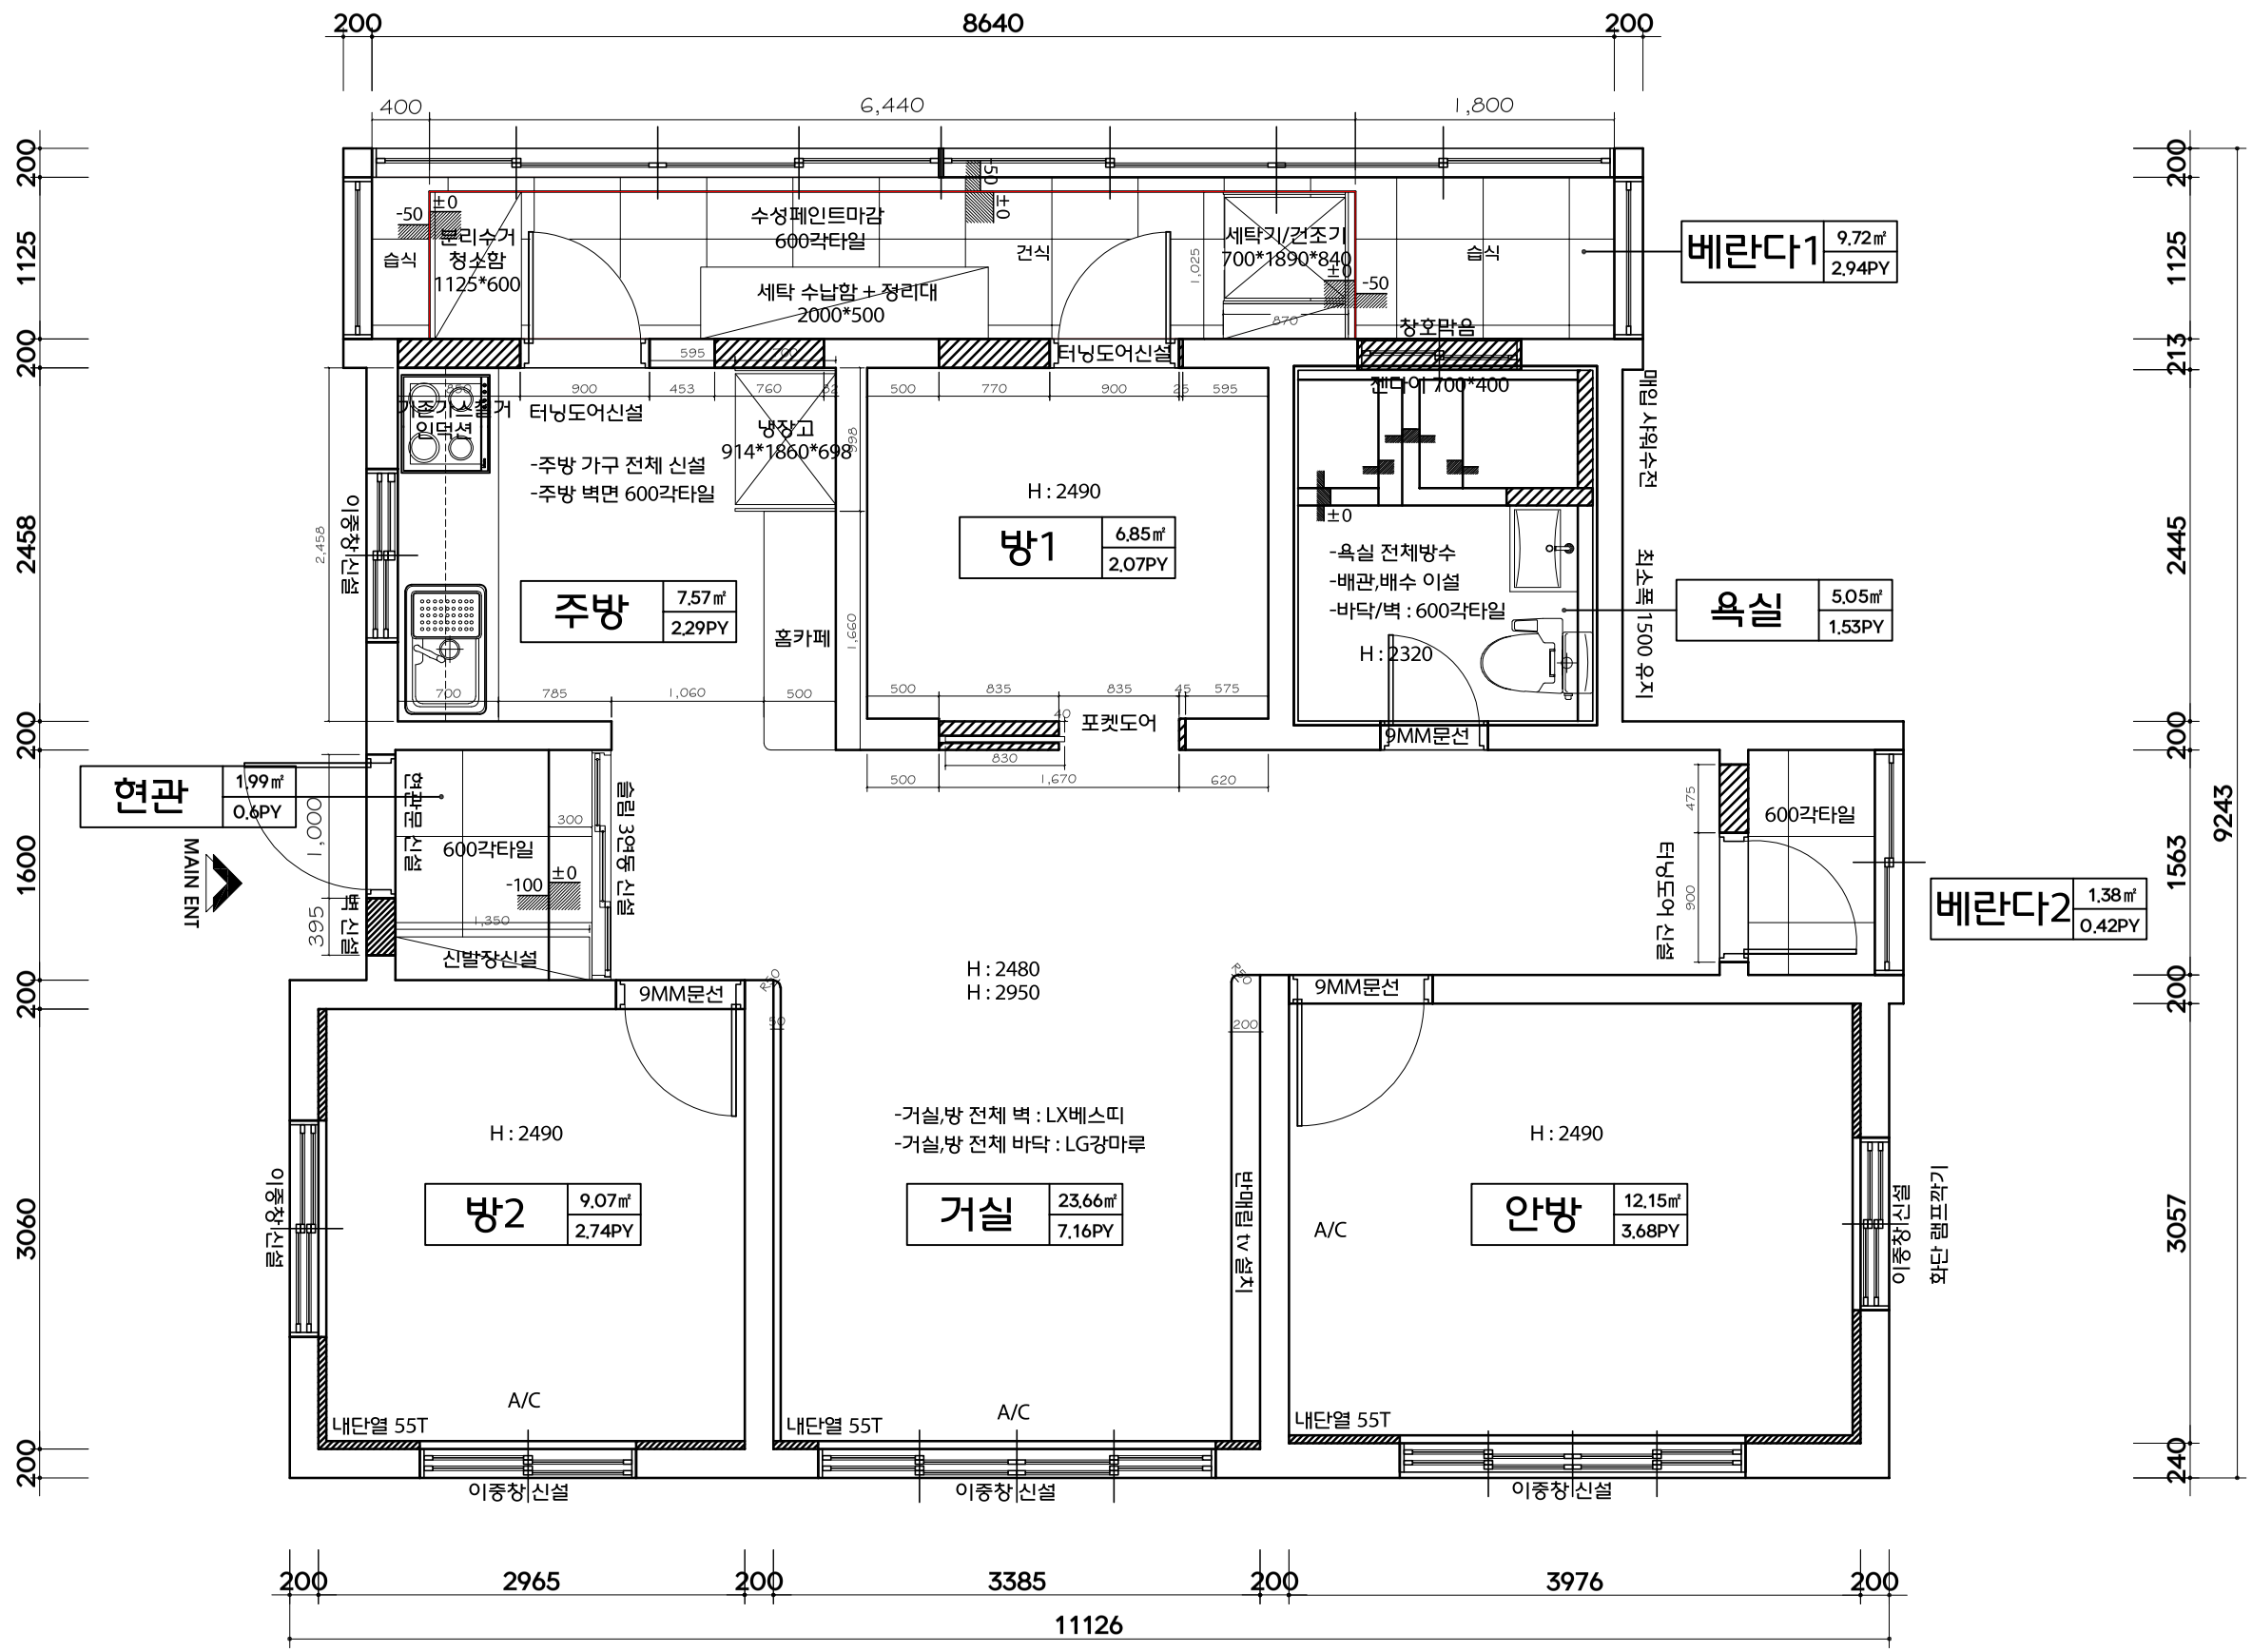

DESIGN BY.

Hand of midas
황 금 손

@__gmdesign__
goldenhand99@naver.com

PROJECT.

REMARK.

SITE CONDITIONS.

ADDRESS.
계명3길 27-8
단독 2층

AREA.
77.21 m2 / 23.39py

HEIGHT.
2480mm/2950mm

PROJECT TYPE.
구옥 리모델링

PROJECT TITLE.
계명3길 27-8 구옥

DRAWING TITLE.
평 면 도

SCALE.
A1:1/00 A3:1/50

DATE.
24.05.16

DRAWN BY.	CHECKED BY.

DRAWING No.	SHEET No.
I-002	001

- 본 도서는 어떠한 경우에도 무단으로 도용할 수 없으며 도용시 '지적재산권' 보호에 관한 법률에 의거, 법적 분쟁이 발생합니다. 또한 본 도서에 관한 모든 저작권은 당사에 있습니다. -