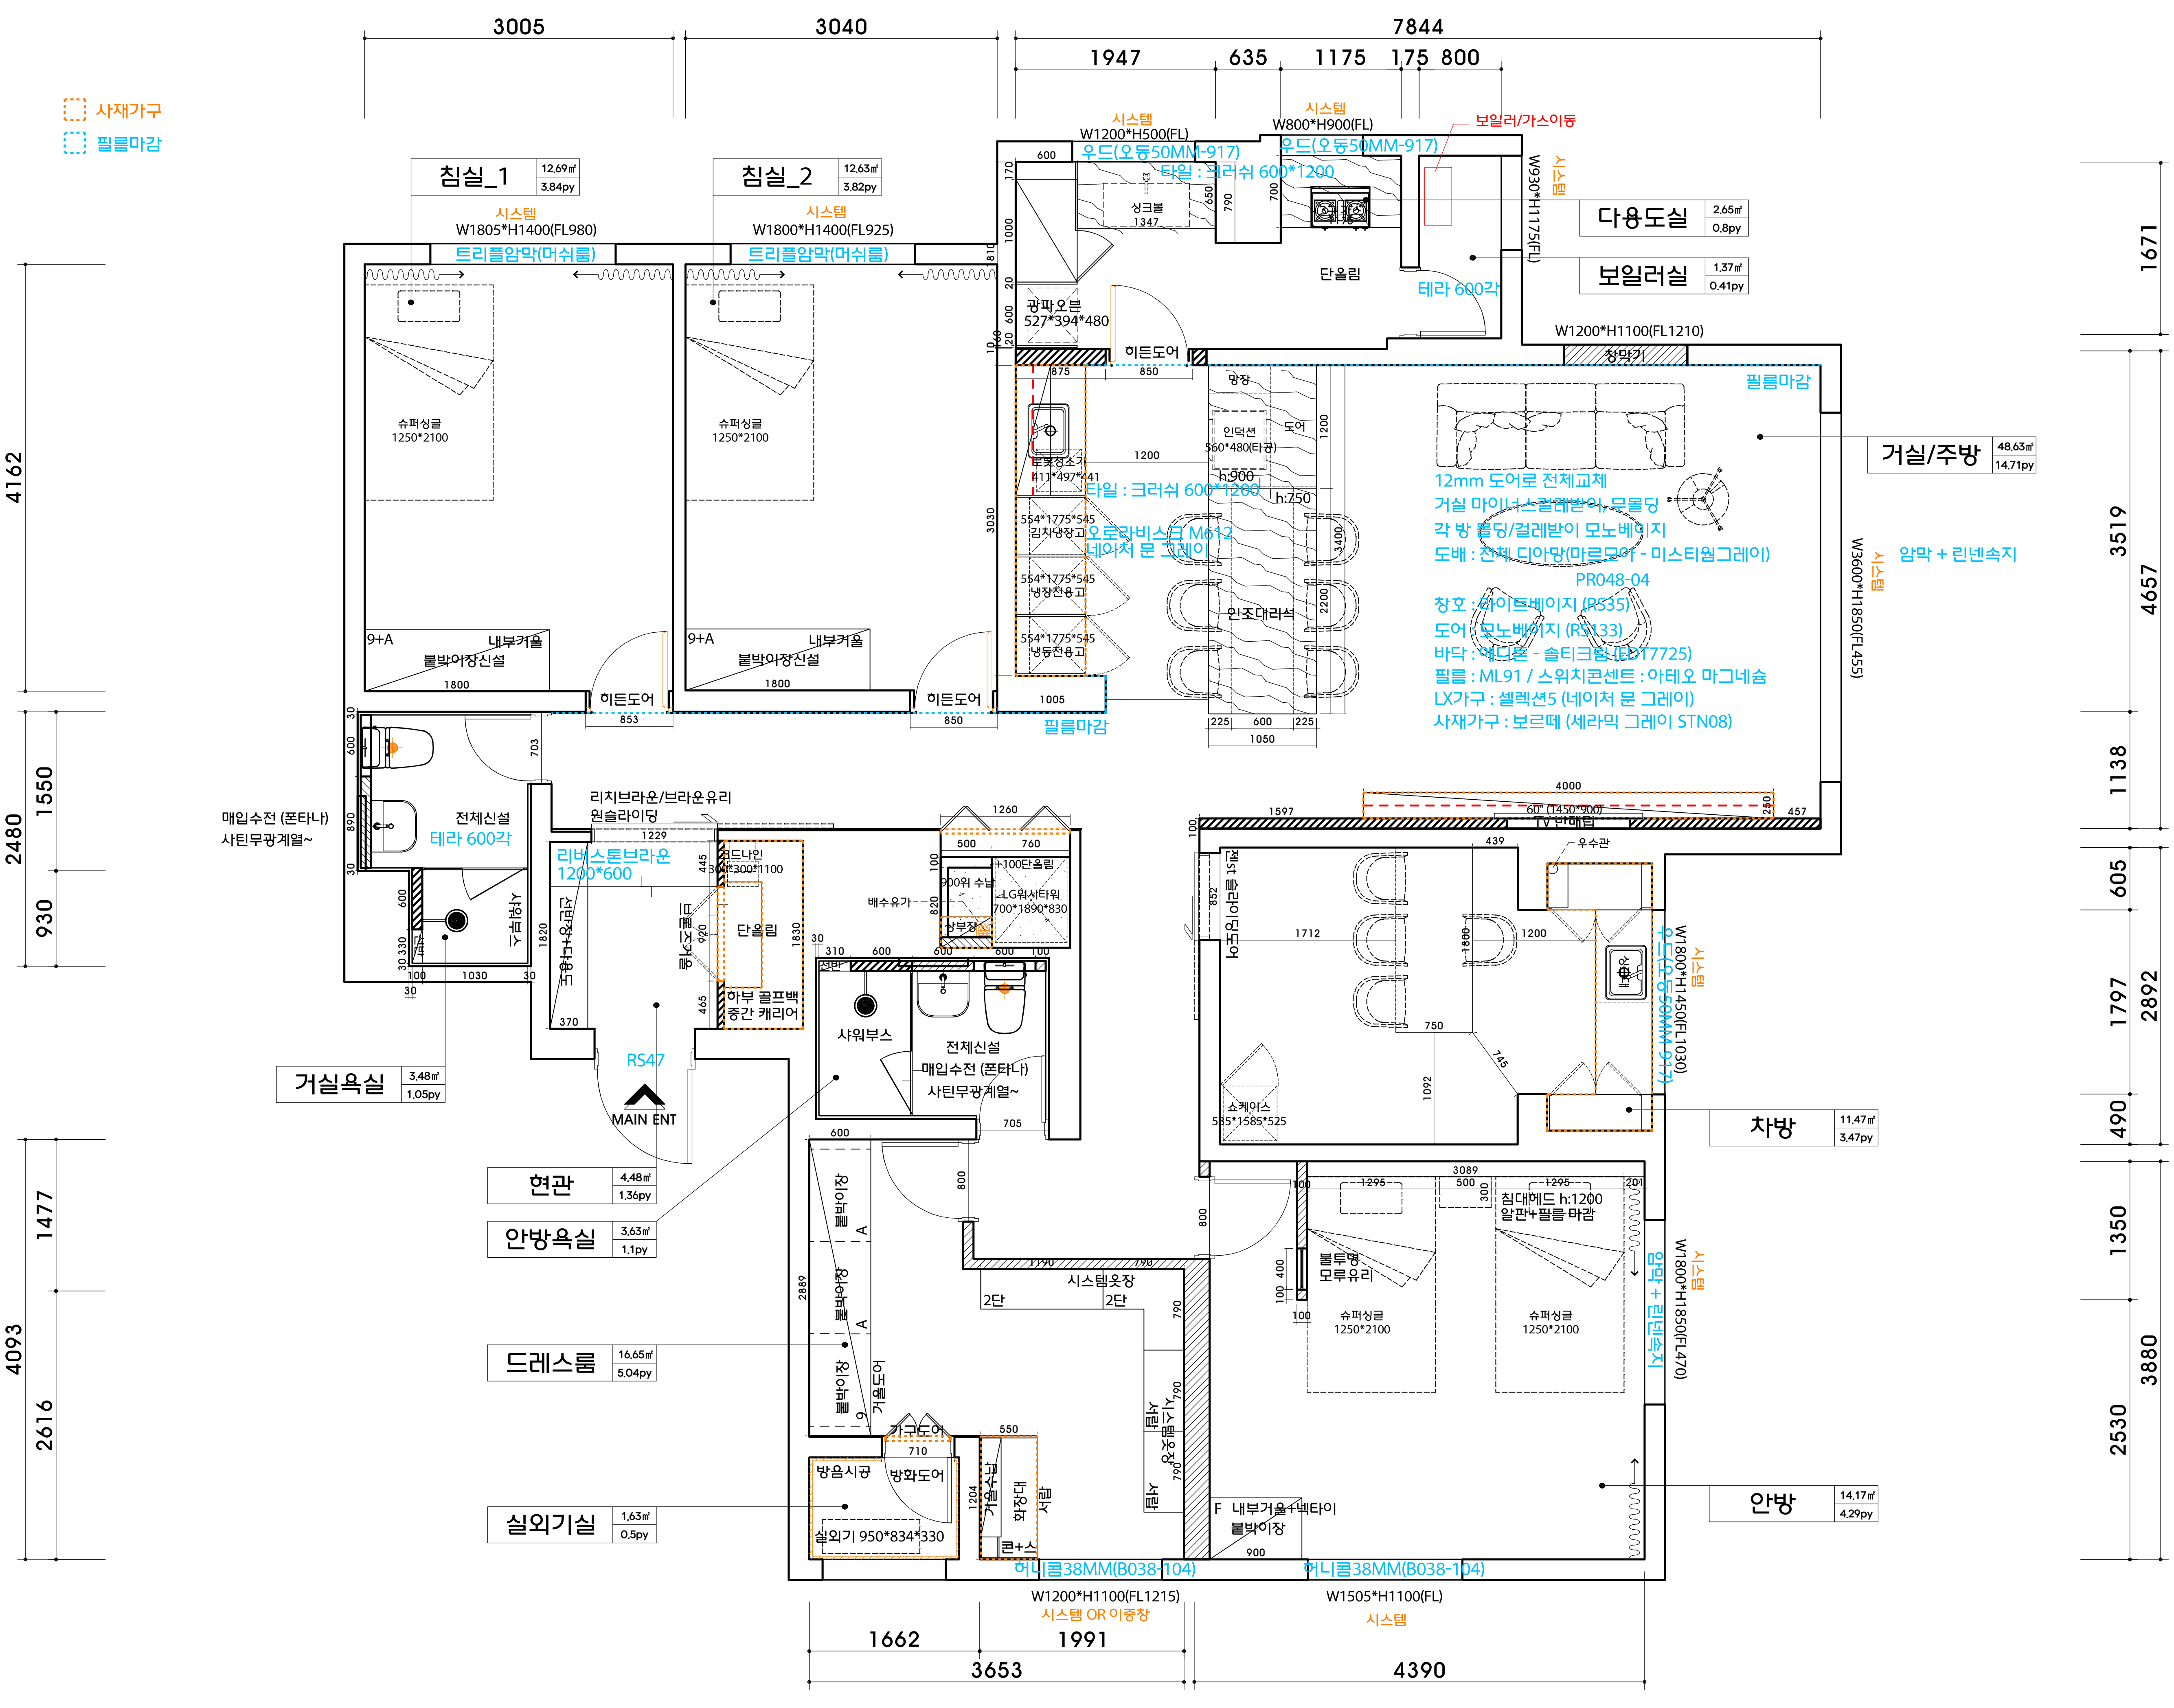
사재가구
필름마감
3005
3040
7844
1947
635
1175
175
800
4162
2480
1550
930
4093
1477
2616
1671
3519
4657
1138
605
1797
2892
490
1350
3880
2530
1662
1991
3653
4390
침실_1
12.69㎡
3.84py
시스템
W1805*H1400(FL980)
트리플암막(머쉬룸)
슈퍼싱글
1250*2100
9+A
내부거울
붙박이장신설
1800
히든도어
853
침실_2
12.63㎡
3.82py
시스템
W1800*H1400(FL925)
트리플암막(머쉬룸)
슈퍼싱글
1250*2100
9+A
내부거울
붙박이장신설
1800
히든도어
850
시스템
W1200*H500(FL)
우드(오동50MM-917)
타일 : 크러쉬 600*1200
시스템
W800*H900(FL)
우드(오동50MM-917)
보일러/가스이동
싱크볼
1347
광파오븐
527*394*480
히든도어
850
875
단올림
테라 600각
W930*H1175(FL)
시스템
다용도실
2.65㎡
0.8py
보일러실
1.37㎡
0.41py
W1200*H1100(FL1210)
창막기
필름마감
망장
인덕션
560*480(타공)
도어
h:900
h:750
로봇청소기
411*497*441
타일 : 크러쉬 600*1200
554*1775*545
김치냉장고
오로라비스크 M612
네이처 문 그레이
554*1775*545
냉장전용고
554*1775*545
냉동전용고
3030
1200
3400
2200
인조대리석
225
600
225
1050
1005
필름마감
거실/주방
48.63㎡
14.71py
W3600*H1850(FL455)
시스템
암막 + 린넨속지
4000
60" (1450*900)
TV 반매립
250
457
1597
매입수전 (폰타나)
사틴무광계열~
전체신설
테라 600각
703
600
890
330
100
1030
30
리치브라운/브라운유리
원슬라이딩
1229
리버스톤브라운
1200*600
코드나인
300*300*1100
445
920
465
1820
1830
370
선반장+다용도
단올림
하부 골프백
중간 캐리어
브론즈거울
RS47
MAIN ENT
1260
500
760
+100단올림
900위 수납
LG워시타워
700*1890*830
상부장
배수유가
820
310
600
100
선반
샤워부스
전체신설
매입수전 (폰타나)
사틴무광계열~
705
거실욕실
3.48㎡
1.05py
현관
4.48㎡
1.36py
안방욕실
3.63㎡
1.1py
드레스룸
16.65㎡
5.04py
실외기실
1.63㎡
0.5py
붙박이장
A
붙박이장
A
붙박이장
9
거울도어
2889
800
1190
790
시스템옷장
2단
2단
790
서랍
시스템옷장
서랍
가구도어
710
550
방음시공
방화도어
실외기 950*834*330
1204
거울수납
화장대
서랍
콘+스
허니콤38MM(B038-104)
W1200*H1100(FL1215)
시스템 OR 이중창
439
우수관
852
젠st 슬라이딩도어
1712
1800
1200
750
1092
745
쇼케이스
535*1585*525
싱크대
W1800*H1450(FL1030)
우드(오동50MM-917)
시스템
차방
11.47㎡
3.47py
3089
1295
500
300
1295
201
100
침대헤드 h:1200
알판+필름 마감
불투명
모루유리
400
100
슈퍼싱글
1250*2100
슈퍼싱글
1250*2100
W1800*H1850(FL470)
암막 + 린넨속지
시스템
F 내부거울+넥타이
붙박이장
900
허니콤38MM(B038-104)
W1505*H1100(FL)
시스템
안방
14.17㎡
4.29py

12mm 도어로 전체교체
거실 마이너스걸레받이, 무몰딩
각 방 몰딩/걸레받이 모노베이지
도배 : 전체 디아망(마르모아 - 미스티웜그레이)
PR048-04
창호 : 라이트베이지 (RS35)
도어 : 모노베이지 (RS133)
바닥 : 에디톤 - 솔티크림 (EDT7725)
필름 : ML91 / 스위치콘센트 : 아테오 마그네슘
LX가구 : 셀렉션5 (네이처 문 그레이)
사재가구 : 보르떼 (세라믹 그레이 STN08)

DESIGN BY.

M2
디 자 인 엠 제 곱

@_m2design_
m2gmg@naver.com

REMARK.

SITE CONDITIONS.

ADDRESS.
제주시 첨단로동길 106
꿈에그린A3

AREA.
146.69m2 /44.37 py

HEIGHT.
2400mm(2300)

PROJECT TYPE.
아파트 리모델링

PROJECT TITLE.
꿈에그린 304-102

DRAWING TITLE.
평 면 도

SCALE.
A1:1/30 A3:1/60

DATE.
25.09.04

DRAWN BY.

CHECKED BY.

DRAWING No.

SHEET No.

- 본 도서는 어떠한 경우에도 무단으로 도용할 수 없으며 도용시 '지적재산권' 보호에 관한 법률에 의거, 법적 분쟁이 발생합니다. 또한 본 도서에 관한 모든 저작권은 당사에 있습니다. -

\\admin-pc01\공유폴더\■ 디자인엠제곱\01_현장\★250711_첨단꿈에그린304-102\02_도면\250904_꿈에그린304-102.dwg,2025-09-12 15:00:10,Microsoft P