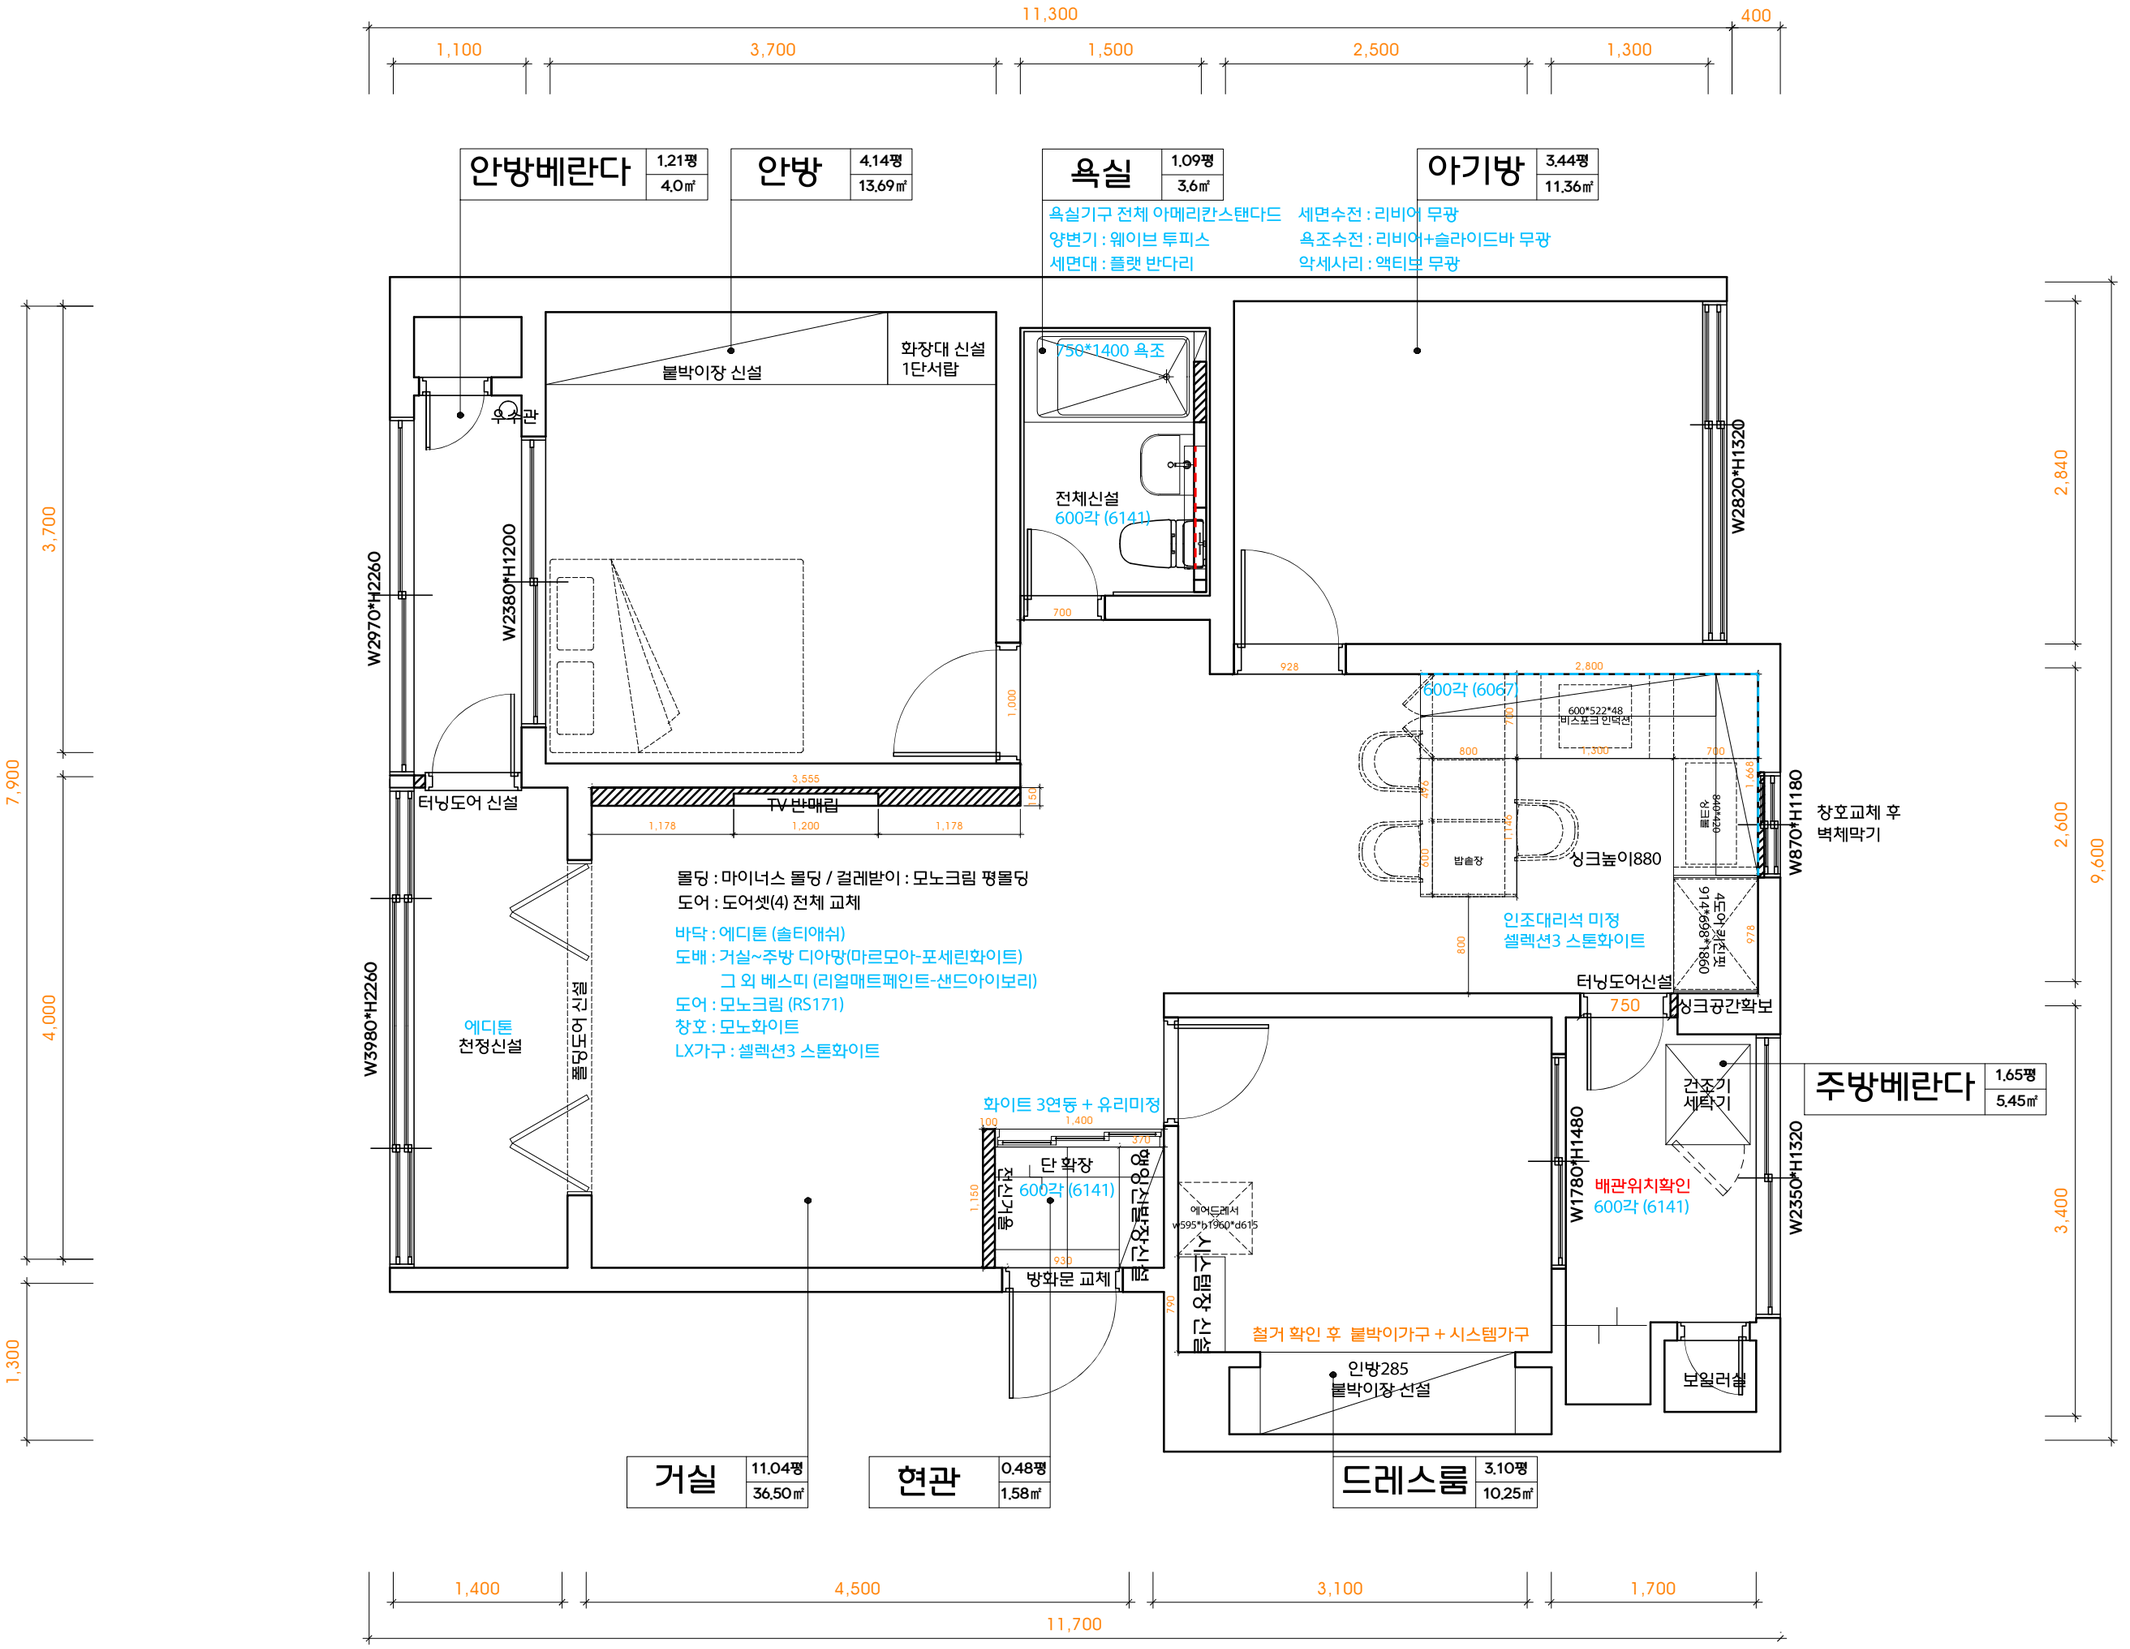


DESIGN BY.

M2
디 자 인 엠 제 곱

@_m2design_
m2gmg@naver.com

REMARK.

*철거

샷시-거실/안방/드레스룸 내창만 철거
도어-도어셋(5), 몰딩, 걸레받이, 문선, 문틀
타일-주방 벽/안방 베란다/현관/주방 베란다
욕실 - ubr 전체 철거
벽/바닥 타일 전체 철거
도기셋,천장,액세서리,욕조,수전,선반대
조명,환풍기 기타외
가구-안방 붙박이장, 드레스룸 붙박이장,
주방 상하부장, 냉장고장, 주방 키큰장
신발장, 주방 베란다 상부장
안방 베란다 공틀장 철거 확인 필요
기타-우물천장, A/C 부분 천장 철거,
거실 베란다 확장 부분 바닥, 현관 파티션 가벽,
주방 베란다 보일러실 도어만 철거, 현관 대리석,
조명, 스위치, 콘센트 외
장판철거
확장 부분 날개 벽 철거 여부 확인

SITE CONDITIONS.

ADDRESS.
제주시 태성로 23
일도성환아파트 102동 409호

AREA.
86.43m2 / 26.14py

HEIGHT.
2330mm(거실) / 2440mm(베란다)

PROJECT TYPE.
아파트 리모델링

PROJECT TITLE.
일도성환아파트 102-409

DRAWING TITLE.
평 면 도

SCALE.
A1:1/25 A3:1/50

DATE.
25.09.24

DRAWN BY.	CHECKED BY.
DRAWING No.	SHEET No.

\\admin-pc01\공유폴더\■ 디자인엠제곱\01_현장\★250717_일도성환아파트 102동 409호\02_도면\250924_일도성환아파트 102-409.dwg,2025-09-24 18:01:00

- 본 도서는 어떠한 경우에도 무단으로 도용할 수 없으며 도용시 '지적재산권' 보호에 관한 법률에 의거, 법적 분쟁이 발생합니다. 또한 본 도서에 관한 모든 저작권은 당사에 있습니다. -