
DESIGN BY.

GM
황 금 손 인 테 리 어

@__gmdesign__
goldenhand99@naver.com

REMARK.
* 신설부분 *
각방에어컨 4대 + 거실 1대 (5마력)
각방에어컨 출력 약한걸로 해서 맞추기
거실에만 욕스위치 사용
주방,거실 터닝도어 모노와이트
안방 터닝도어 라이트베이지
전체 창호 라이트베이지

조명(팬던트, 벽등), 욕실거울장(여닫이)

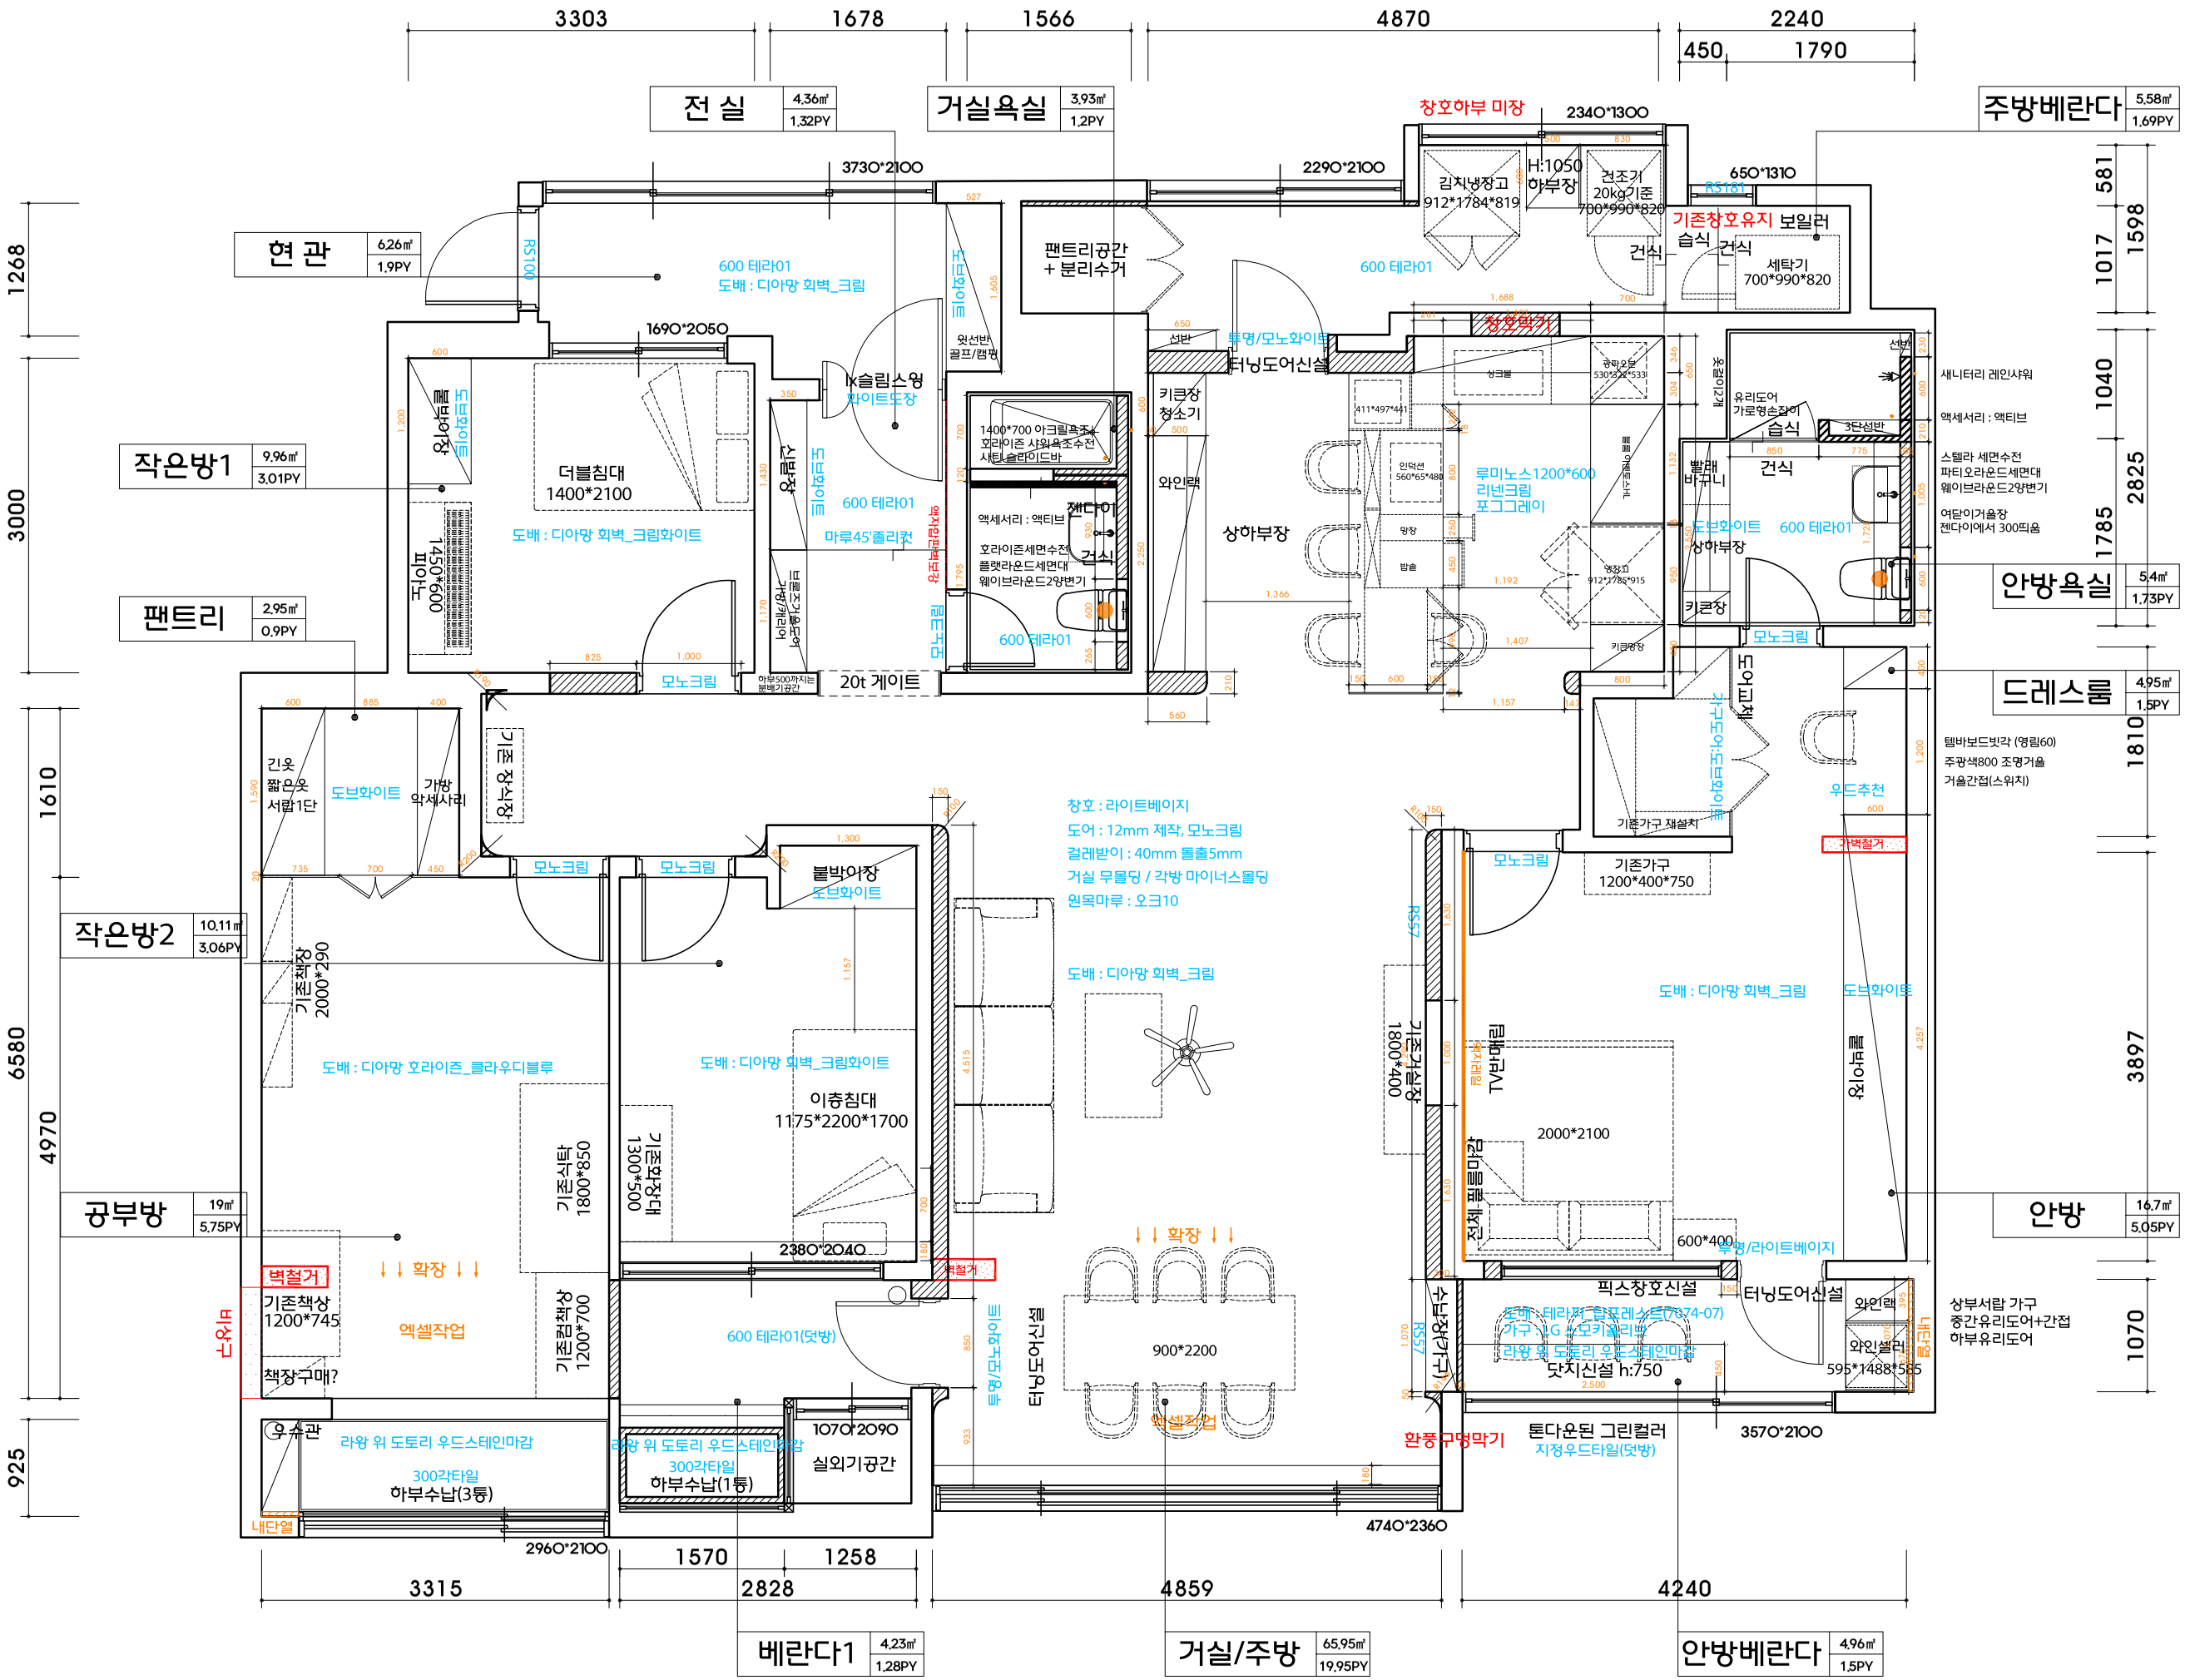

창호 : 라이트베이지
도어 : 12mm 제작, 모노크림
걸레받이 : 40mm 돌출5mm
거실 무몰딩 / 각방 마이너스몰딩
원목마루 : 오크10

조명/모노와이트
터닝도어신설
조명/라이트베이지
터닝도어신설
환풍구명막기
톤다운된 그린컬러
지정우드타일(덧방)

SITE CONDITIONS.
ADDRESS.
노형 대림 아파트
노형동 2585-2
AREA.
181.06 m2 / 54.77py
HEIGHT.
2280mm(최고2318mm)
PROJECT TYPE.
아파트 리모델링
PROJECT TITLE.
노형대림 103-1401
DRAWING TITLE.
평 면 도
SCALE.
A1:1/00 A3:1/60
DATE.
25.04.21
DRAWN BY.
CHECKED BY.
DRAWING No.
SHEET No.

- 본 도서는 어떠한 경우에도 무단으로 도용할 수 없으며 도용시 '지적재산권' 보호에 관한 법률에 의거, 법적 분쟁이 발생합니다. 또한 본 도서에 관한 모든 저작권은 당사에 있습니다. -