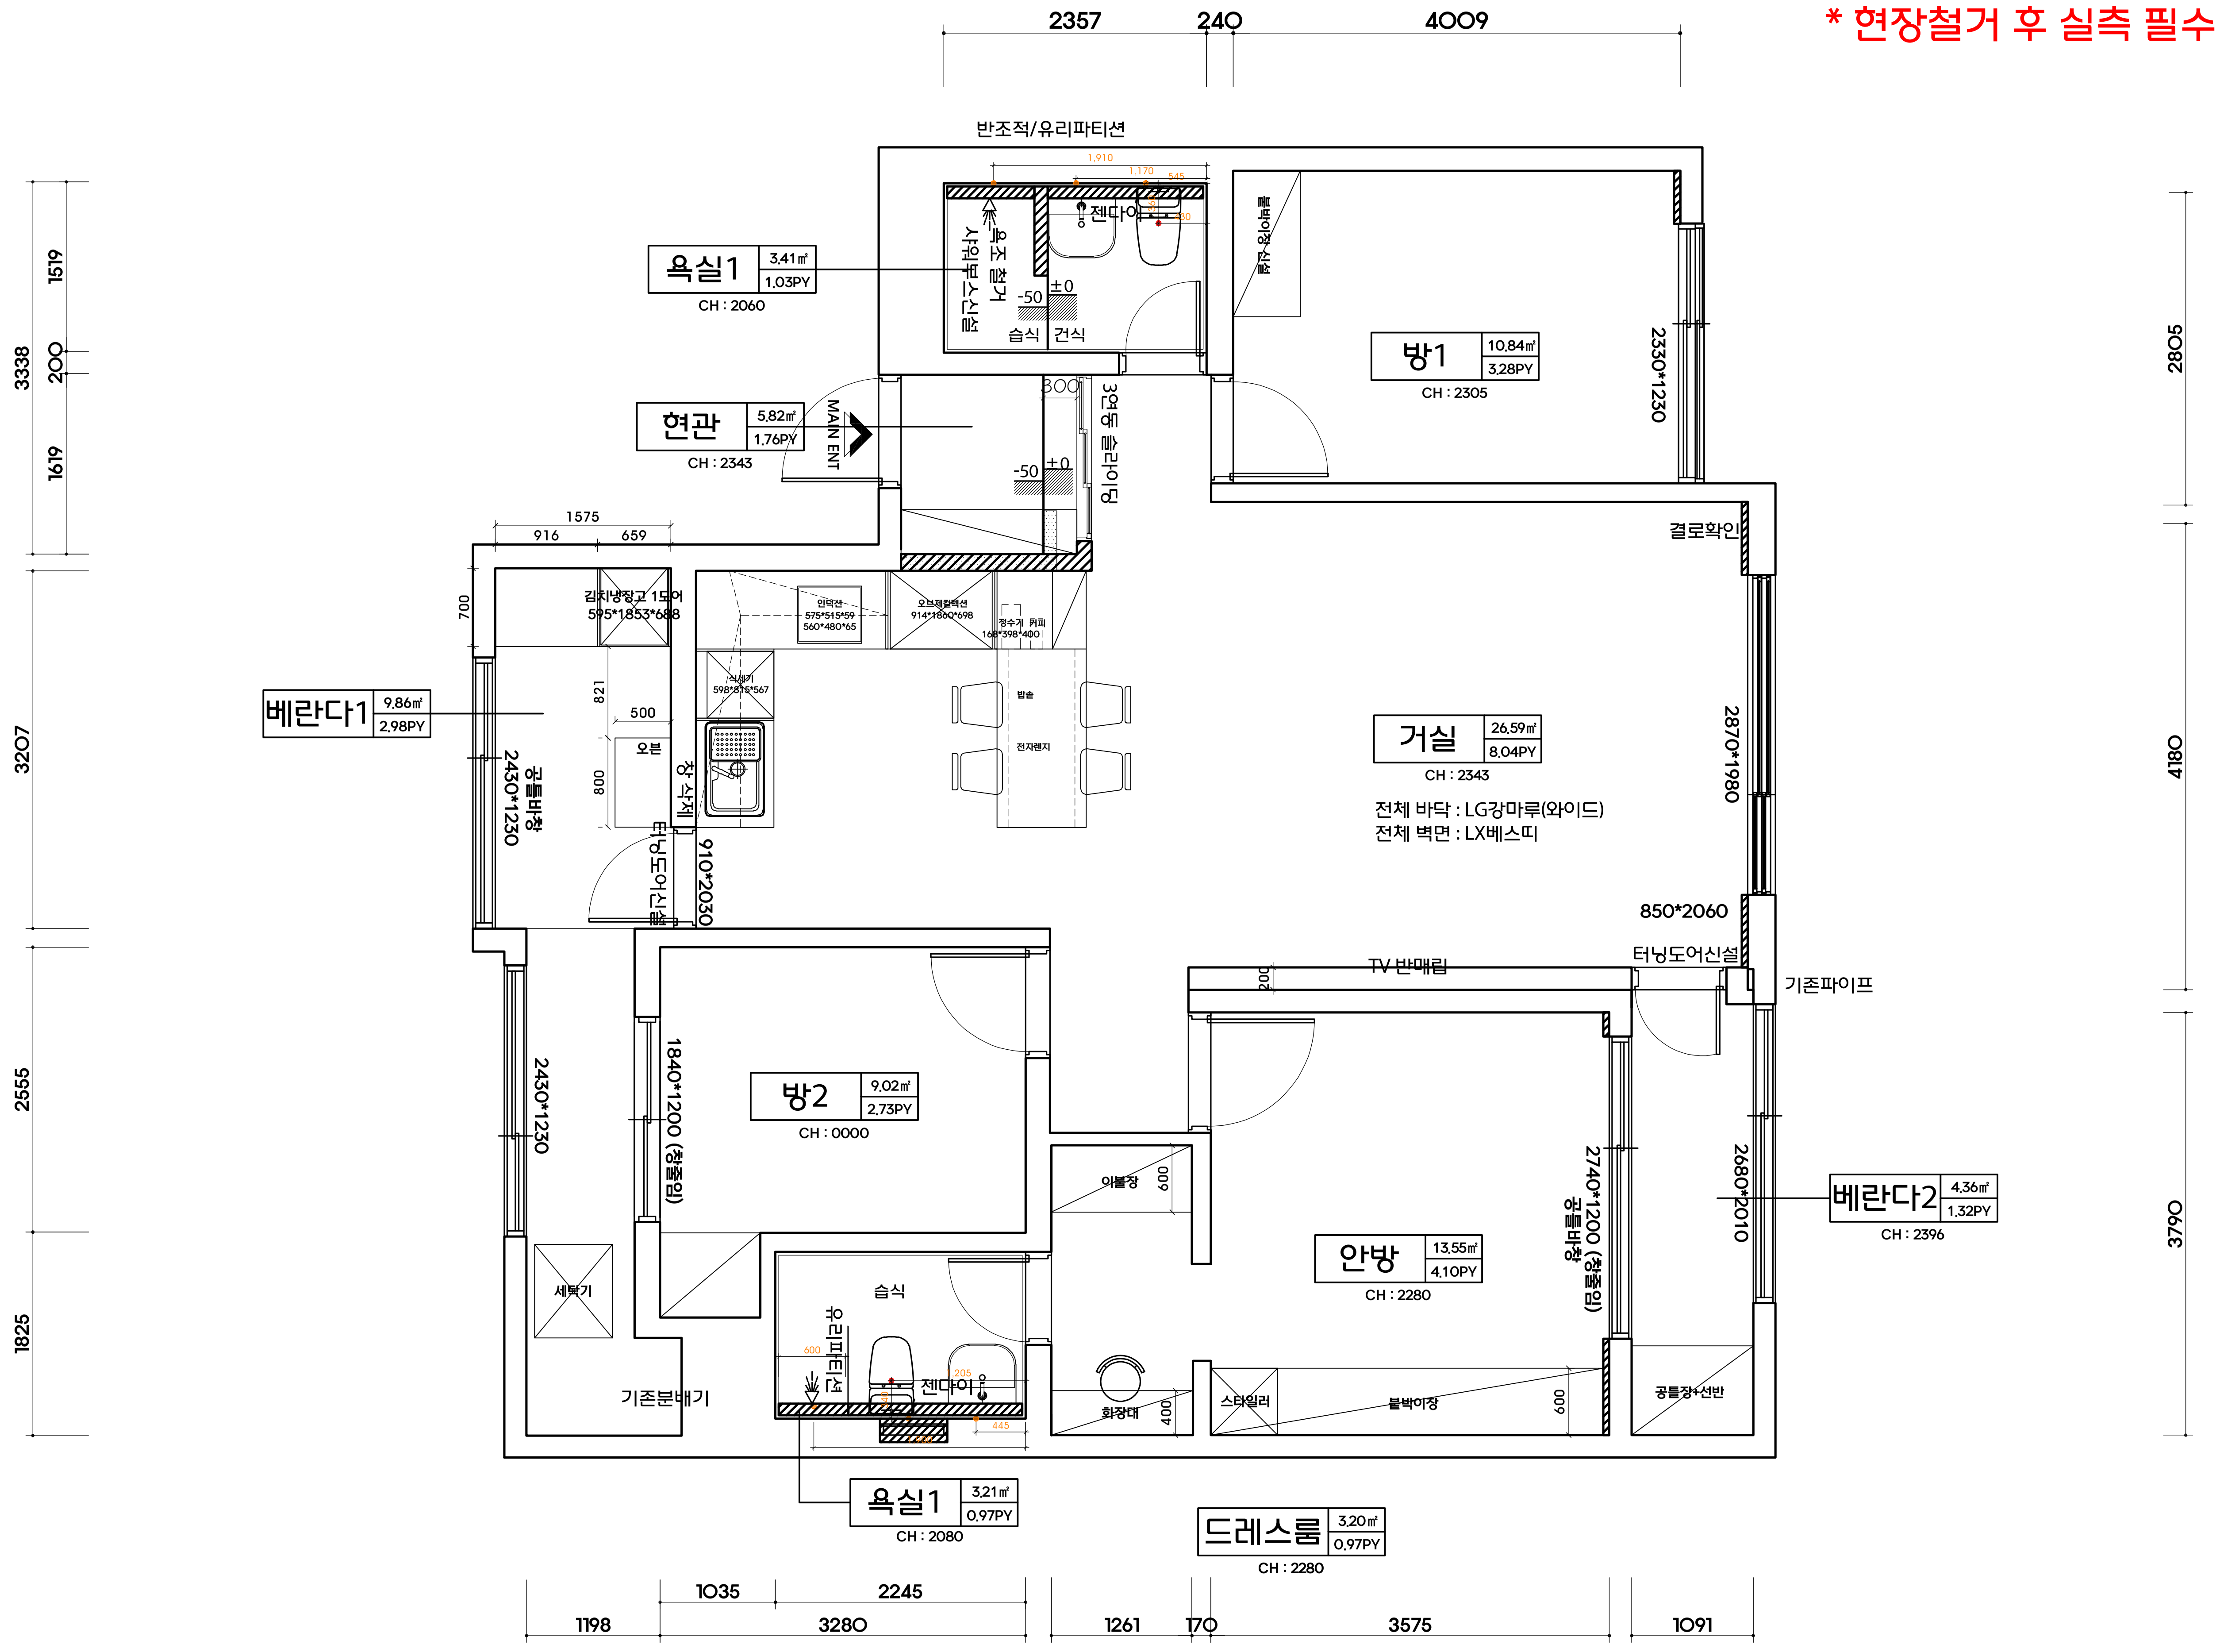
2357
240
4009
2805
4180
3790
3338
1519
200
1619
3207
2555
1825
1198
1035
3280
2245
1261
170
3575
1091
반조적/유리파티션
1,910
1,170
545
360
430
욕실1 3.41㎡ 1.03PY
CH : 2060
욕조 철거
샤워부스신설
젠다이
-50
±0
습식
건식
붙박이장 신설
방1 10.84㎡ 3.28PY
CH : 2305
2330*1230
현관 5.82㎡ 1.76PY
CH : 2343
MAIN ENT
300
3연동 슬라이딩
-50
±0
1575
916
659
700
김치냉장고 1도어
595*1853*688
인덕션
575*515*59
560*480*65
오브제컬렉션
914*1860*698
정수기 커피
168*398*400
식세기
598*815*567
밥솥
전자렌지
821
500
오븐
800
창 삭제
베란다1 9.86㎡ 2.98PY
공틀바창
2430*1230
터닝도어신설
910*2030
결로확인
거실 26.59㎡ 8.04PY
CH : 2343
전체 바닥 : LG강마루(와이드)
전체 벽면 : LX베스띠
2870*1980
850*2060
터닝도어신설
기존파이프
TV 반매립
200
2430*1230
1840*1200 (창출입)
방2 9.02㎡ 2.73PY
CH : 0000
이불장
600
안방 13.55㎡ 4.10PY
CH : 2280
2740*1200 (창출입)
공틀바창
2680*2010
베란다2 4.36㎡ 1.32PY
CH : 2396
세탁기
기존분배기
습식
유리파티션
600
340
1,205
445
1,900
젠다이
욕실1 3.21㎡ 0.97PY
CH : 2080
화장대
400
스타일러
붙박이장
600
공틀장+선반
드레스룸 3.20㎡ 0.97PY
CH : 2280

*** 현장철거 후 실측 필수 ***

DESIGN BY.

DESIGN M²

@__gmdesign__
goldenhand99@naver.com

PROJECT.

REMARK.
화이트 / 그레이 / 밝게

SITE CONDITIONS.

ADDRESS.
서사로 18길 16 시스빌 702호
아파트 7층

AREA.
100.39 m2 / 30.37py

HEIGHT.
2343mm(거실)

PROJECT TYPE.
아파트 리모델링

PROJECT TITLE.
시스빌 702호

DRAWING TITLE.
평 면 도

SCALE.
A1:1/00 A3:1/60

DATE.
24.05.20

DRAWN BY.	CHECKED BY.
DRAWING No. I-002	SHEET No. 001

– 본 도서는 어떠한 경우에도 무단으로 도용할 수 없으며 도용시 '지적재산권' 보호에 관한 법률에 의거, 법적 분쟁이 발생합니다. 또한 본 도서에 관한 모든 저작권은 당사에 있습니다. –