
ALT_1

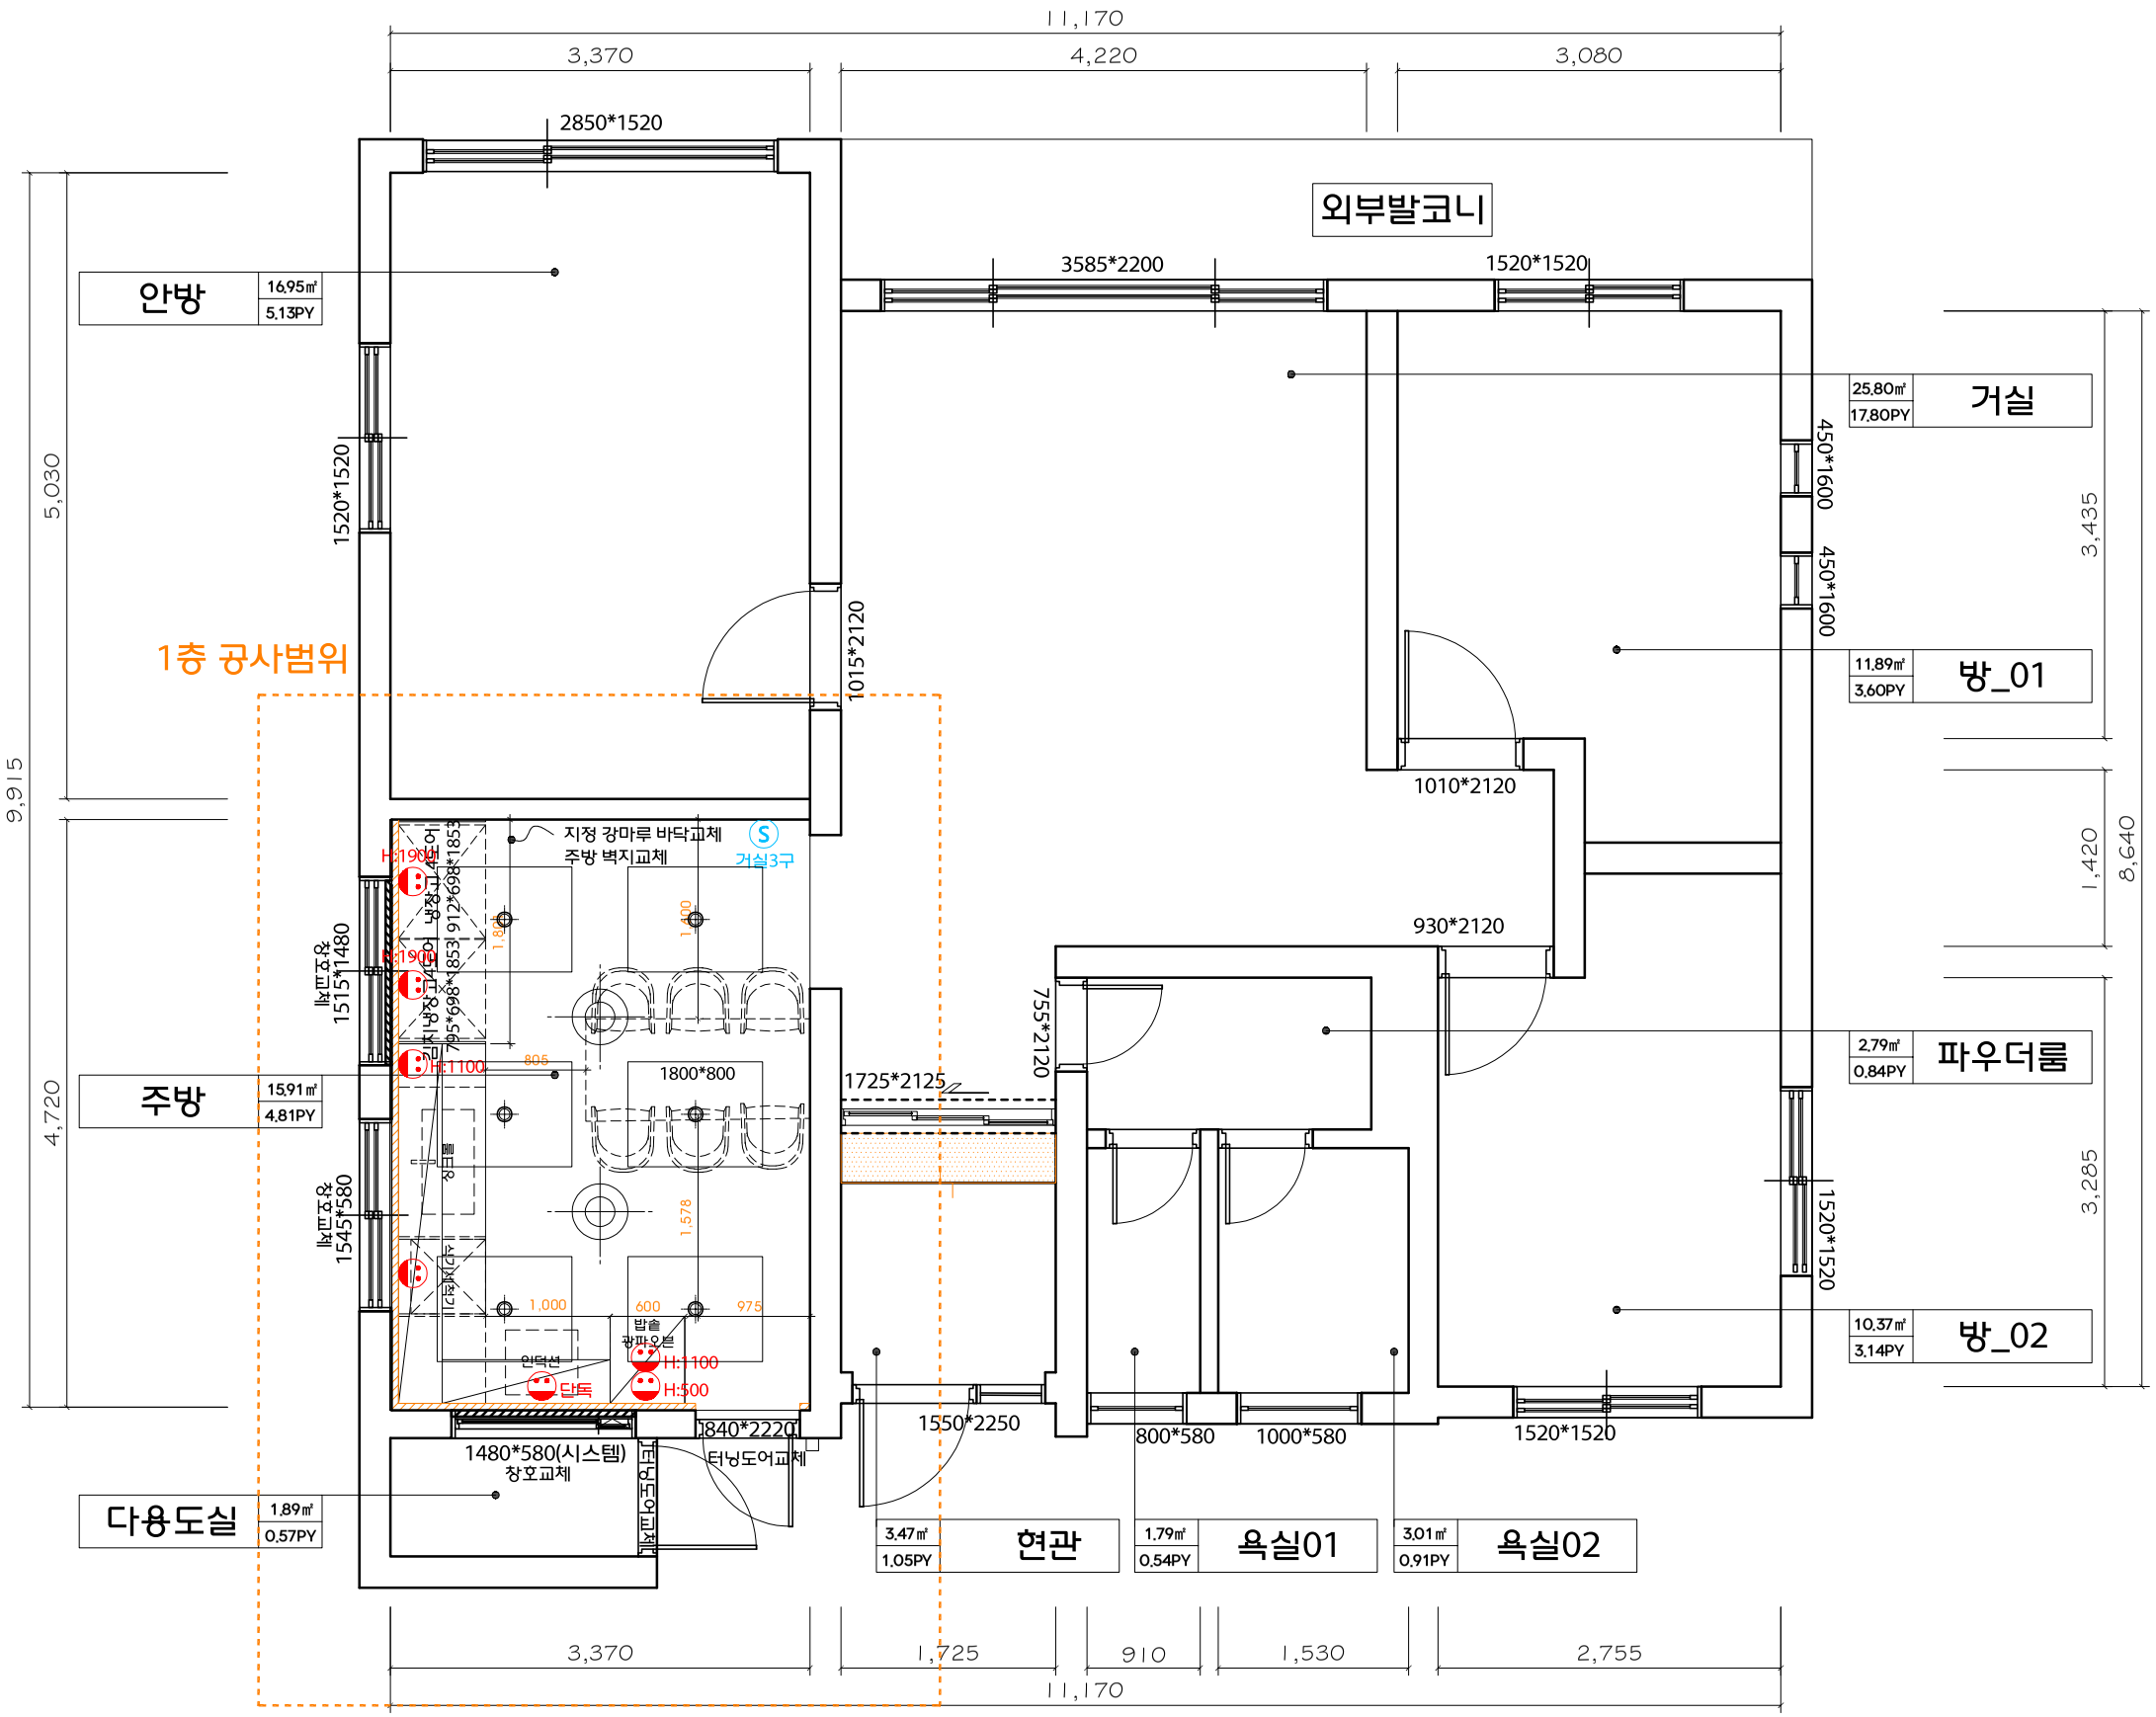

DESIGN BY.

GM
황 금 손 인 테 리 어

@__gmdesign__
goldenhand99@naver.com

PROJECT.

SITE CONDITIONS.

ADDRESS.
제주시 흥랑길 44-14
단독주택 1층

AREA.
103.29m2 / 31.23py

HEIGHT.
2610mm(거실),2470mm(방)

PROJECT TYPE.
주택 리모델링

PROJECT TITLE.
흥랑길 44-14

DRAWING TITLE.
평 면 도

SCALE.
A1:1/00 A3:1/60

DATE.
25.05.07

DRAWN BY.	CHECKED BY.
DRAWING No.	SHEET No.

- 본 도서는 어떠한 경우에도 무단으로 도용할 수 없으며 도용시 '지적재산권' 보호에 관한 법률에 의거, 법적 분쟁이 발생합니다. 또한 본 도서에 관한 모든 저작권은 당사에 있습니다. -