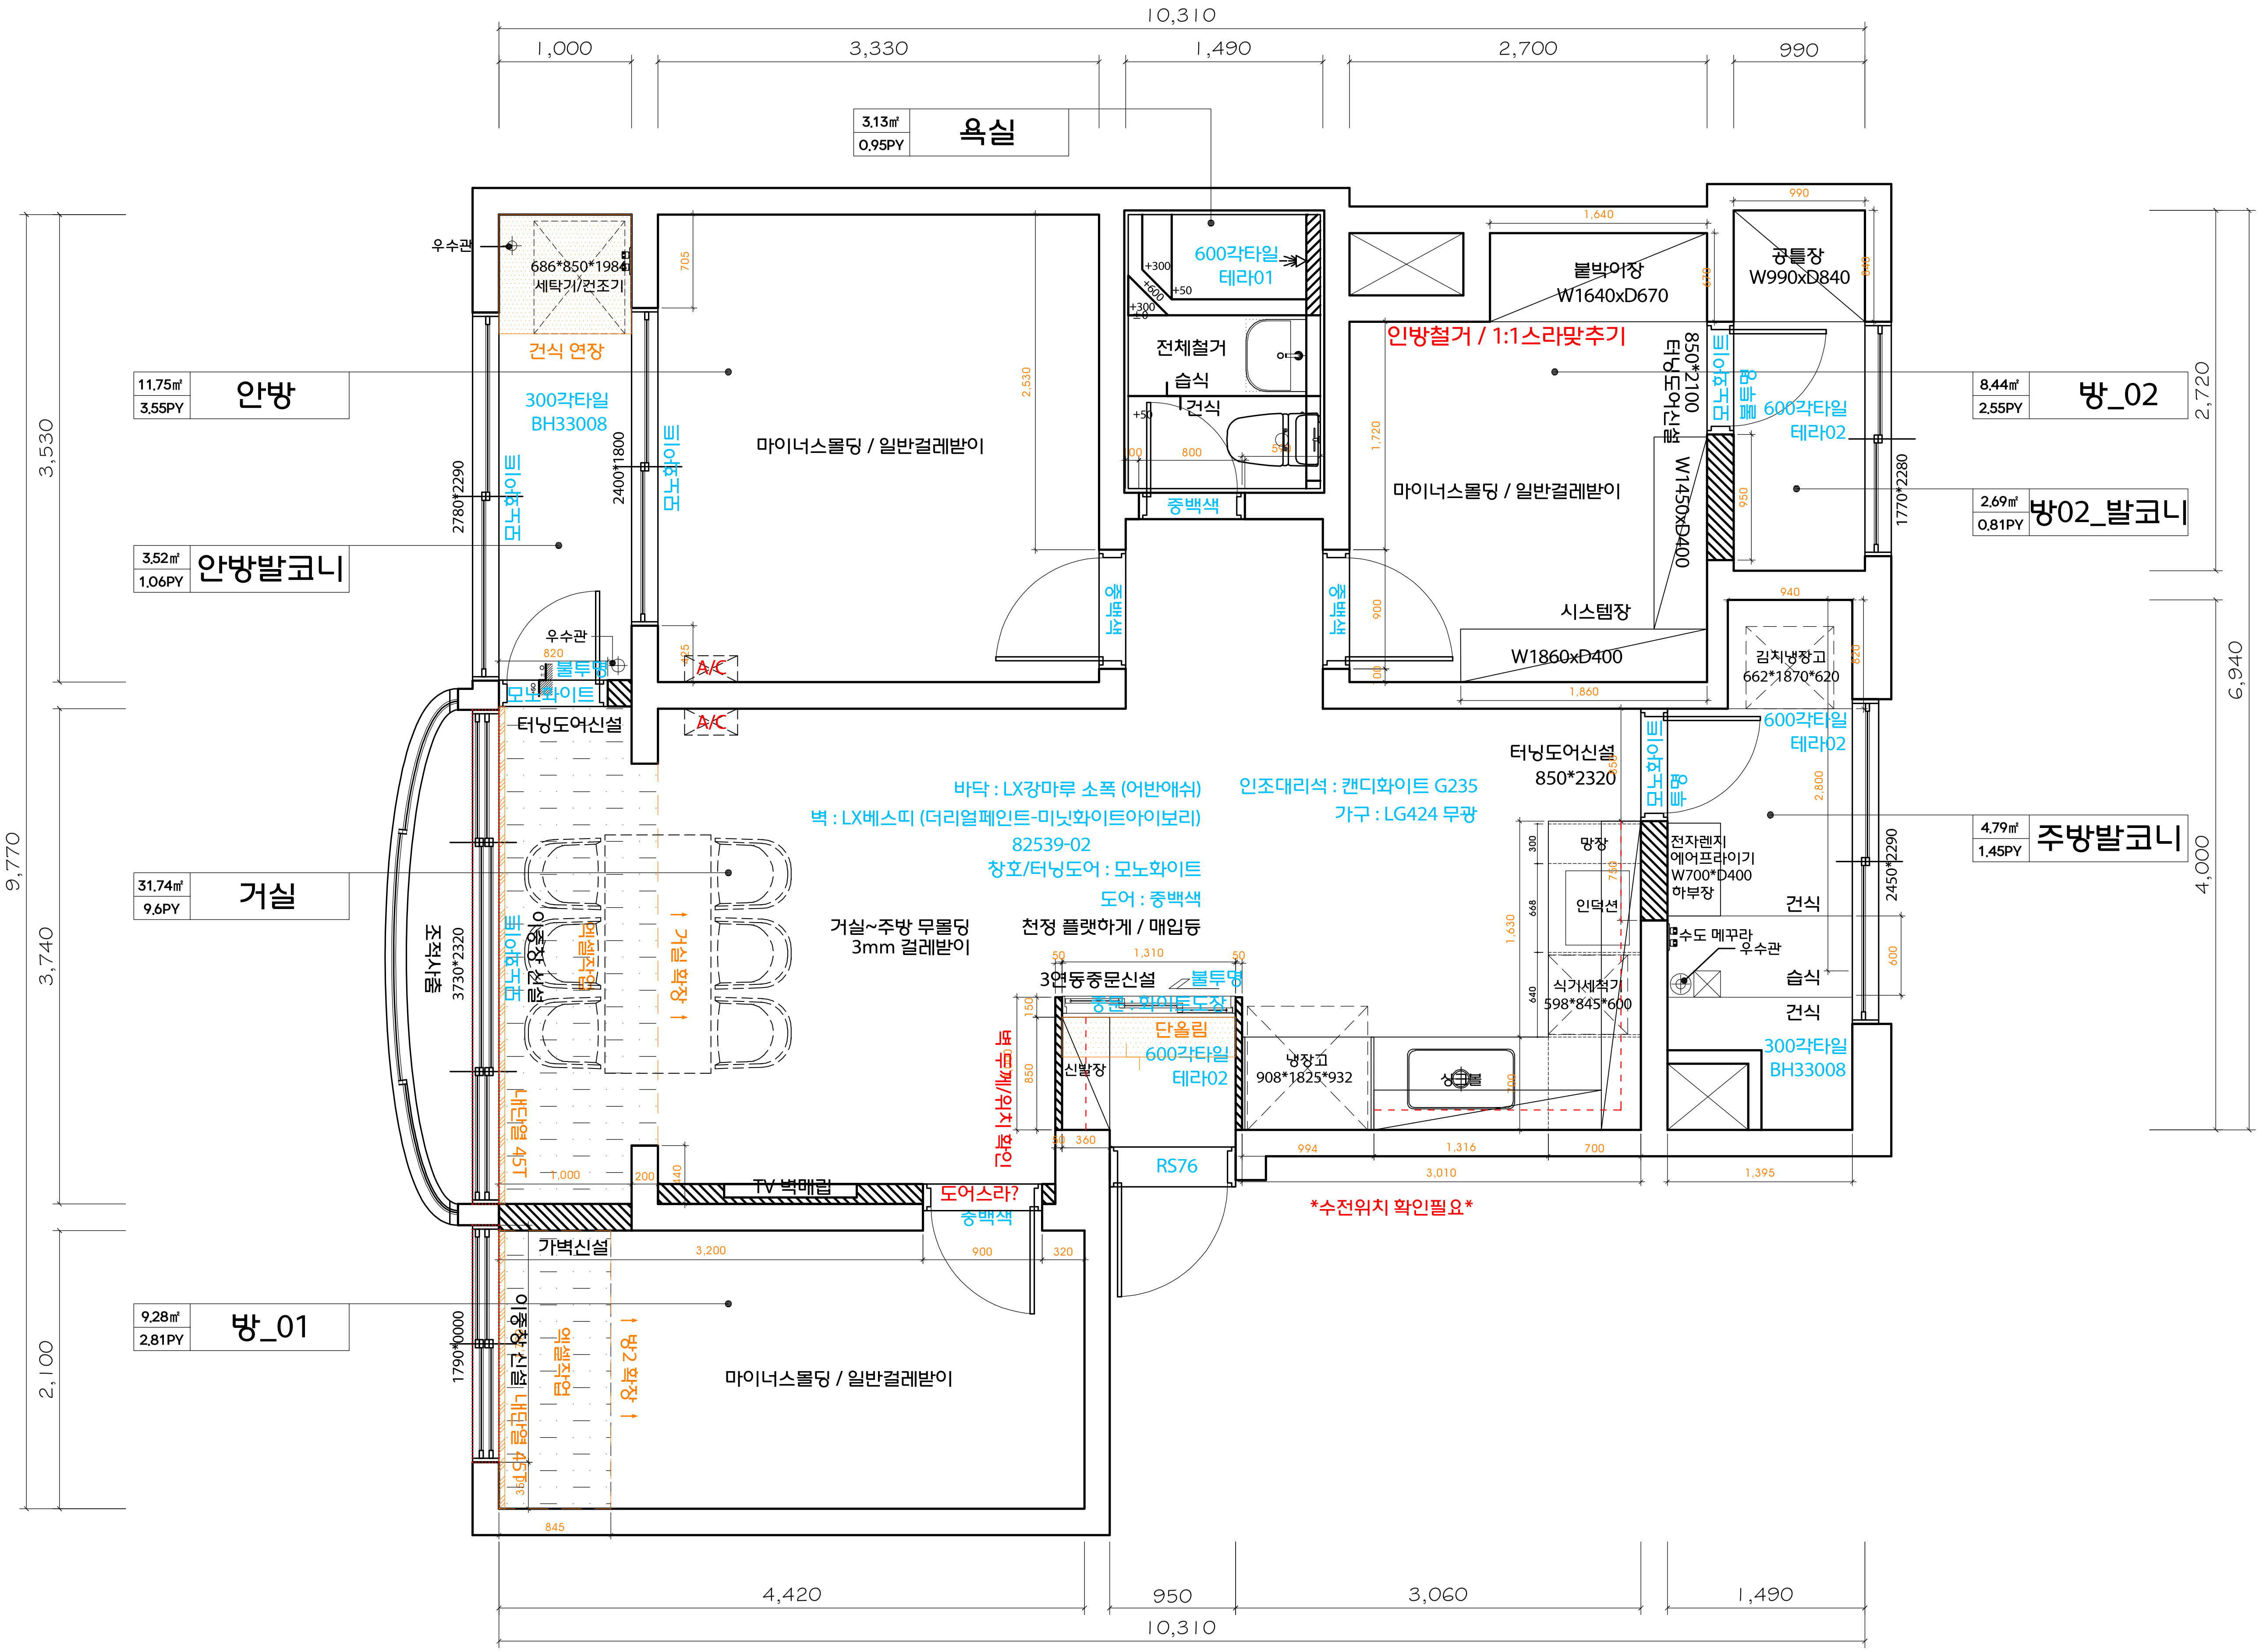
10,310
1,000
3,330
1,490
2,700
990
3,13㎡
0,95PY
욕실
우수관
686*850*1984
세탁기/건조기
건식 연장
705
11,75㎡
3,55PY
안방
300각타일
BH33008
2780*2290
2400*1800
모노화이트
마이너스몰딩 / 일반걸레받이
2,530
3,52㎡
1,06PY
안방발코니
우수관
820
불투명
모노화이트
터닝도어신설
A/C
A/C
600각타일
테라01
+300
+600
+300
+50
±0
전체철거
습식
건식
+50
100
800
590
중백색
중백색
중백색
900
100
1,720
1,640
붙박이장
W1640xD670
670
990
공틀장
W990xD840
840
인방철거 / 1:1스라맞추기
850*2100
터닝도어신설
모노화이트
불투명
600각타일
테라02
8,44㎡
2,55PY
방_02
2,69㎡
0,81PY
방02_발코니
1770*2280
950
W1450xD400
시스템장
W1860xD400
1,860
940
김치냉장고
662*1870*620
820
600각타일
테라02
모노화이트
불투명
2,800
터닝도어신설
850*2320
850
바닥 : LX강마루 소폭 (어반애쉬)
벽 : LX베스띠 (더리얼페인트-미닛화이트아이보리)
82539-02
창호/터닝도어 : 모노화이트
도어 : 중백색
인조대리석 : 캔디화이트 G235
가구 : LG424 무광
거실~주방 무몰딩
3mm 걸레받이
천정 플랫하게 / 매입등
31,74㎡
9,6PY
거실
조적사춤
3730*2320
모노화이트
이중창 신설
벽체작업
↑ 거실 확장 ↑
내단열 45T
1,000
200
440
TV 벽매립
도어스라?
중백색
3연동중문신설
불투명
중문 : 화이트도장
1,310
50
50
150
850
50
360
단올림
600각타일
테라02
신발장
벽 두께/위치 확인
RS76
냉장고
908*1825*932
망장
300
668
640
1,630
750
인덕션
식기세척기
598*845*600
싱크볼
700
994
1,316
700
3,010
수전위치 확인필요
전자렌지
에어프라이기
W700*D400
하부장
건식
수도 메꾸라
우수관
습식
건식
300각타일
BH33008
600
2450*2290
1,395
4,79㎡
1,45PY
주방발코니
9,28㎡
2,81PY
방_01
가벽신설
3,200
900
320
1790*0000
이중창 신설
내단열 45T
벽체작업
↑ 방2 확장 ↑
마이너스몰딩 / 일반걸레받이
845
3,530
3,740
2,100
9,770
2,720
4,000
6,940
4,420
950
3,060
1,490
10,310

DESIGN BY.

GM
황 금 손 인 테 리 어

@__gmdesign__
goldenhand99@naver.com

PROJECT.

* 철거부분
도어 : 도어 4개, 창호(내창) 3개
창호도어 2개
현관 : 신발장
거실 : 확장(내창, 바닥, 천정), 장판
주방 : 싱크대, 베란다 창호도어
주방베란다 : 가구일체
거실베란다 : 가구일체
안방 : 가구일체
방1 : 가구일체, 확장(내창,바닥,천정),내창
안방발코니 :
방2 : 가구일체, 확장(바닥,천정),내창
욕실 : 전체철거

비브랜드 제품이여도 니켈로
에어컨은 스탠드/벽걸이형

SITE CONDITIONS.

ADDRESS.
해오름아파트
104동 1401호

AREA.
81.71m2 / 24.72py

HEIGHT.
2300mm(거실)

PROJECT TYPE.
아파트 리모델링

PROJECT TITLE.
해오름104동 1401호

DRAWING TITLE.
평 면 도

SCALE.
A1:1/00 A3:1/50

DATE.
25.03.05

DRAWN BY.

CHECKED BY.

DRAWING No.

SHEET No.

– 본 도서는 어떠한 경우에도 무단으로 도용할 수 없으며 도용시 '지적재산권' 보호에 관한 법률에 의거, 법적 분쟁이 발생합니다. 또한 본 도서에 관한 모든 저작권은 당사에 있습니다. –